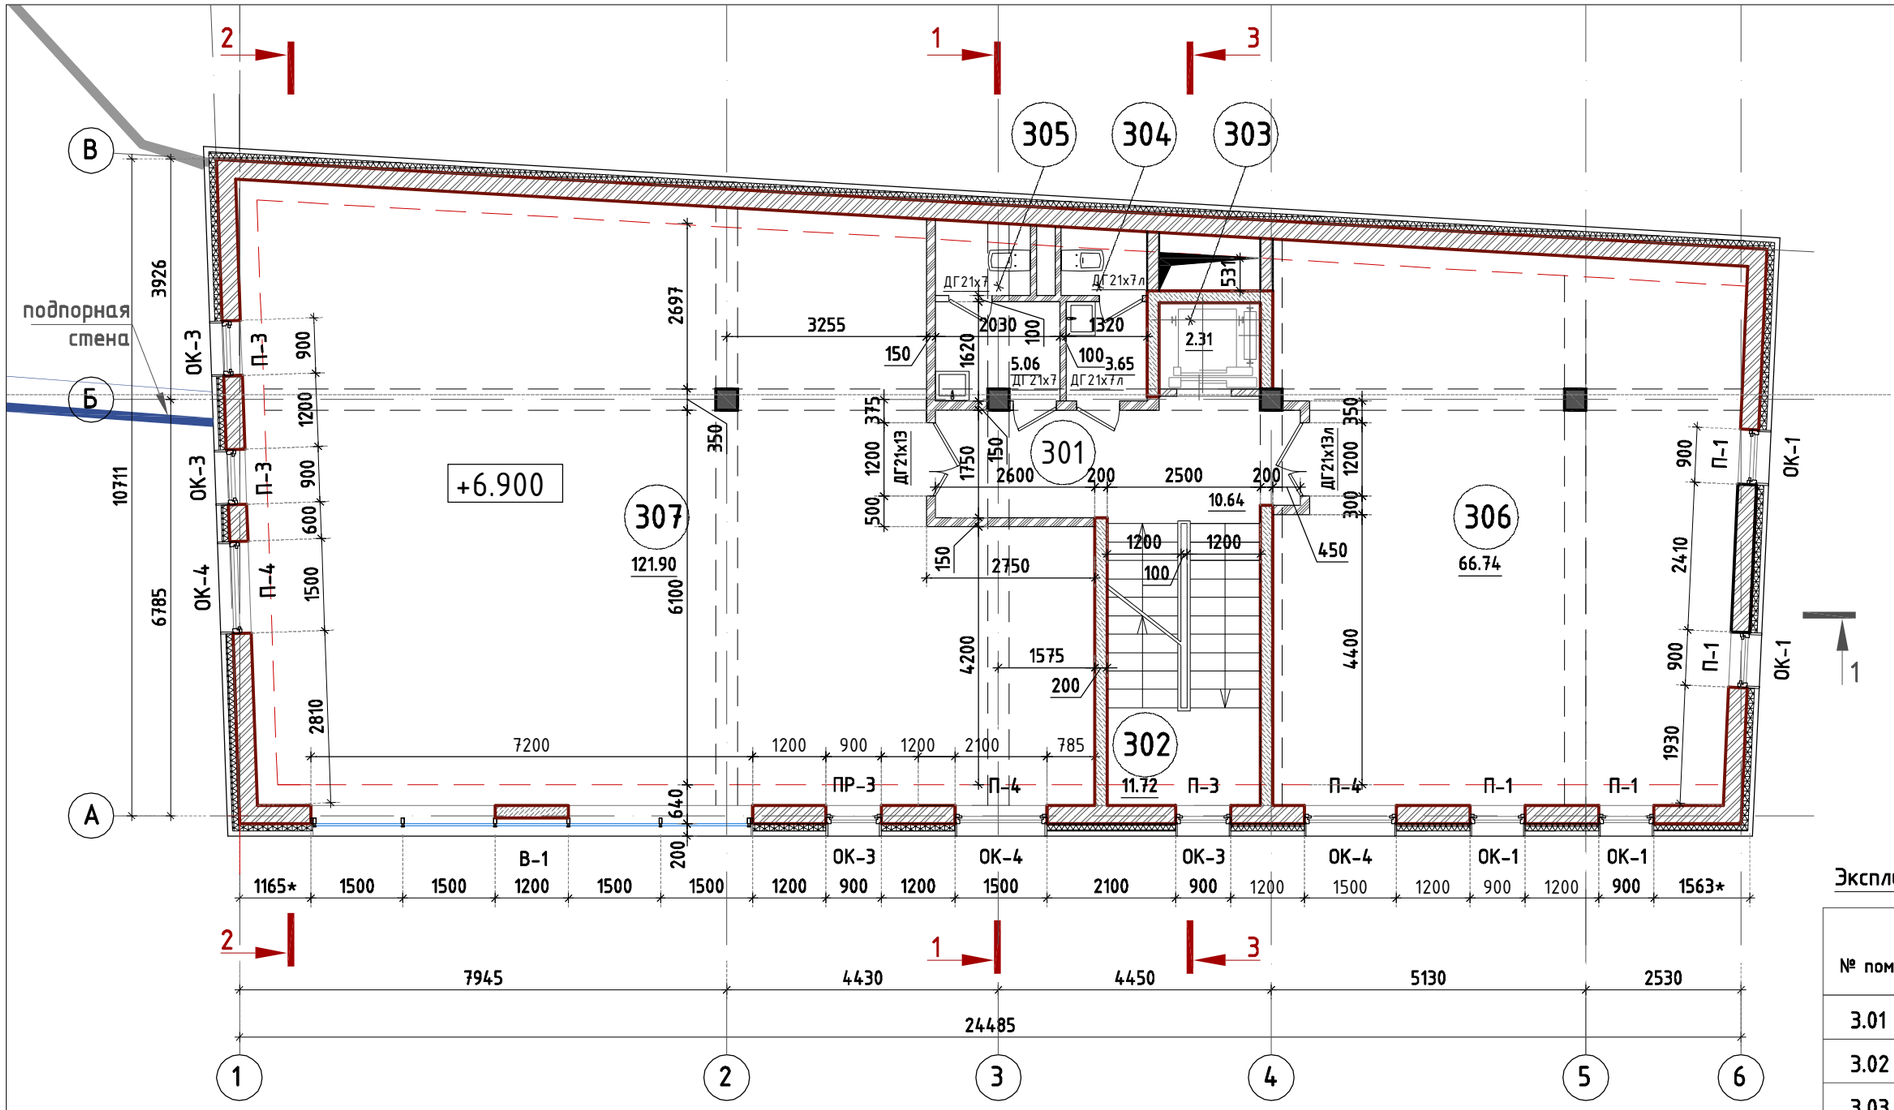

Экспликация помещений 3 этаж на отм. +6.600

№ пом.	Наименование помещений	Площадь, кв.м.
3.01	Холл	10.64
3.02	Лестница №1	11.72
3.03	Лифт №1	
3.04	Сан узел	3.65
3.05	Сан узел	5.06
3.06	Офис	66.74
3.07	Офис	121.90
	Итого	221.62

Условные обозначения

1		Монолитный железобетон
2		Стены из керамзитобетона (М100*см.КЖ) 190 мм
3		Кирпичная стена 640/520 мм
4		Кирпичная перегородка 120/250 мм
5		Утеплитель., Минераловатные плиты = 100 кг/т3 типа " Rockwool Venti-Batts" 180 мм*
6		Гипсокартонная водостойкая перегородка 100/150 мм
7		Контур демонтажа
8		Контур балок

Изм.	Кол.уч.	Лист	Nдок.	Подпись	Дата
Директор					
ГИП		Рягузов			
ГАП		Язмурадова			
Проверил		Рягузов			

** АР

Заказчик: ЗАО "АЛЬЯНСТРАНССТРОЙ"

Проект реконструкции Административного здания, по адресу: г. Москва,ЦАО,Нововаганьковский пер.,д.3,стр.2

Стадия	Лист	Листов
Р	10	

план 3-го этажа на отм.+6.900

ЗАО"АЛЬЯНСТРАНССТРОЙ