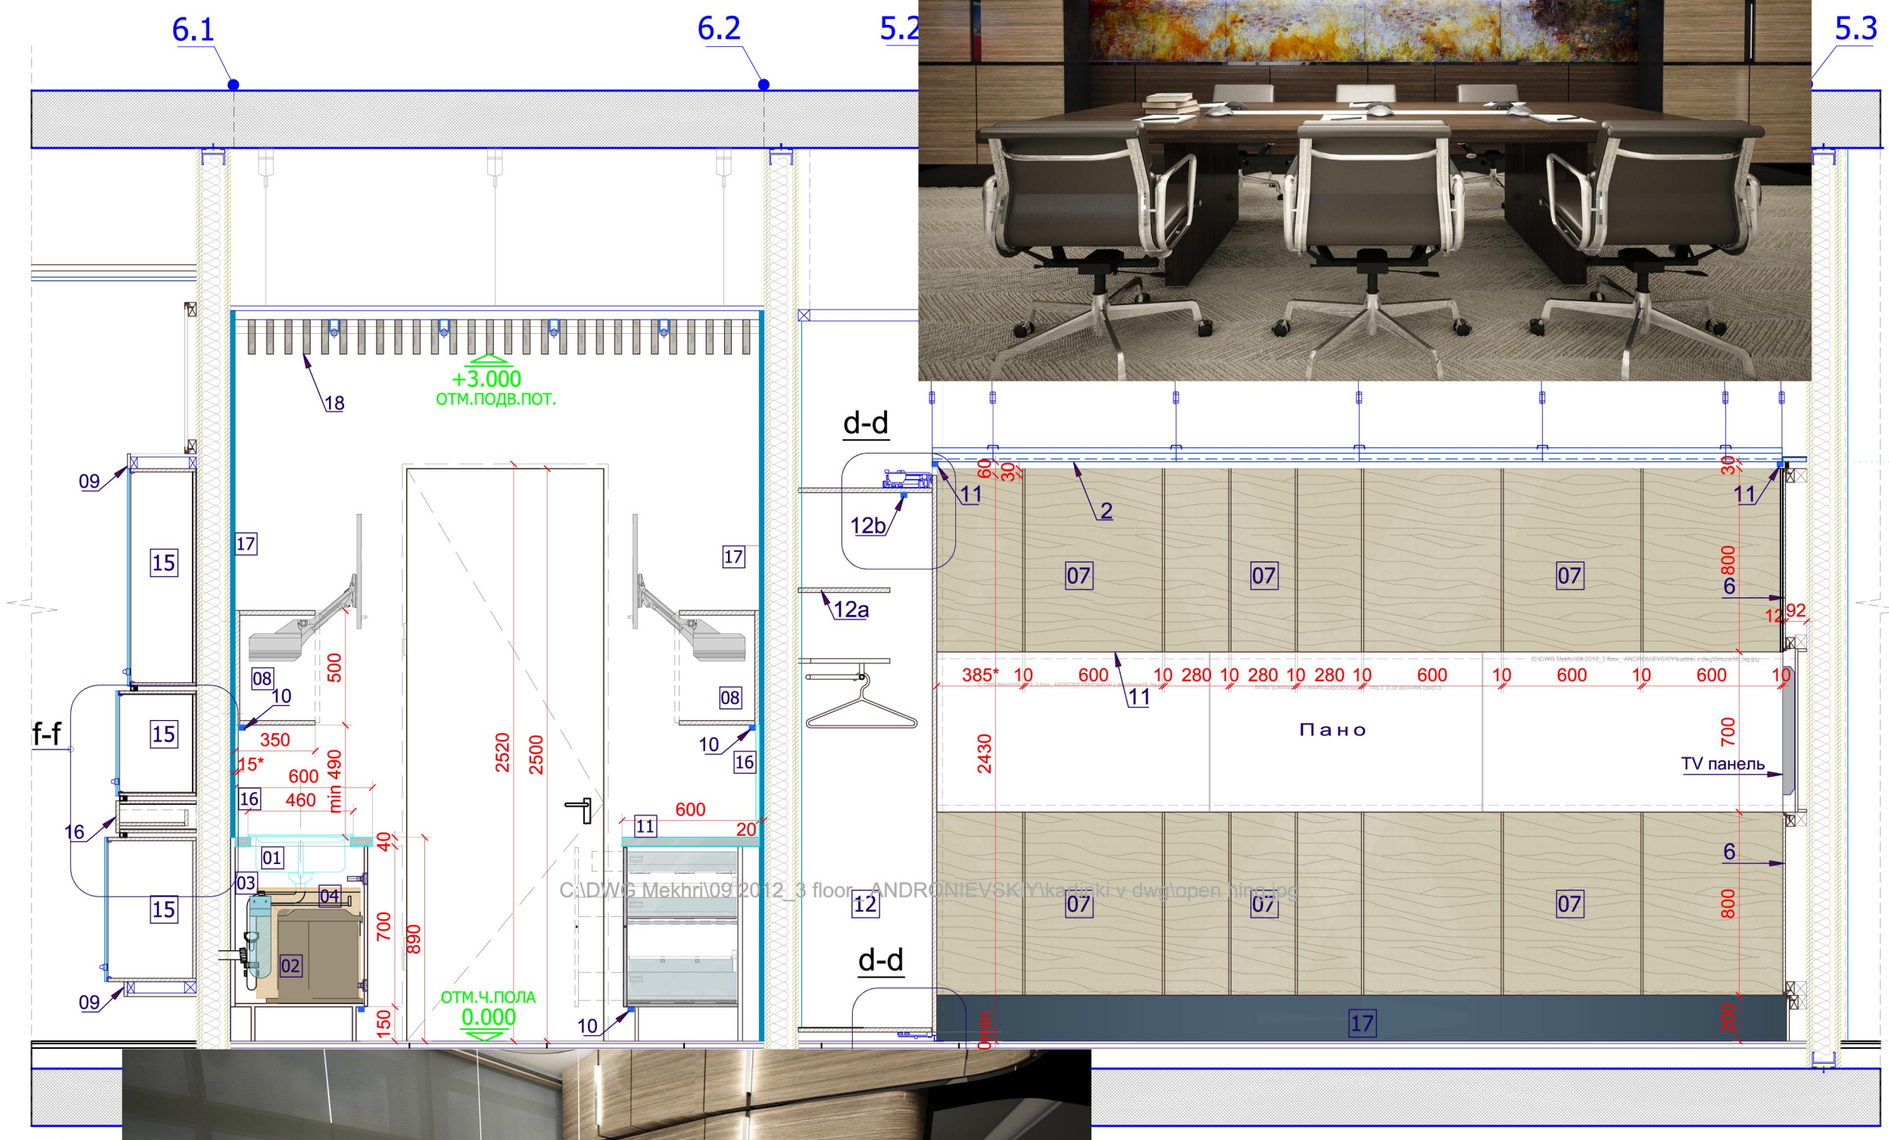

Развер
Зона о

f-f

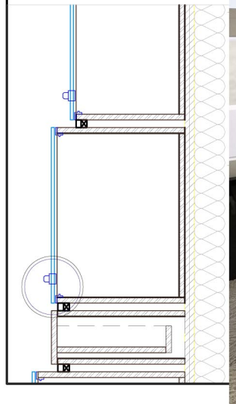

Данный лист читать совместно с листом 12,15,16, 23

M1:25

Изм.	Кол.	Лист	№док.	Подпись	Дата
ен.директор		Маркович			
АП		Язмурадова			
изайнер		Барышников			
роверил					
Н. контр.					

Заказчик:ОАО "Сбербанк"

АИ

Залы ОПЕРУ
г. Москва ул. Большая Андроньевская, д. 8

3 этаж

Стадия	Лист	Листов
Р	28	

Зона отдыха №5, мини-кухня №6 .,
Развертка 6.1-6.2, 5.2-5.3 ., схема
расскладки деревянных панелей

Felix Markovich
АРХИТЕКТУРНО-КОНСТРУКТОРСКОЕ БЮРО

на возводимых перегородок

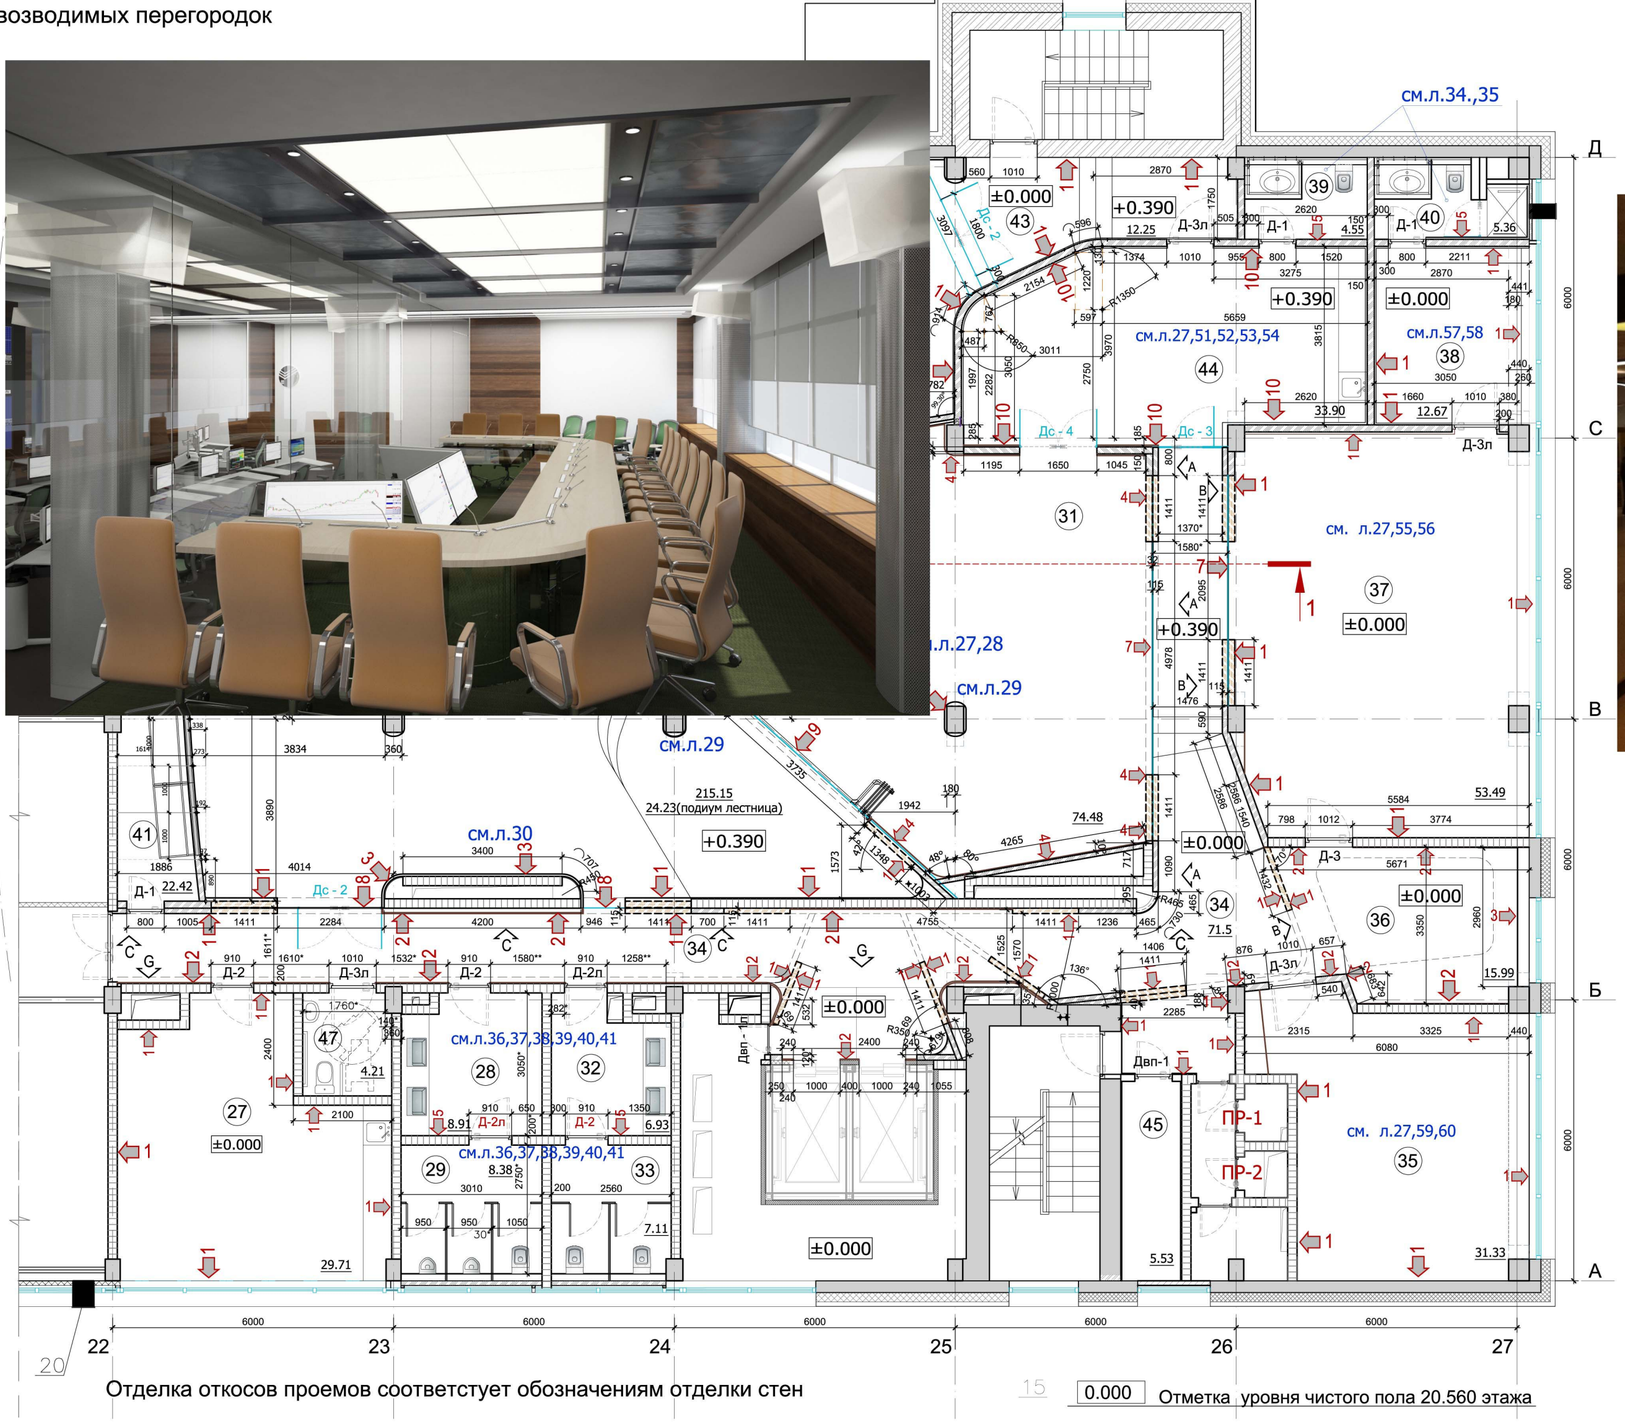

Отделка откосов проемов соответстует обозначениям отделки стен

Номер помещ.	Наименование	Площадь, м 2
27	Кухня	29.71
28	Тамбур	8.91
		8.39
		215.15
		74.48
		6.93
		7.11
		71.50
		31.33
		15.99
		53.49
		12.67
		3.87
		4.81
		22.42
		12.25
44	Приемная / комната для сопровождающих	33.90
45	Техническое коридор	5.53
47	С/узел для инвалидов	4.21
	Общая площадь	622.65

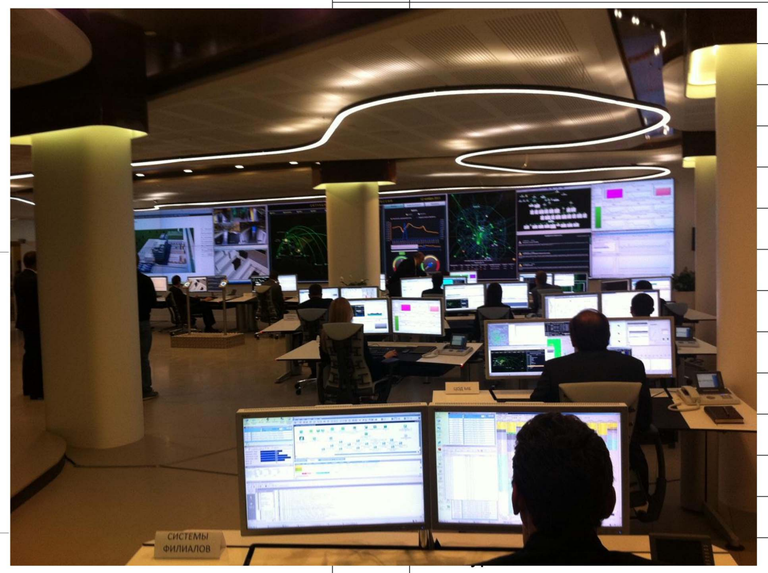

Условные обозначения

1		Стена из ячеистых блоков
2		Монолитный железобетон
3		Гипсокартонная водостойкая перегородка 150 мм См.альбом техн. решений изготовителя
4		Кирпичная кладка
5		Гипсокартонная перегородка переменной высоты

1.Гипсокартонные перегородки см. совместно с альбомом технических решений изготовителя

(металлические профили направляющих для монтажа Марка ПН-4 Марка ПС-4 75х40х0.55)

(Марка ПУ-2 31Х31Х0.55)

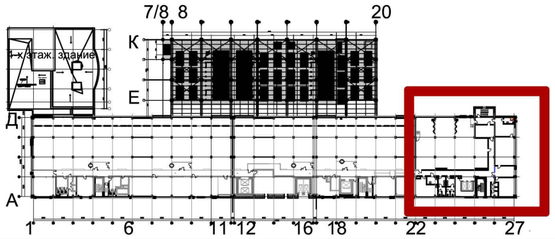

М 1:100

ные обозначения материалов

		Стены, колонны, перегородки
		Декоративное покрытие, Ral *
		Обои из дублированного шпона Casaleno
		Стеновые панели "DuPont Corian" Artic Ice
		Стеновые панели покрытие под дерево "Ровингер "
		Керамический гранит (см л. 23-24)

6	1.Экран
7	Стеклянная панель, из безопасного стекла с фурнитурой из шлифованной нерж. стали.пленка-графическим рисунком(матовый)
8	Стеклянная панель, из безопасного стекла с графическим рисунком (кубики прозрачные)
9	DORMA HSW-G - передвижная цельностеклянная перегородка из панелей с верхними и нижними шинами и открытыми боковыми кромками стекла.
10	Стеновые панели из гипса

Сечение по перегородкам см. лист 25,27

Изм.	Кол.	Лист	№док.	Подпись	Дата
Ген.директор		Маркович			
ГАП		Язмурадова			
Архитектор		Барышников			
Проверил					
Н. контр.					

Заказчик:ОАО "Сбербанк"

Комплекс инженерно-технических систем Мегавычислительного центра ОАО "Сбербанк России" по адресу: Москва, 2-й Южнопортовый проезд, 12А, корпус 1, стр.2

ситуационный центр Единого центра обработки данных (МегаЦОД)"

Стадия	Лист	Листов
И	06	

План отделки стен
Плана возводимых перегородок

Felix Markovich
АРХИТЕКТУРНО-КОНСТРУКТОРСКОЕ БЮРО

Фрагмент развертки

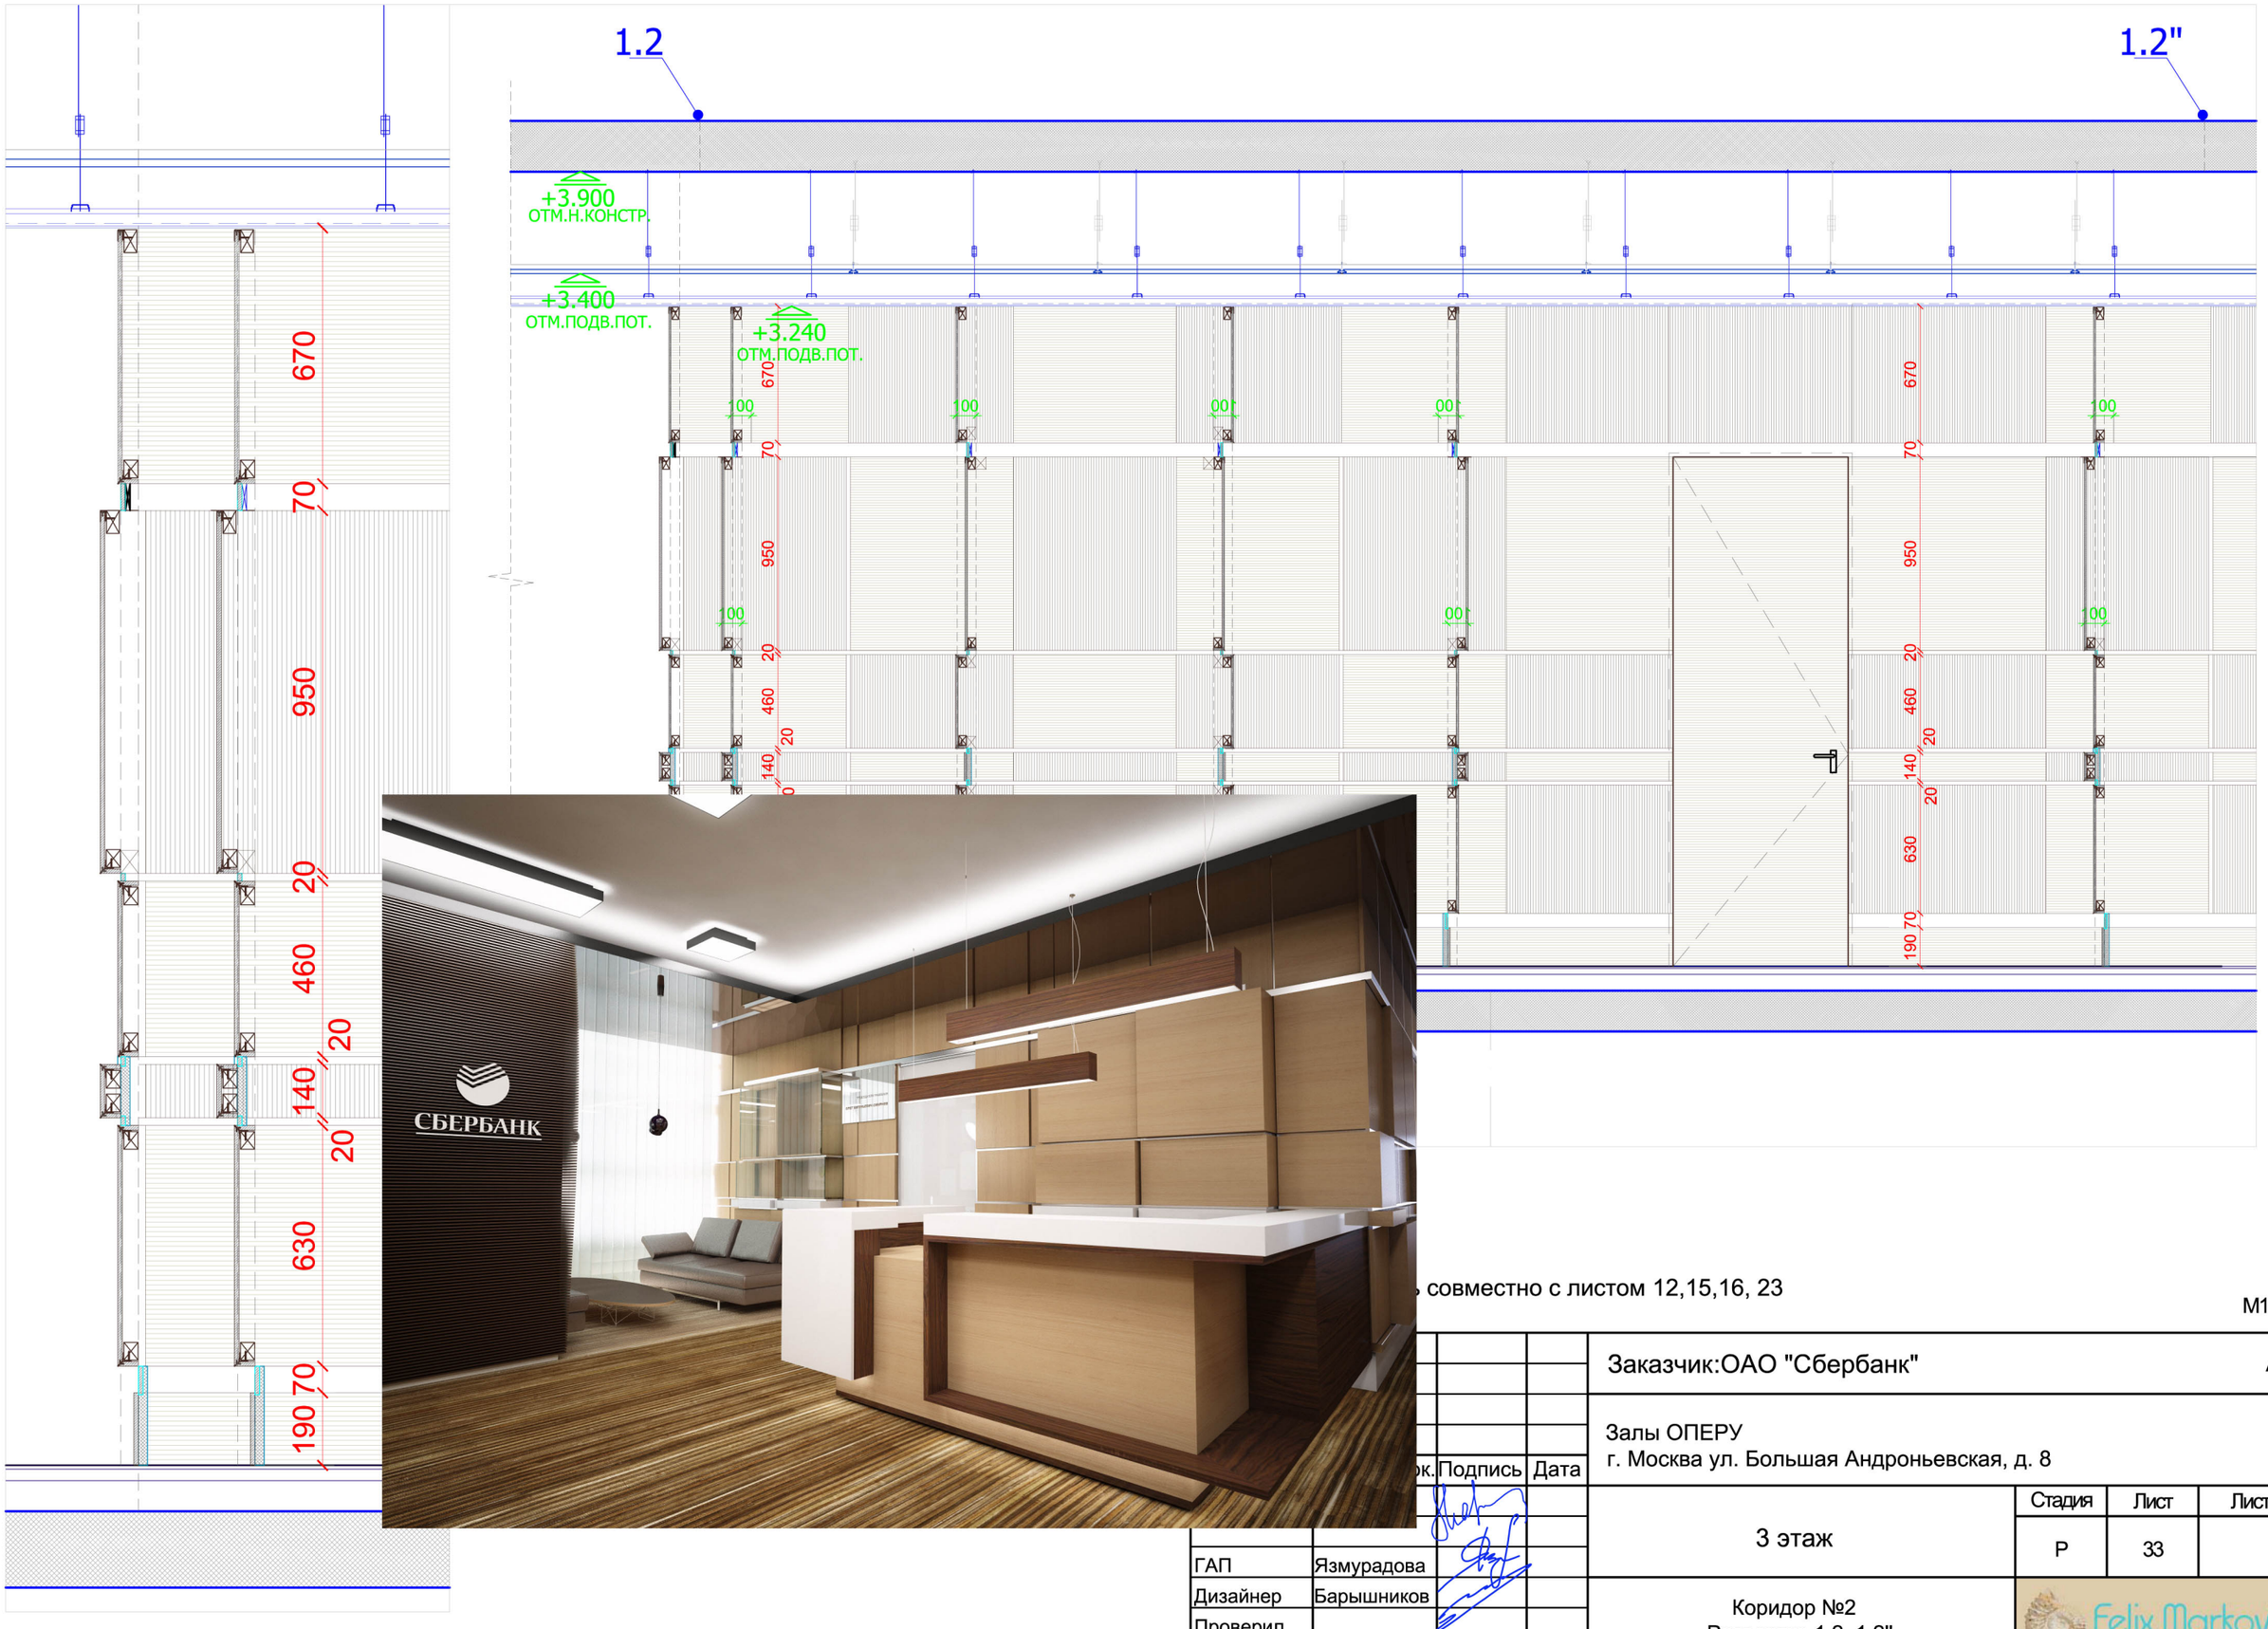

совместно с листом 12,15,16, 23

М1:30/15

				Заказчик:ОАО "Сбербанк" АИ
				Залы ОПЕРУ г. Москва ул. Большая Андроньевская, д. 8
				3 этаж — Стадия: Р; Лист: 33; Листов:
ГАП	Язмурадова			Коридор №2 Развертка 1.2, 1.2"
Дизайнер	Барышников			Felix Markovich АРХИТЕКТУРНО•КОНСТРУКТОРСКОЕ БЮРО
Проверил				
Н. контр.				

ок. Подпись Дата

План этажа с расстановкой выключателе

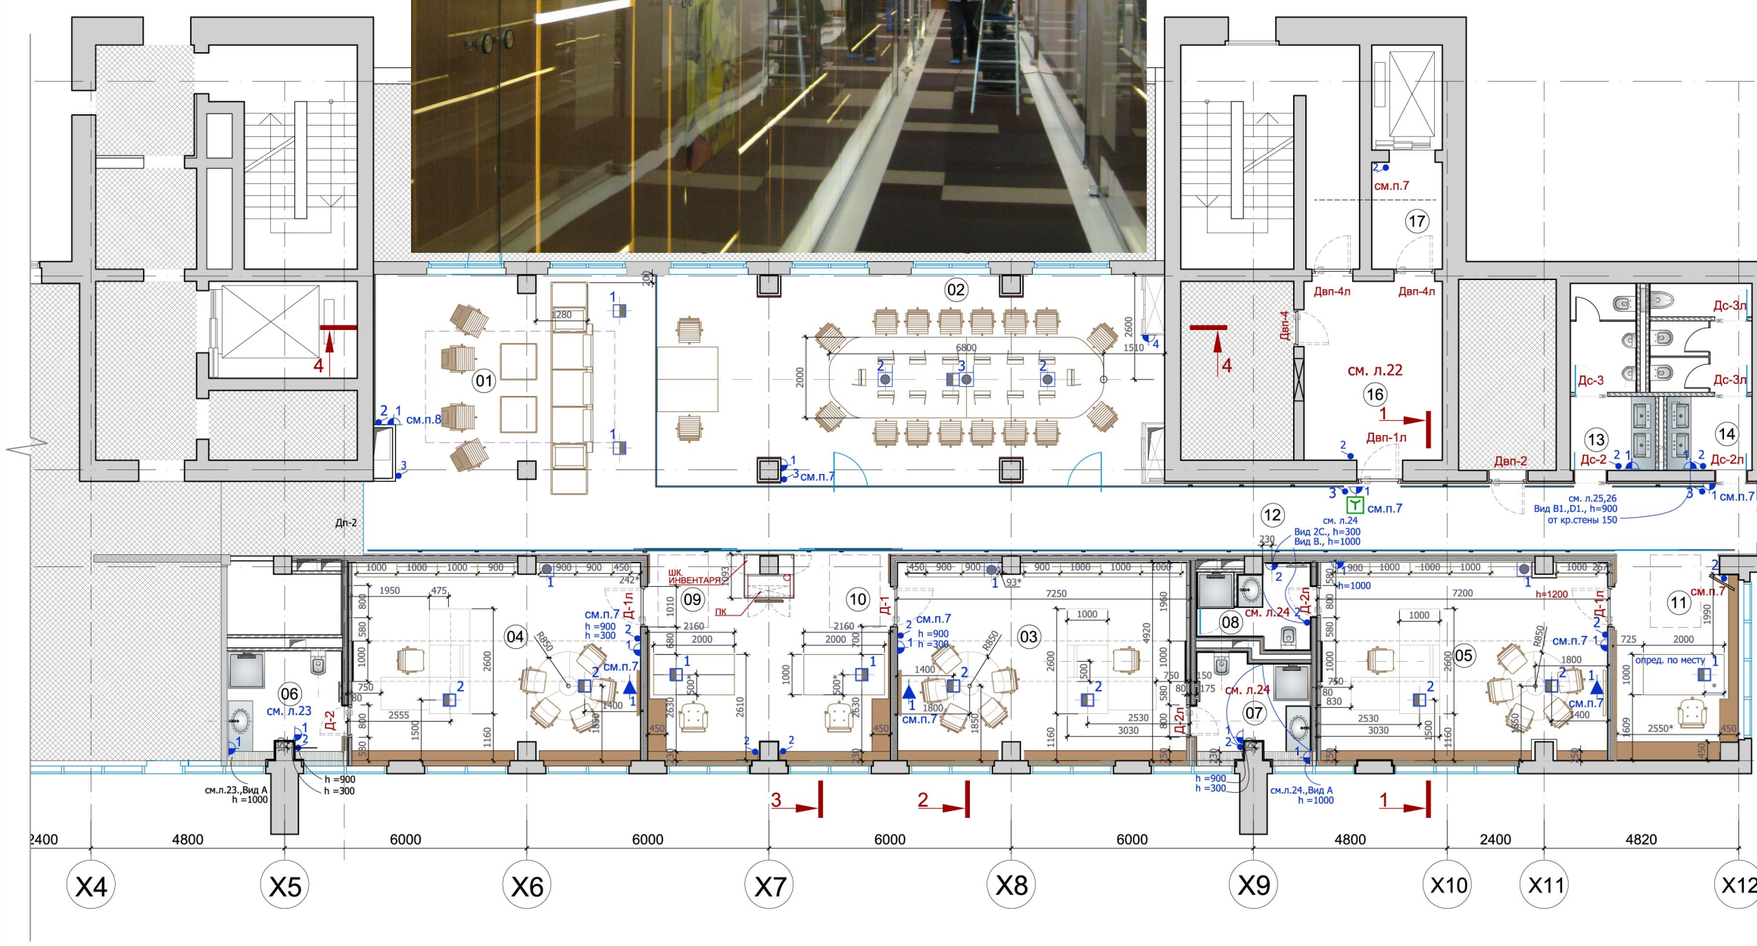

1	Зона рекреации	35.83
2	Переговорная	64.90
3	Кабинет руководителя	35.34
4	Кабинет руководителя	35.34
5	Кабинет руководителя	34.53
6	Сан. узел	7.34
7	Сан. узел	7.32
8	Сан. узел	5.22
9	Приемная	15.28
10	Приемная	15.28
11	Приемная	15.42
12	Коридор	61.32
13	Сан. узел мужской	8.56
14	Сан. узел женский	10.95
16	Лифтовой холл	15.19
17	Лифтовой холл	4.6

УСЛОВНЫЕ ОБОЗНАЧЕНИЯ ЭЛ.РОЗЕТОК/ВЫКЛЮЧАТЕЛЕЙ:

Обозначение	Наименование	Количество
1	2	3
n	блок розеток на 1 рабочее место n-означает кол-во блоков, к рабочему месту кабель проходит в меб. кабельканале	1, 2, 1
n	блок розеток оргтехника n-означает кол-во блоков	1, 2
n	Лючок электрический в полу n-означает кол-во блоков	1, 2, 1
n	Блок розеток в мебели n-означает кол-во блоков	1, 2, 1
n	розетка силовая компьютерная 220V ИБП (Источник бесперебойного питания) n - означает количество розеток	
n	розетка силовая бытовая 220V n - означает количество розеток	
n	телевизионная розетка	
n	слаботочная розетка RJ 45 n - означает количество розеток	
n	слаботочная розетка RJ 45 n - означает количество розеток	
n	розетка силовая бытовая с защитой от брызг 220V	
	эл. вывод 220V местоположение **уточняется проектом поставщика оборудования**	
N	Пульт вкл. потолочных и настенных осветительных приборов	

n — стандартный одноклавишный выключатель; n-указывает число выключателей

n — стандартный переключатель; n-указывает число переключателей

LCD Panel HD Beo vision 10* "BaNG &OLUFSEN

n — Регулятор климатконтроля; n-указывает число регуляторов.

обозначения групп включения сетильников

обозначения групп включения сетильников в режиме "ночного освещения"

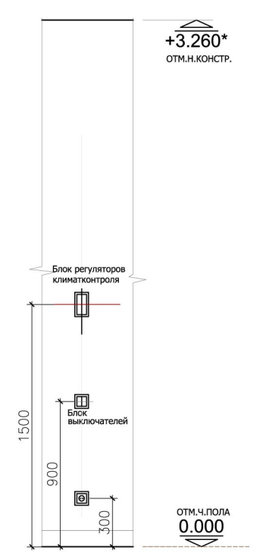

Общие указания

1. Этот чертеж смотри совместн
   и соответствующими инжене

2. За отметку ±0.000 принята отметка уровня чистого пола этажа.

3. Высота расположения розеток, розеточных групп на стенах и перегородках Н=300мм от уровня чистого пола.

4. Все размеры даны от стен и перегородок "в чистоте".

5. Привязки розеток, розеточных групп и электрических лючков указаны на плане от центра розетки.

6. Проводка монтируется преимущественно скрыто в перегородках, в запотолочном простанстве, в фальш-стенах.

7. Привязка розеток около дверей дается на 200мм от края дверного проема, угла если не указано иное. см. фрагмент и см. лист 12,13

8. Привязка розеток около дверей дается на 150мм от края дверного проема, угла если не указано иное. см. фрагмент

Данный лист см. с листом 1,2

М 1:100

Изм.	Кол.	Лист	№док.	Подпись	Дата
ГАП		Язмурадова			
Архитектор		Барышников			
Проверил					
Н. контр.					

Заказчик:ОАО "Сбербанк"

Проект перепланировки офисных помещений 23-ого этажа корпуса А по адресу:г. Москва, А.Вавилова,19

23-й этаж корпуса А

Стадия	Лист	Листов
И	11	

План этажа с расстановкой выключателей и групп освещения

23

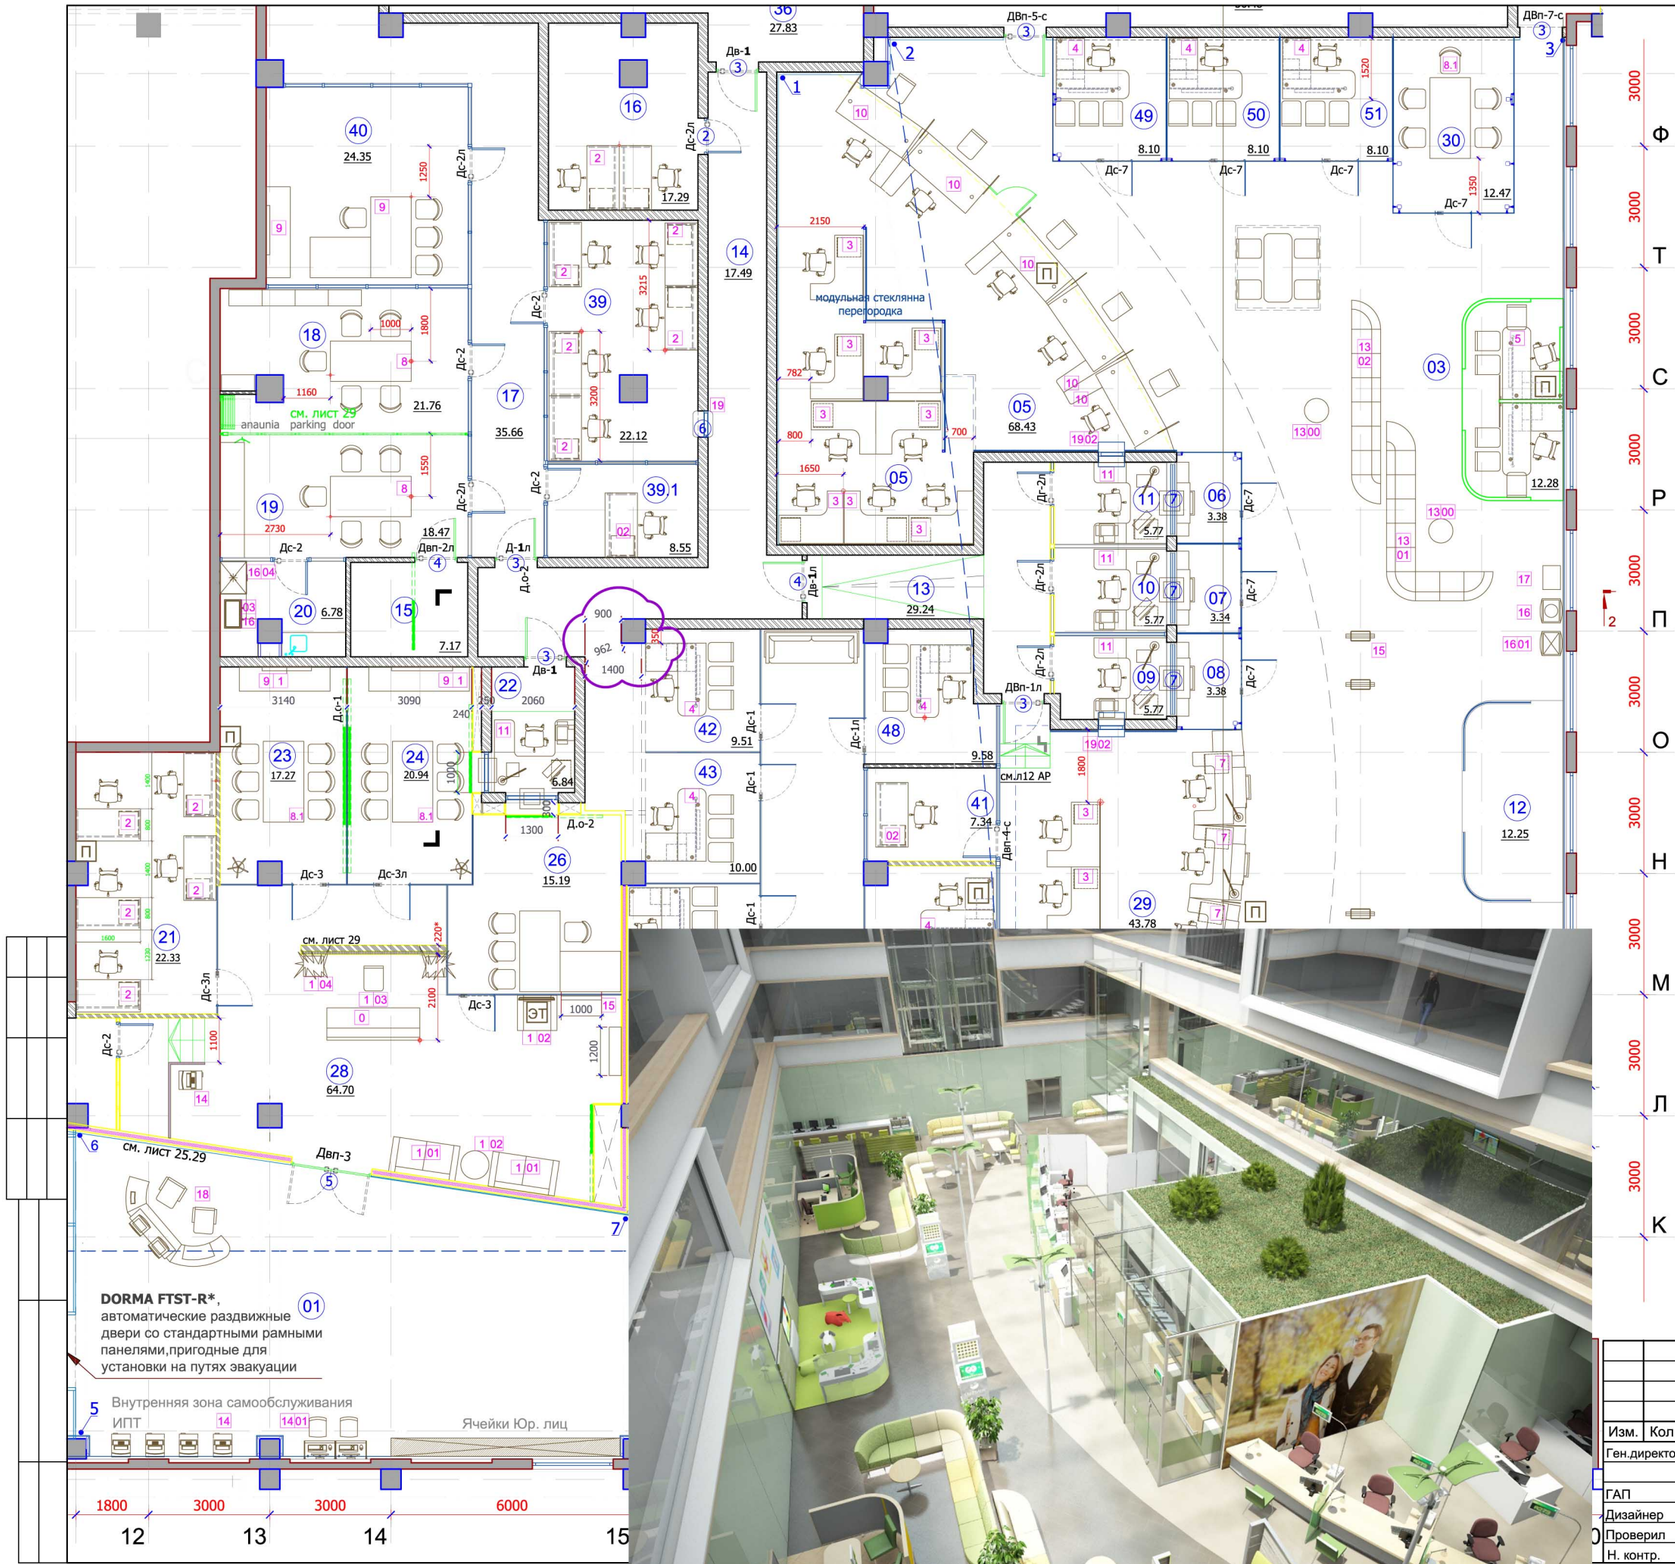

Фрагмент плана (помещение №27)

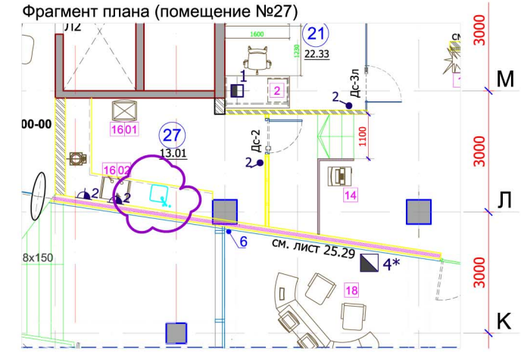

Условные обозначения

1		Монолитный железобетон
2		Бронепанели
3		Кирпичная перегородка 250мм
4		Цельностеклянная перегородка
5		Кирпичная перегородка 120мм
6		Гипсокартонная водостойкая перегородка 150 мм
7		Существующие стены
8		Мобильные перегородки
9		Разделительная перегородка с бронестеклом
10		Существующие стены(не входят в состав дизайна)
11		Контур плиты второго этажа

Условные обозначения

ЭТ	Табло электронной очереди

М 1:100

Изм.	Кол.	Лист	№док.	Подпись	Дата
Ген.директор		Маркович			
ГАП		Язмурадова			
Дизайнер		Барышников			
Проверил					
Н. контр.					

Заказчик:ОАО "Сбербанк" АИ

Залы ОПЕРУ
г. Москва ул. Большая Андроньевская, д. 8

1 этаж

Стадия	Лист	Листов
Р	12	

План расстановки мебели (1 часть)

Felix Markovich

EZED

План потолков с осветительным оборудованием/ План разводки освещения на выключатели

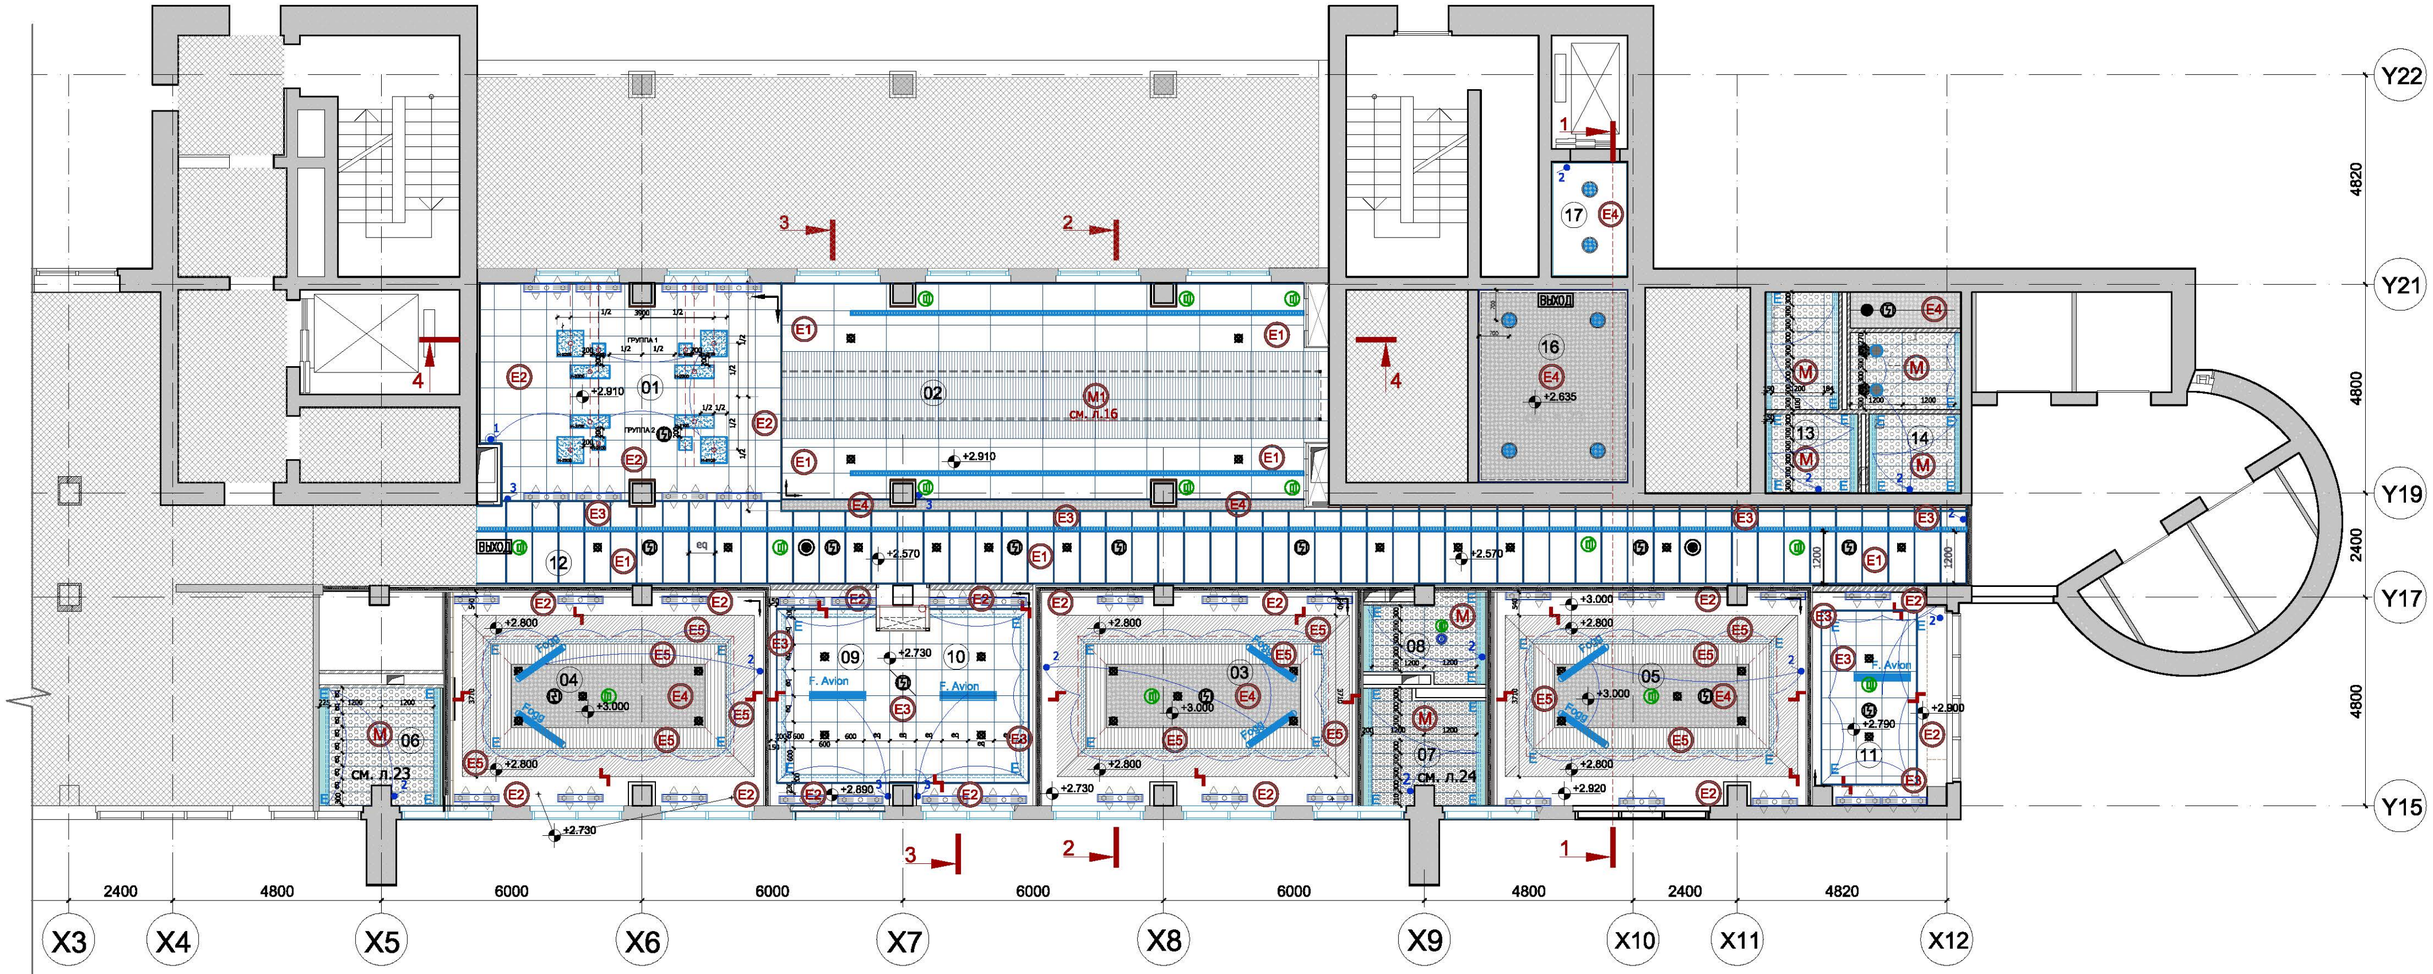

Условные обозначения материалов

Обозн.	Потолки	Площадь м2	Примечание
E1	1.Подвесной акустический потолок Ecophon Focus кромка D .,600x1200	288.0	п.69
E2	1.Подвесной акустический потолок OWA coustic premium.,скрытая система 600x1200	92.0	п.70
E3	1.Подвесной акустический потолок Ecophon Focus кромка D 600x600	79.2	п.69
	2.Ecophon Focus **Wing** FT*устанавливается **по периметру подвесных потолков** Focus кромка (приемная № 09,10,11)	4.32 17.92	п.70 п.71 см. л.13,
E5	1.Подвесной гипсовый потолок	102.5	см. л.13,14 п.76

Обозн.	Потолки	Площадь м2	Примечание
E4	1.Подвесной водостойкий гипсокартоный потолок "Knauf" 2.обработкой поверхностей потолков акриловой грунтовкой 3. с последующей окраской водоэмульсионным составом по штукатурке потолков	53.00	п.73 п.74 см.л. 14,23
M	1.Перфорированный металлический потолок АР 300x1200, цвет бело-матовый диаметр отверстий 1,5 мм.,0,7 (L*.,L*)	41.40	п.72 см.л.19,20,21
M2	1.Декоративная подвесная потолочная конструкция из нержавеющей стали.,см. л.16 (переговорная)	272 шт.	п.47 см.л. 16

Условные обозначения осветительных приборов

Позиция	Наименование	Обозначение
1	2	3
1	Скрытая подсветка	E
2	Светильник на тросовом подвесе Open Box Beta (A-1546) "Fagerhult" *	F.Open Box
3	Линейный встраиваемый светильник Notor_Delta "Fagerhult"	F.Notor_Delta
4	Линейный встраиваемый светильник XAL **	XAL L- 3000

Позиция	Наименование	Обозначение
1	2	3
4	Светильник на тросовом подвесе Avion 50 "Fagerhult"	F.Avion
5	Светильник на тросовом подвесе (по индв. дизайну) "Fogg"	
6	Светильник на тросовом подвесе (по индв. дизайну) "Fogg"	Fogg
7	Светильник встраиваемый с люминесцентными лампами "Fagerhult"	

М 1:100

Изм.	Кол.	Лист	№док.	Подпись	Дата
Ведущ.арх.					
Архитектор					
Проверил					
Н. контр.					

Заказчик:ОАО "Сбербанк"

Проект перепланировки офисных помещений 23-ого этажа корпуса А по адресу:г. Москва, А.Вавилова,19

23-й этаж корпуса А

Стадия	Лист	Листов
И	10	

План потолков с осветительным оборудованием
План разводки освещения на выключатели

Согласовано:

2-2
развертка 26,27

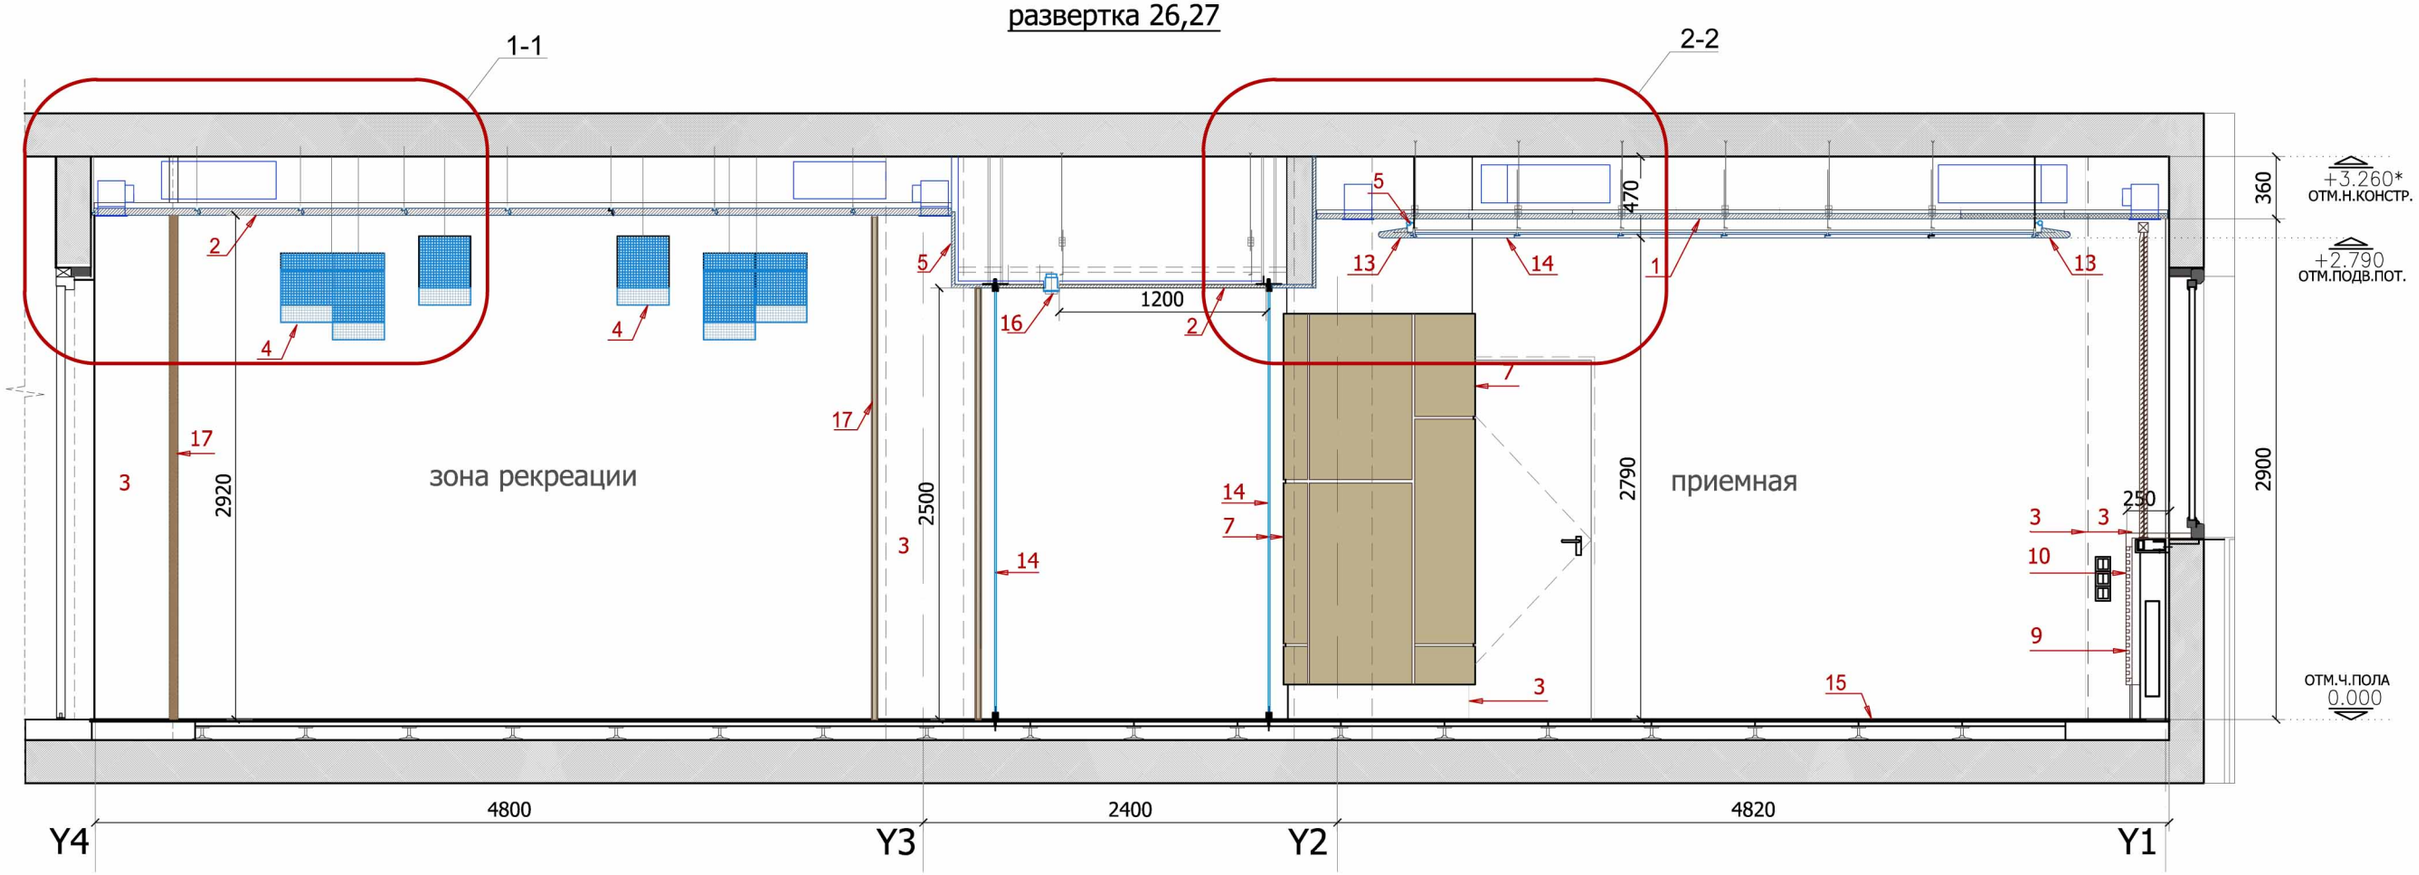

фрагмент потолка 1-1

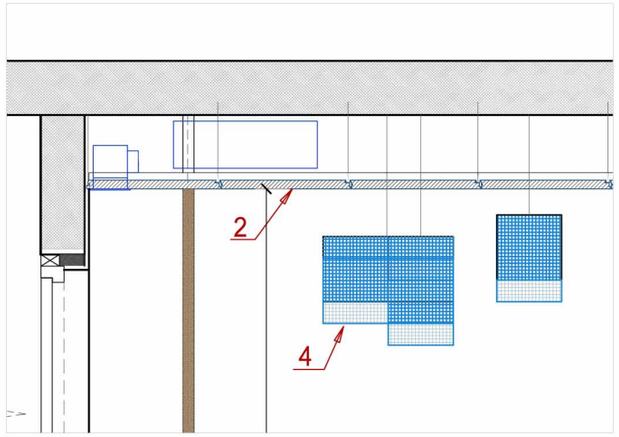

фрагмент потолка 2-2

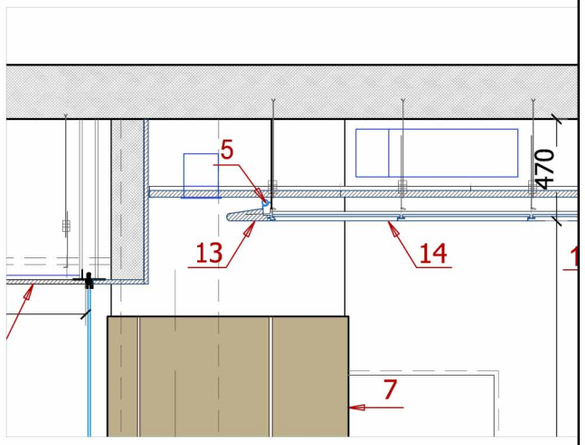

Условные обозначения материалов

1	Подвесной акустический потолок OWA coustic premium.,скрытая система 600x600
2	Подвесной акустический потолок Ecophon Flexiform
3	Стеновые панели "DuPont Corian" Artic Ice (4)
4	Светильники на тросовом подвесе Fogg
5	ГКЛ
6	Стеклянные раздвижные двери/панели
7	Трехслойная стеновая панель облицованная шпоном с светодиодовой подсветкой
8	Финишное покрытие Ковролин "Net Frise"
9	Декоративный экран для ниш отопления из шпонированных решеток
10	Подоконная доска (шпон)
11	Интегрированная скрытая подсветка Ecophon
12	Перегородка из стеклянного безопасного стекла
13	Ecophon Focus Wing
14	Панели потолочные Ecophon 600x600
15	Финишное покрытие Кварцевое напольное покрытие "DuPont /Zodiaq"Snow white
16	Профильный уголок
17	Колонна.,шпонированная панель- орех
18	Подвесной акустический потолок Ecophon Master /Combison кромка D .,600x1200

Данный лист см. с листом 1,2

Изм.	Кол.	Лист	№док.	Подпись	Дата	Заказчик:ОАО "Сбербанк"			
						Проект перепланировки офисных помещений 23-ого этажа корпуса А по адресу:г. Москва, А.Вавилова,19			
						23 этаж корпус А	Стадия	Лист	Листов
							И	14	
Вед.арх.		Язмурадова				сечение 2-2	Felix Markovich АРХИТЕКТУРНО•КОНСТРУКТОРСКОЕ БЮРО		
Архитектор		Барышников							
Проверил									
Н. контр.									

развертка 26,27 (приемная)
развертка 28,25..,24,21 (зеркально)

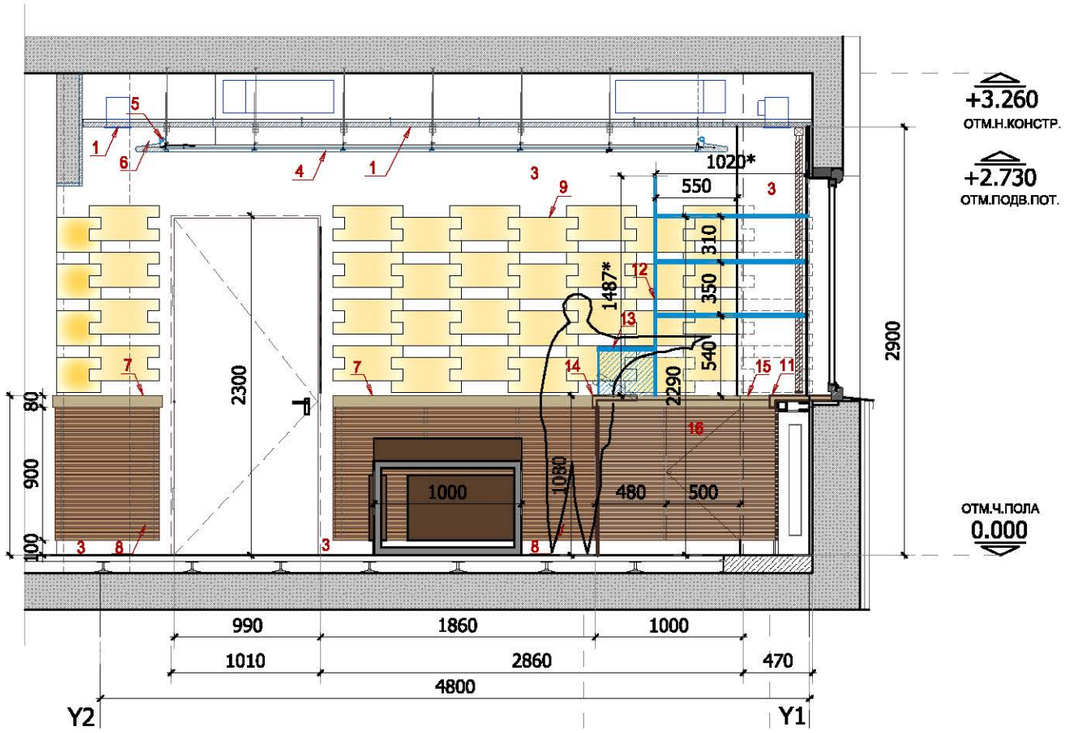

развертка 27,28 (приемная)

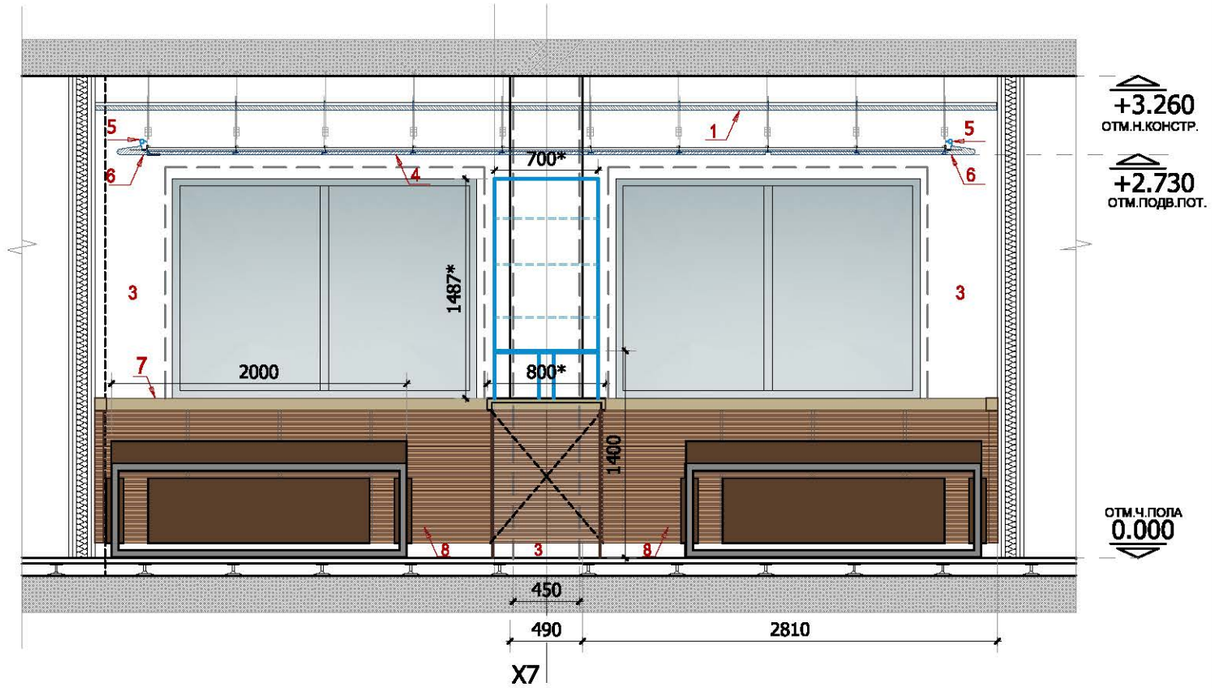

фрагмент плана

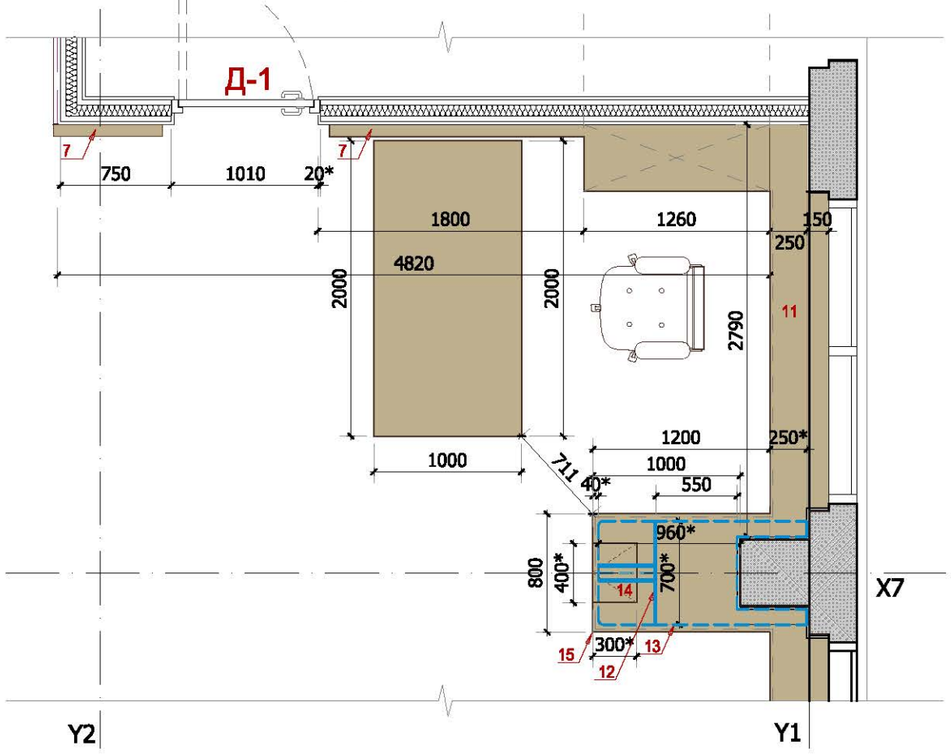

Условные обозначения материалов

1	Подвесной акустический потолок OWA coustic premium.,скрытая система 600x1200
2	Скрытая подсветка
3	Стеновые панели "DuPont Corian" Artic Ice (4)
4	Подвесной акустический потолок Ecophon Master /Combison кромка D .,600x1200
5	Интегрированная скрытая подсветка Ecophon
6	Ecophon Focus Wing
7	Верхний пояс декоративного экрана для ниш (итальянский орех)
8	Декоративный экран для ниш отопления из шпонированных решеток (темный дуб)
9	Декоративная настенная панель с элементами освещения
10	Дверца встроенной мебели (Декоративный экран из шпонированных решеток)
11	Подоконная доска (шпон)
12	Стойки из безопасного стекла(стекло матовое)
13	Полка из безопасного стекла (стекло матовое)
14	Откидная полка встроенного шк. для шредера
15	Верхняя полка встроенной мебели (итальянский орех)
16	Дверца встроенной мебели (Декоративный экран из шпонированных решеток)

Изм.	Кол.	Лист	№док.	Подпись	Дата				
						Заказчик:ОАО "Сбербанк"			
						Проект перепланировки офисных помещений 23-ого этажа корпуса А по адресу:г. Москва, А.Вавилова,19			
						Приемная помещения №9,10	Стадия	Лист	Листов
							И	17	
Вед.арх.						развертки фрагмент плана			
Архитектор									
Проверил									
Н. контр.									

Вид С

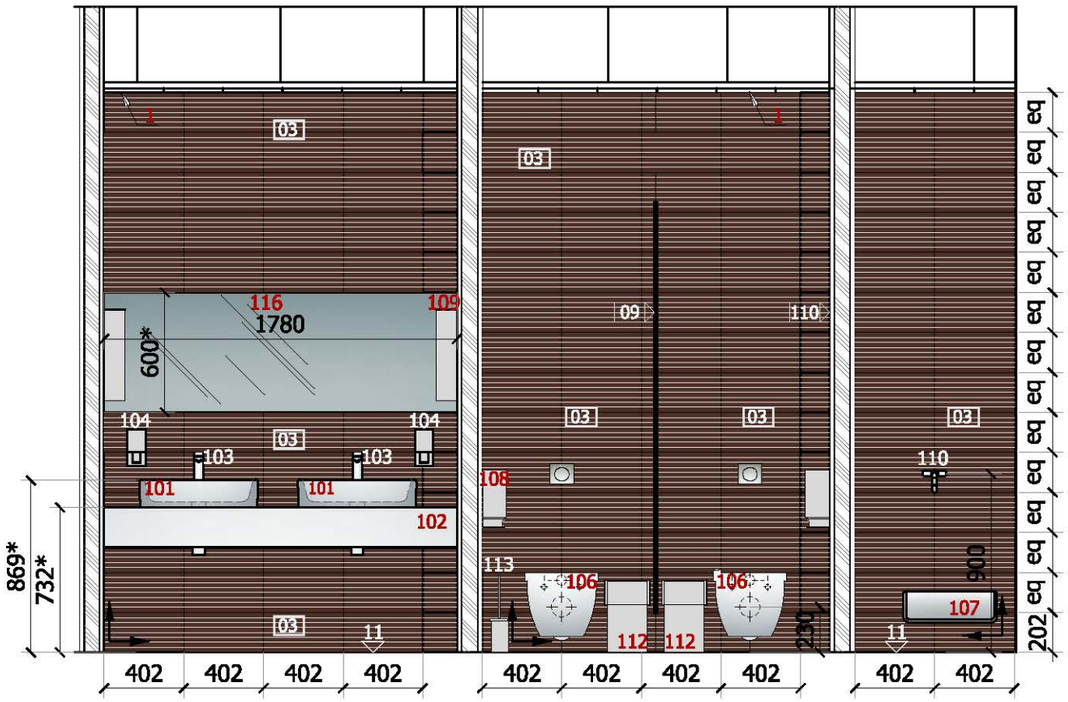

Вид В

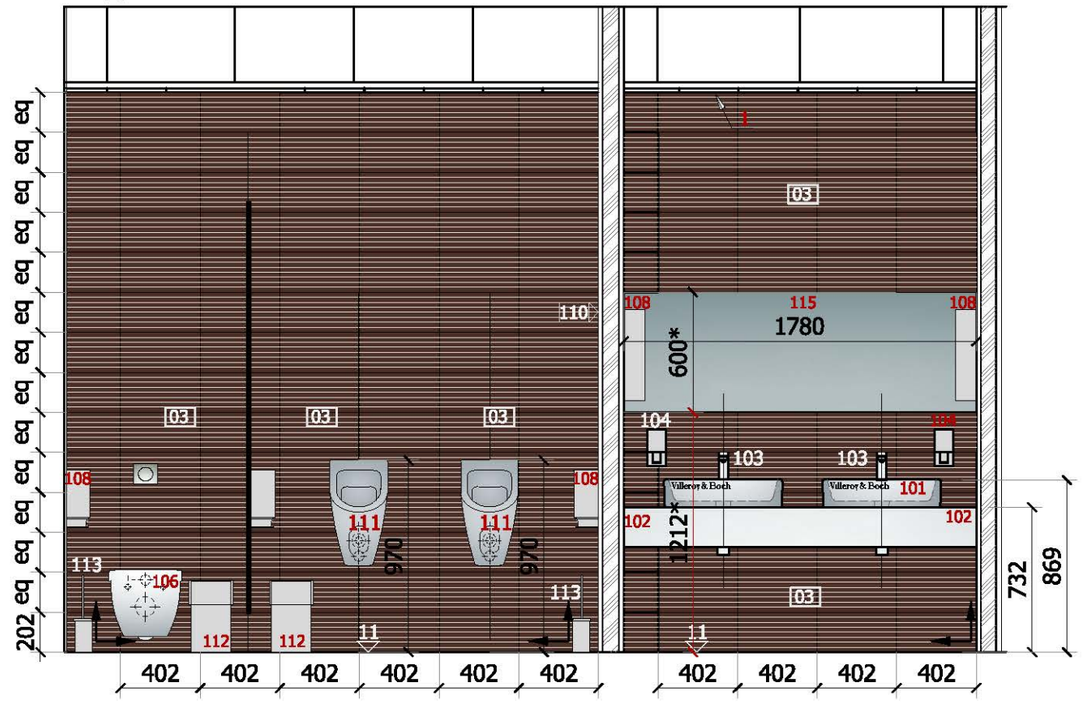

фрагмент плана

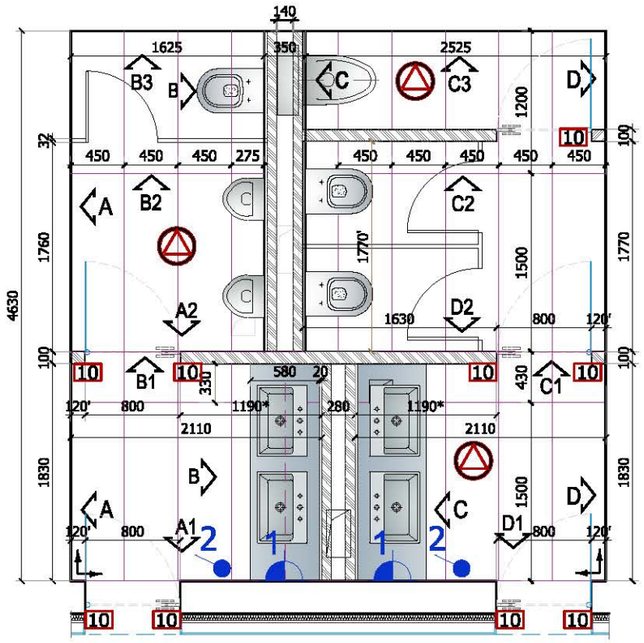

фрагмент потолка

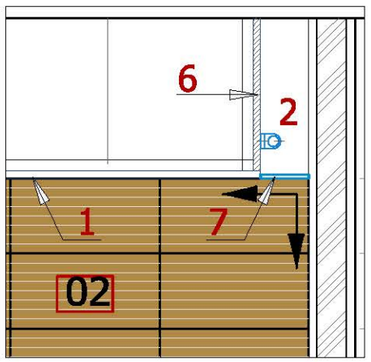

Общие указания

1.Общие указания смотри АИ лист 1.
2.Данный лист смотри с ведомостью материалов
3.Данный лист смотри с листом **
5.Расскладка плитки выполненна с учетом швов
6.Ширину швов между плитками выполнить2мм.
7.Каждая кабинка с/у должна содержать полный набор аксессуаров : бумагодержатель , мусорную карзину ,держатель запасных рулонов туалетной бумаги , ершик , держатель освежителя воздуха в зоне раковин необходимы : контейнер для жидкого мыла , контейнер для бумажных полотенец , мусорная корзина , электрическая сушка для рук . Размеры зеркал, столешниц и типы крепежей уточнить по месту перед заказом.
8.Отверстия в столешнице под раковины выполняются по установочным размерам производителя.
9.Зеркало - встроенное, "заподлицо" с керамической плиткой, за зеркалом плитку не класть, образец зеркала согласовать.
10.Затирка влагостойкая подбирается под горизонт. членений плитки и согласовывается.

Согласовано:

Изм.	Кол.	Лист	№док.	Подпись	Дата	Заказчик:ОАО "Сбербанк"		
						Проект перепланировки офисных помещений 23-ого этажа корпуса А по адресу:г. Москва, А.Вавилова,19		
						Санитарный узел Помещение №13,14	Стадия	Лист	Листов
							И	20	
Вед.арх.		Язмурадова							
Архитектор		Барышников				развертки фрагмент схемы плана	Felix Markovich АРХИТЕКТУРНО-КОНСТРУКТОРСКОЕ БЮРО	
Проверил								
Н. контр.								

1-1

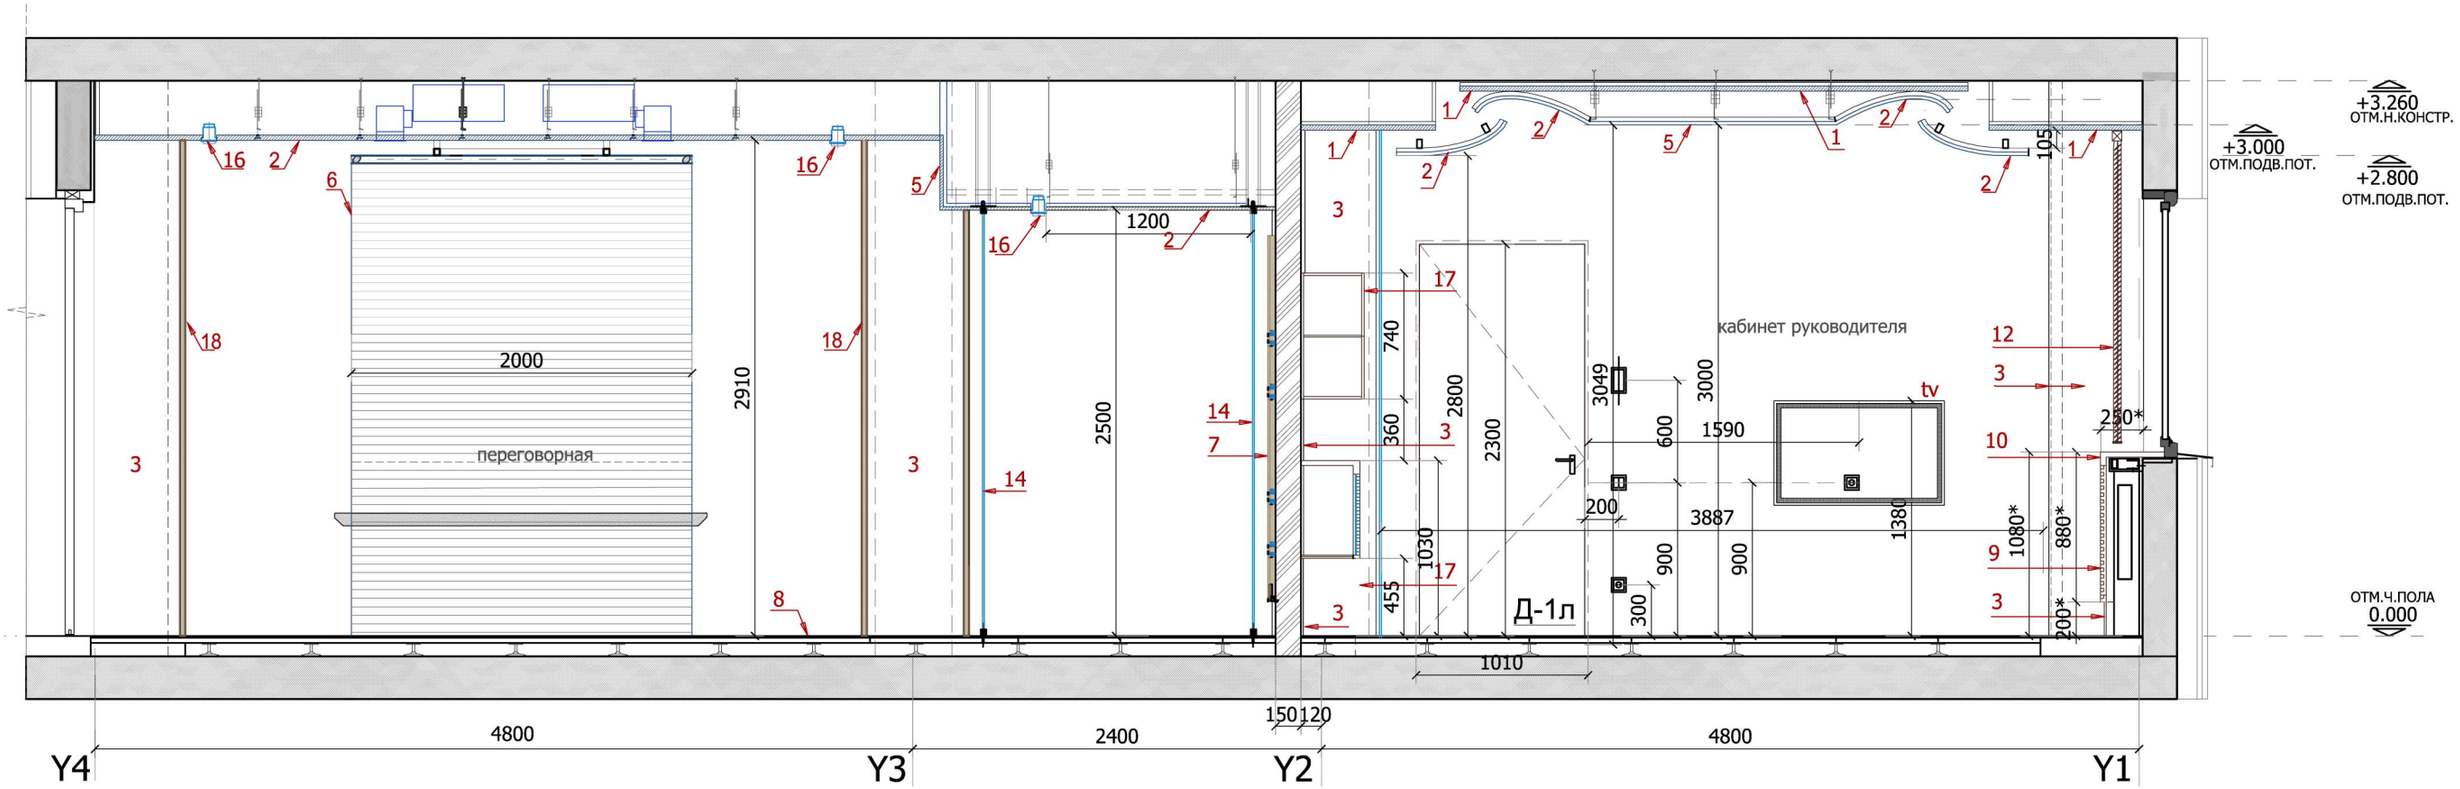

Условные обозначения материалов

1	Подвесной акустический потолок OWA coustic premium.,скрытая система 600x1200
2	Декоративный подвесной элемент потолка (легкий гипс)
3	Стеновые панели "DuPont Corian" Artic Ice (4)
4	Подвесной акустический потолок Ecophon Flexiform
5	ГКЛ
6	Декоративный подвесной потолочный элемент (металл)
7	Стеновая панель облицованная шпоном с светодиодовой подсветкой
8	Финишное покрытие Ковролин "Limited Edition"
9	Декоративный экран для ниш отопления из шпонированных решеток
10	Подоконная доска (шпон)
11	Декоративная панель колонны из закаленного стекла (или триплекс)
12	Горизонтальные жалюзи
13	Автоматическая система раздвижных стен
14	Перегородка из стеклянного безопасного стекла
15	Карнизный светильник
16	Линейный встраиваемый светильник Notor_Delta "Fagerhult" *
17	Навесные шкафы
18	Колонна.,шпонированная панель

Изм.	Кол.	Лист	№док.	Подпись	Дата	Заказчик:ОАО "Сбербанк"			
						Проект перепланировки офисных помещений 23-ого этажа корпуса А по адресу:г. Москва, А.Вавилова,19			
						23 этаж корпус А	Стадия	Лист	Листов
							И	13	
Вед.арх.									
Архитектор						сечение 1-1			
Проверил									
Н. контр.									

Вид 2С

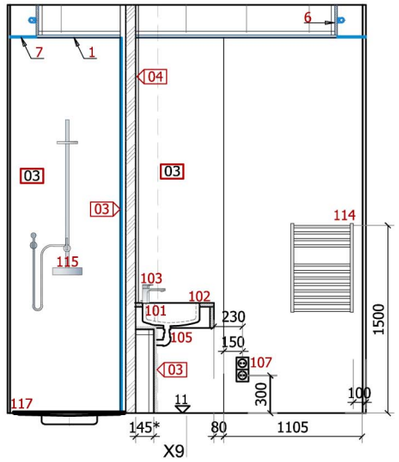

Вид Е

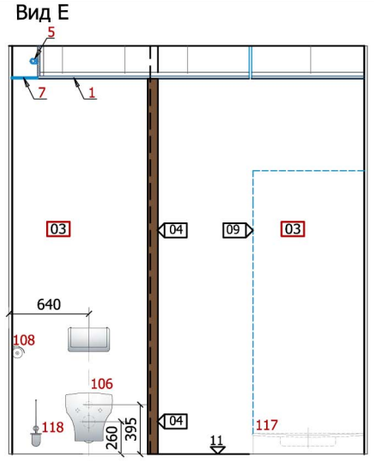

Вид 1С

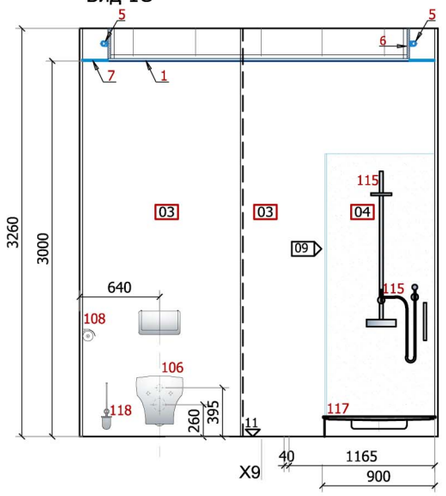

Вид В

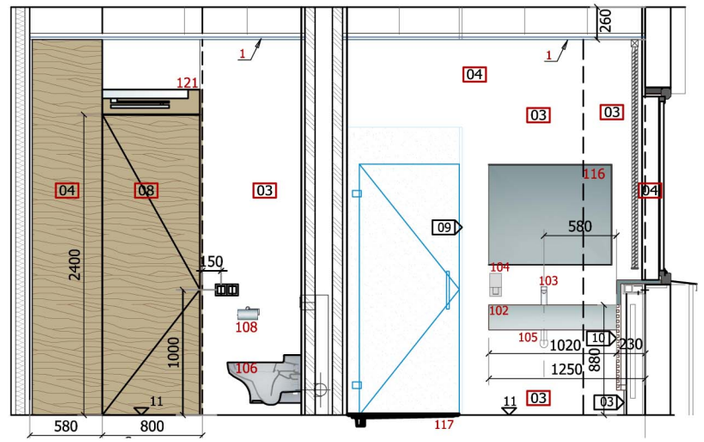

Вид А

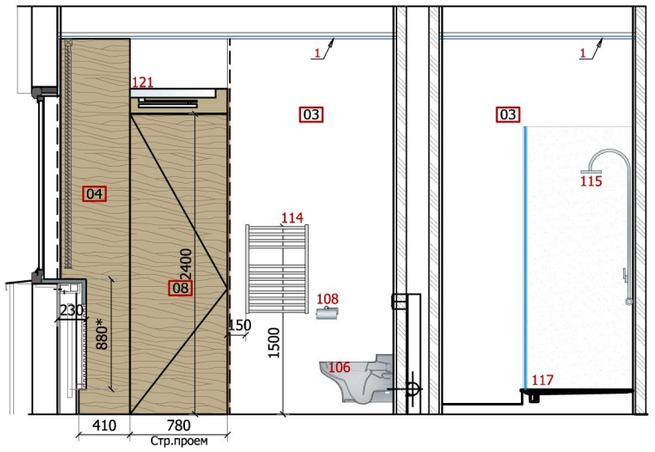

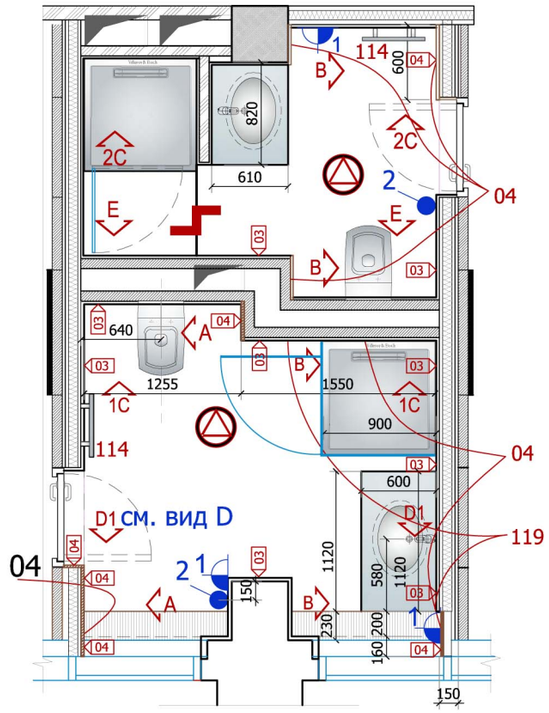

Условные обозначения материалов

№	Наименование	Площадь,м2 кол-во.	Примечание
1	Перфорированный металлический потолок OWAtecta Perfora, кассеты с зажимами	см. л.10	п.72
2	Подоконная доска (шпон итальянский орех)	см. л.8/8.1	
3	Стеновые панели "DuPont Corian" Artic Ice (4)	см. л.8/8.1	п.60.61
4	Водостойкие шпонированные панели, беленый дуб	14.89	п.56/57
5	Встроенная люминистцентная подсветка	см раздел ЭОМ	
6	Гипсокартоная боковая панель		
7	Съемное матовое стекло		
8	Дверной блок в проеме гипсокартонной стены с облицовкой шпонированными стеновыми панелями	см. л.4,5,6	
9	Стеклянная перегородка душевой кабины	см. л.4,5,6	
10	Декоративный экран для ниш отопления из шпонированных решеток (темный дуб)	см. л.4,5,6	п.152/153
11	Кварцевое напольное покрытие "DuPont /Zodiaq" Snow white	см. л.9	

Условные обозначения оборудования

№	Позиция	Наименование	Примечание
1	2	3	4
1	101	Раковина встроенная под столешницу "Villeroy Boch" LOOP & FRIENDS	Аксессуары - шлифованная нержавеющая сталь
2	102	Столешница из кориана, перед заказом уточнить размер по месту.	
3	103	Смеситель однорычажный для раковины "Villeroy Boch" Cult	Изменения согласовать с автором проекта
4	104	Дозатор Жидкого Мыла	3шт.
5	105	Видимый сифон из хромированной стали	3шт.
6	106	Унитаз навесной со встроенным бачком "Villeroy Boch"Bellevue кнопка смыва-матовый хром	3шт.
7	107	Блок розеток	см. л.11
8	108	Держатель рулонов туалетной бумаги	3шт.
9	109	Электрическая сушка для рук.	3шт.
10	110	Смеситель Для Приборaслива Из Уборочных Машин	3шт.
11	111	Держатель рулонов туалетной бумаги	3шт.
12	112	Мусорная корзина	3шт.
13	113	Электрическая сушка для рук.	*шт.
14	114	Полотенцесушитель	3шт.
15	115	Термостат для душа со стационарной стойкой и душевым гарнитуром настенного крепления, "Villeroy Boch" CIRCLE или аналог	3шт.
16	116	Зеркало встраиваемое	3шт. п.152/153
17	117	Душевой падон "Villeroy Boch" Squaro 900x900	3шт.
18	118	Ершик настенный	3шт.
19	119	Линейный встроенный настенный светильник Inter-Lux	3шт.
20	120	Горизонтальные жалюзи	3шт.
21	121	Автоматический дверной оператор распашной двери см. л.4,5,6	3шт.

Согласовано:

Изм.	Кол.	Лист	№док.	Подпись	Дата
Вед.арх.		Язмурадова			
Архитектор		Барышников			
Проверил					
Н. контр.					

Заказчик:ОАО "Сбербанк"

Проект перепланировки офисных помещений 23-ого этажа корпуса А по адресу:г. Москва, А.Вавилова,19

Санитарный узел
Помещение №7,8

Стадия	Лист	Листов
И	22	

развертки
Фрагмент плана

Felix Markovich
АРХИТЕКТУРНО•КОНСТРУКТОРСКОЕ БЮРО

Фрагмент развертки

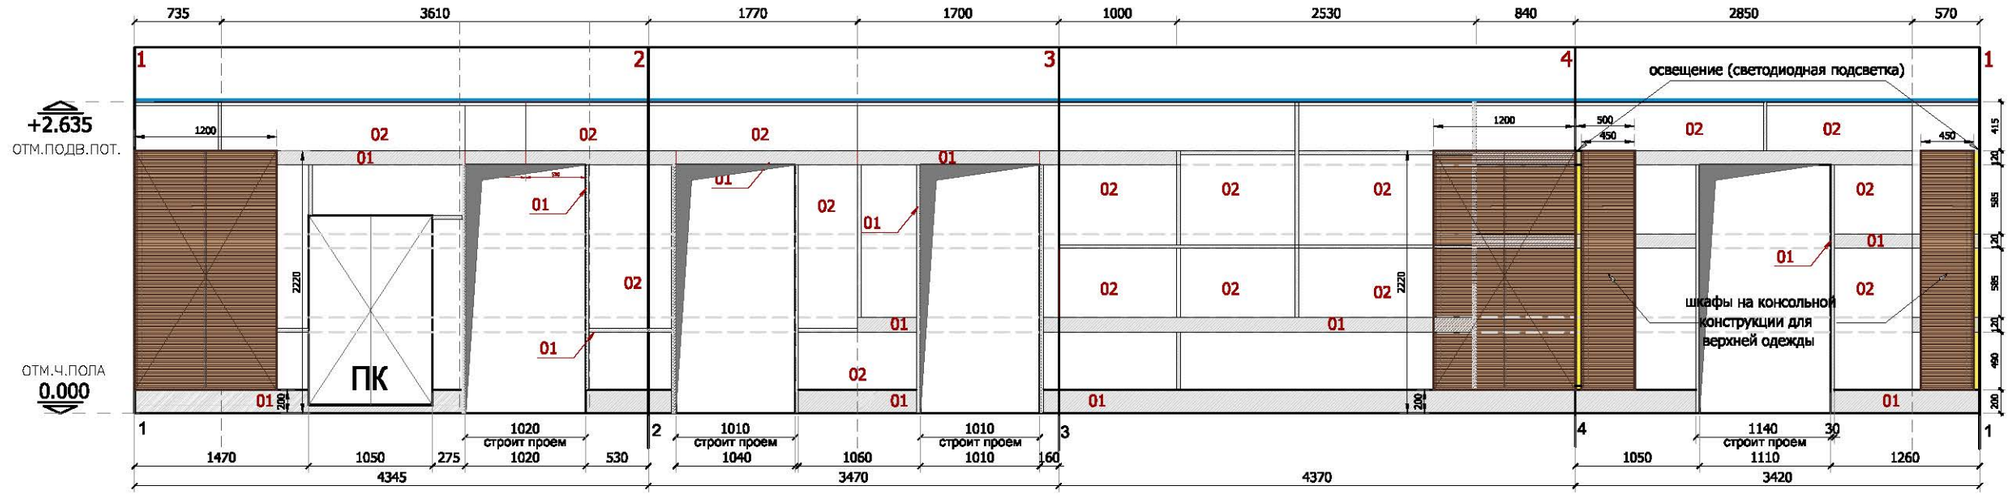

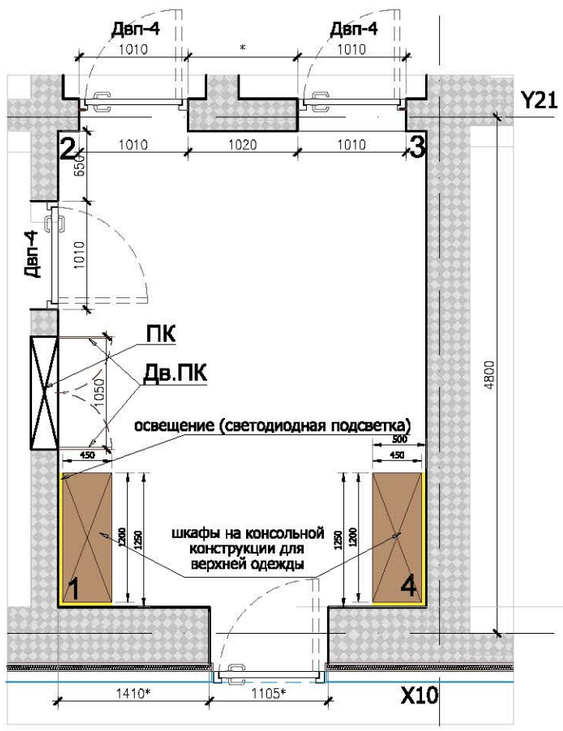

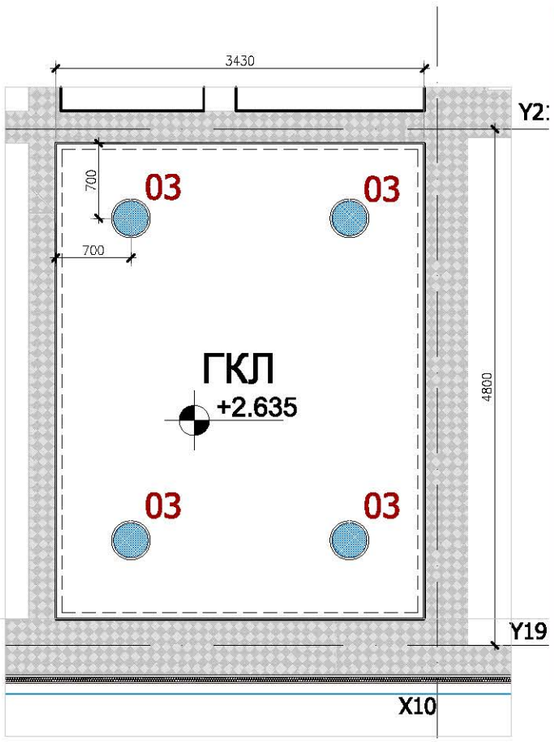

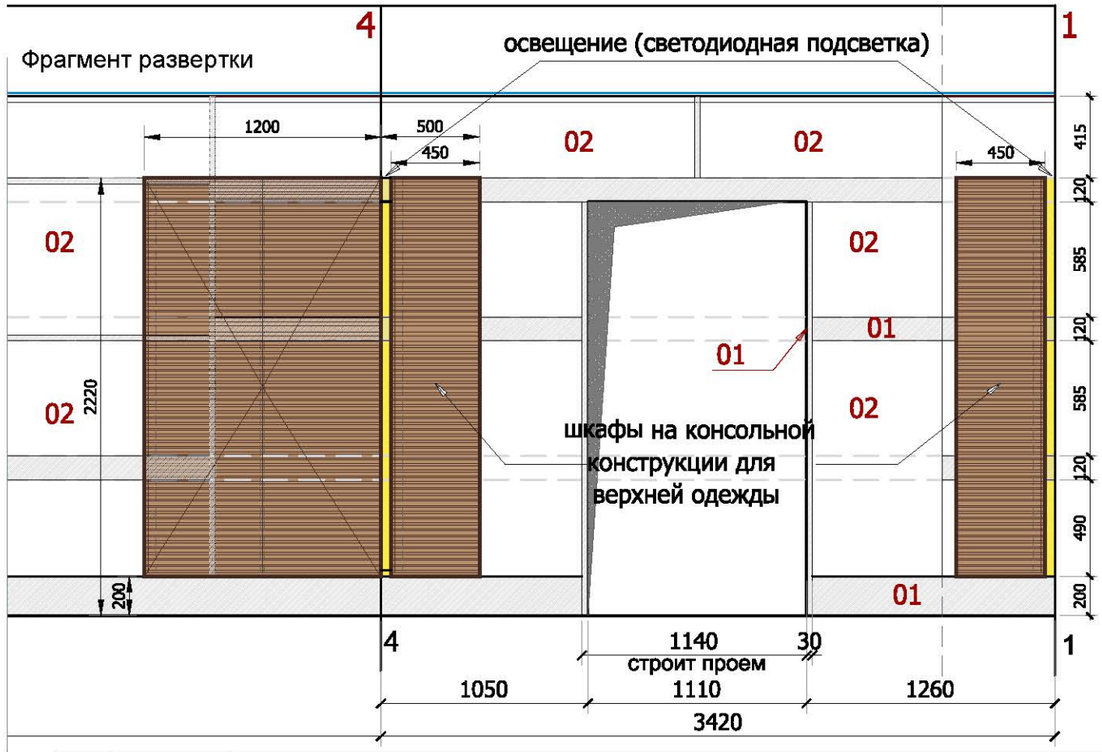

Данный лист см. с л. 23

Изм.	Кол.	Лист	№док.	Подпись	Дата	Заказчик:ОАО "Сбербанк"		М 1:50
						Проект перепланировки офисных помещений 23-ого этажа корпуса А по адресу:г. Москва, А.Вавилова,19		
						Лифтовый холл (№15)	Стадия: И	Лист: 23.1 / Листов:
Вед.арх.								
Архитектор						Фрагмент разверток		
Проверил								
Н. контр.								

План потолков
Схема расположения потолочных лючков

Потолки

	Наименование	S м2
R	Подвесной акустический перфорированный потолок Knauf_ Cleaneo Akustik	316.98
E	1.Подвесной акустический потолок Ecophon Focus ,скрытая система 600x1200	109.34
L	Подвесной потолок покрытие под дерево "Ровингер "	145.00
Г	Подвесной водостойкий гипсокартоный потолок "Knauf"	120.00
K	1.Карнизный элемент из легкого гипса	L= 434.0 М
M	1.Реечный металлический потолок	35.55
M1	1.Реечный металлический потолок	8.66
C	Светящийся потолок (капитель) см л. 31-33 панели из матового стекла.,светильники располагаются под подвесным потолком	

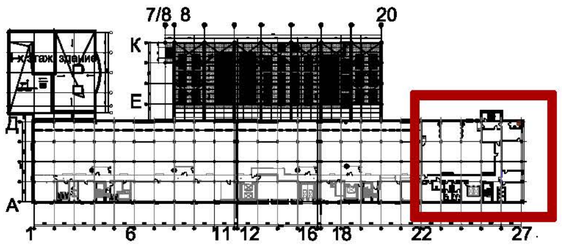

Данный лист см. л.50

ЭКСПЛИКАЦИЯ ПОМЕЩЕНИЙ ФРАГМЕНТА 5 ЭТАЖА

Номер помещ.	Наименование	Площадь, м 2
27	Кухня	29.71
28	Тамбур	8.91
29	С/у мужской	8.39
30	Операторский зал	215.15
31	Переговорная операторский зал	74.48
32	Тамбур	6.93
33	С/у женский	7.11
34	Коридор	71.50
35	Кабинет директора ЦОД	31.33
36	Комната секретаря	15.99
37	Кабинет руководителя	53.49
38	Комната отдыха	12.67
39	С/У	3.87
40	С/У	4.81
41	Техническое помещение	22.42
43	Тамбур	12.25
44	Приемная / комната для сопровождающих	33.90
45	Техническое коридор	5.53
47	С/узел для инвалидов	4.21
	Общая площадь	622.65

Условные обозначения

1		Стена из ячеистых блоков
2		Монолитный железобетон
3		Гипсокартонная водостойкая перегородка 150 мм
4		Кирпичная кладка
5		Гипсокартонная перегородка переменной высоты

Условные обозначения потолочных лючков

1		400x400	Крок
2		600x400	Хай Тек
3		400x400	Вентиляция и кондиционирование
4		600x400	Астафос
5			Проектор
6	2400 / 1200		П12 Потолки Knauf cleaneo Akustik Блочная перфорация В6

Изм.	Кол.	Лист	№док.	Подпись	Дата
ГАП		Язмурадова			
Архитектор		Барышников			
Проверил					
Н. контр.					

Заказчик:ОАО "Сбербанк"

Комплекс инженерно-технических систем Мегавычислительного центра ОАО "Сбербанк России" по адресу: Москва, 2-й Южнопортовый проезд, 12А, корпус 1, стр.2

ситуационный центр Единого центра обработки данных (МегаЦОД)"

Стадия	Лист	Листов
И	16	

План потолков
Схема расположения потолочных лючков

Felix Markovich
АРХИТЕКТУРНО-КОНСТРУКТОРСКОЕ БЮРО