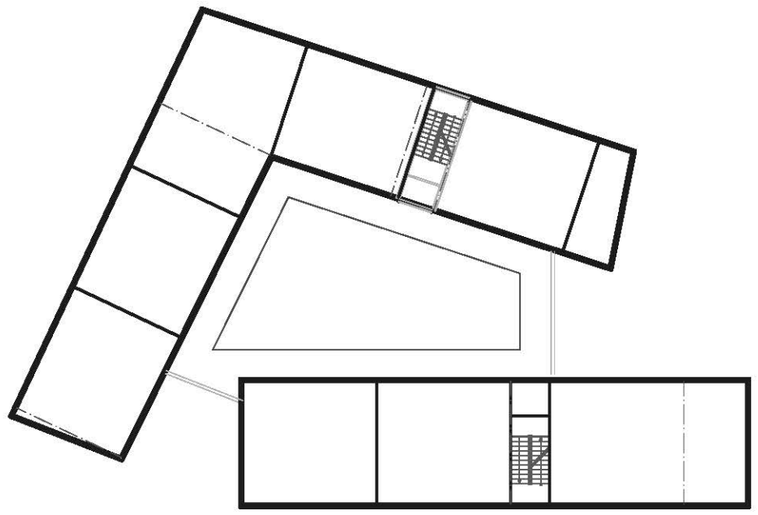

Площадь земельного участка 1280м2
Жилая площадь 640м2
Периметр 280м

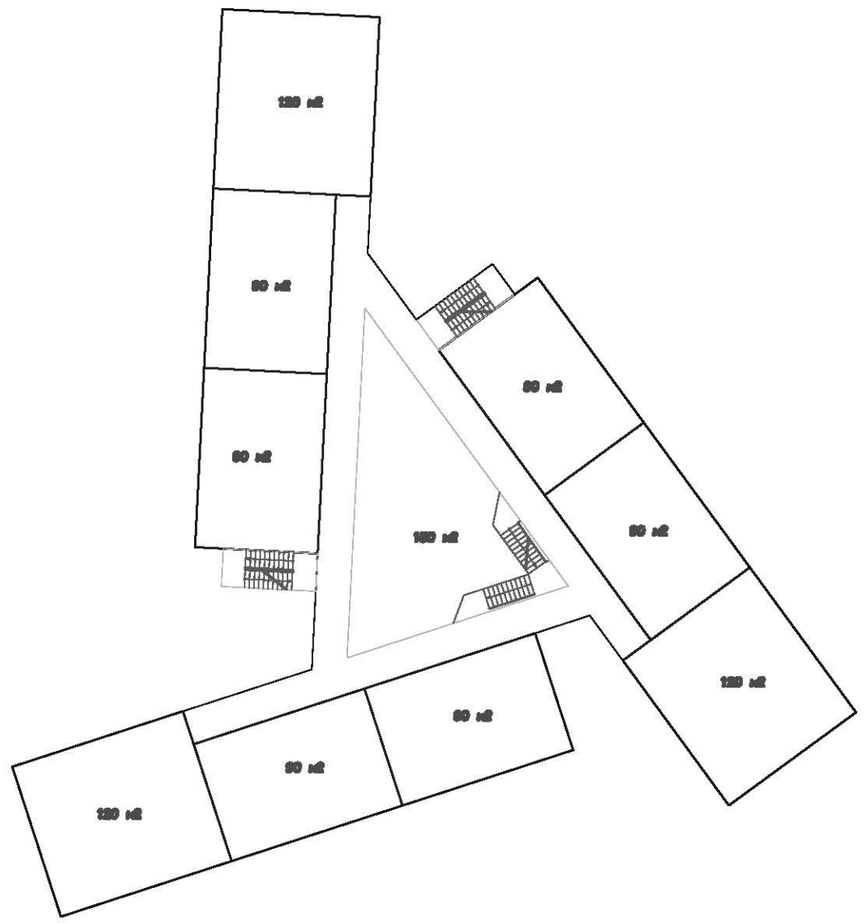

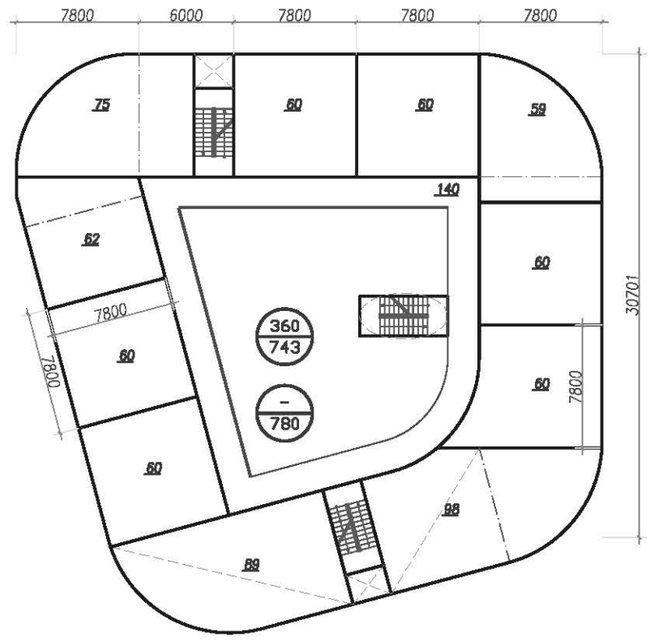

Площадь земельного участка 1280м2
Жилая площадь 640м2
Периметр 240м

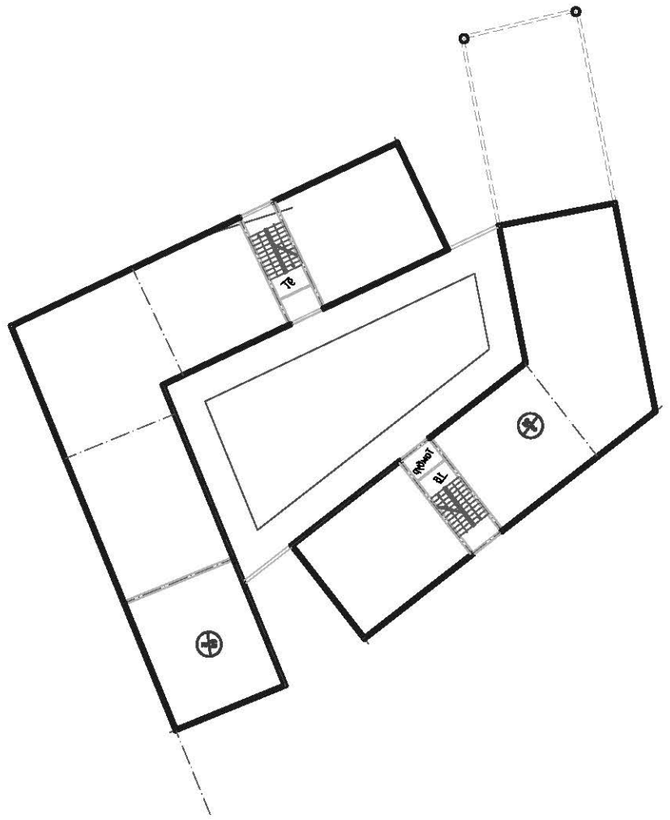

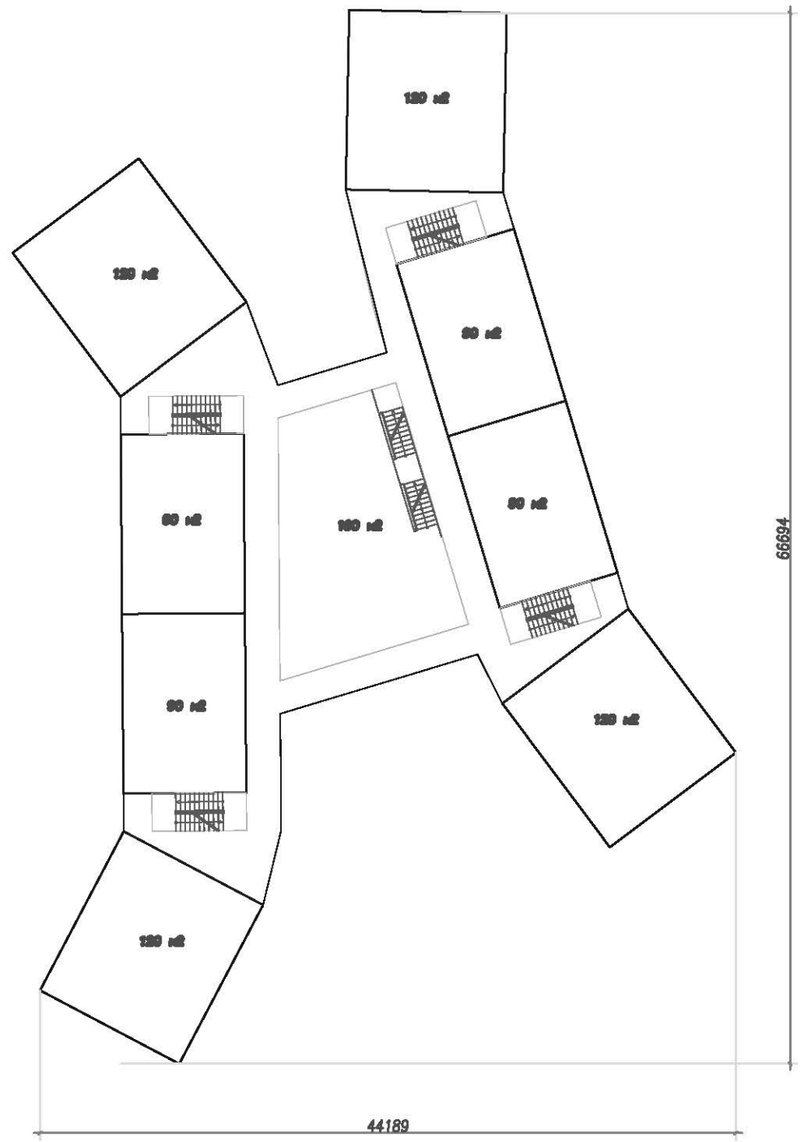

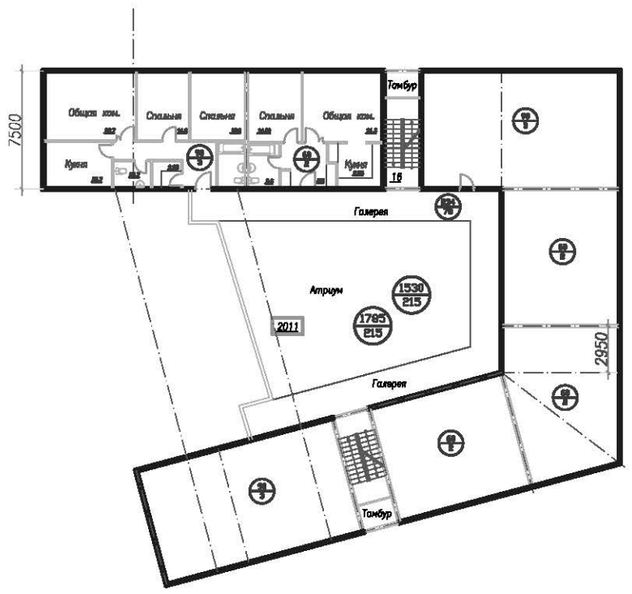

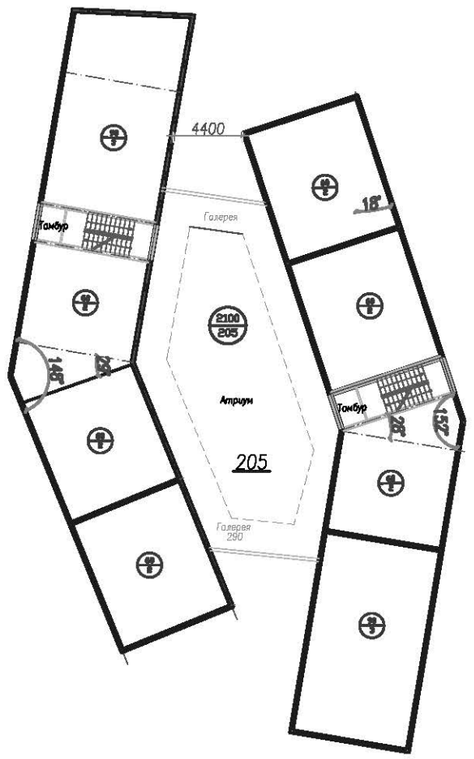

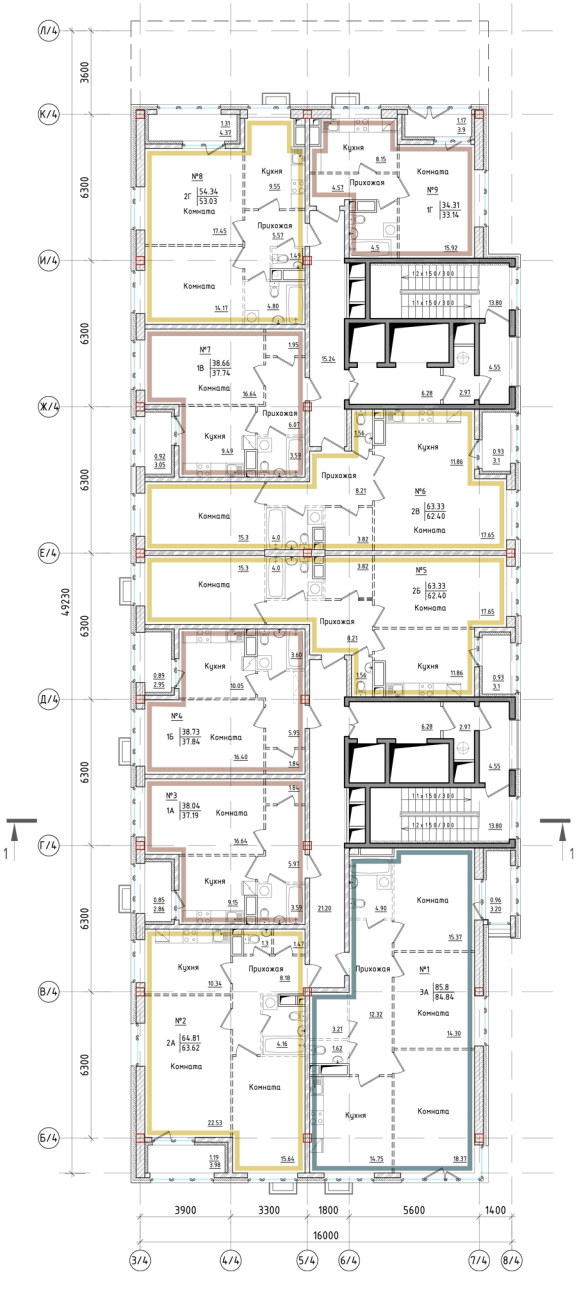

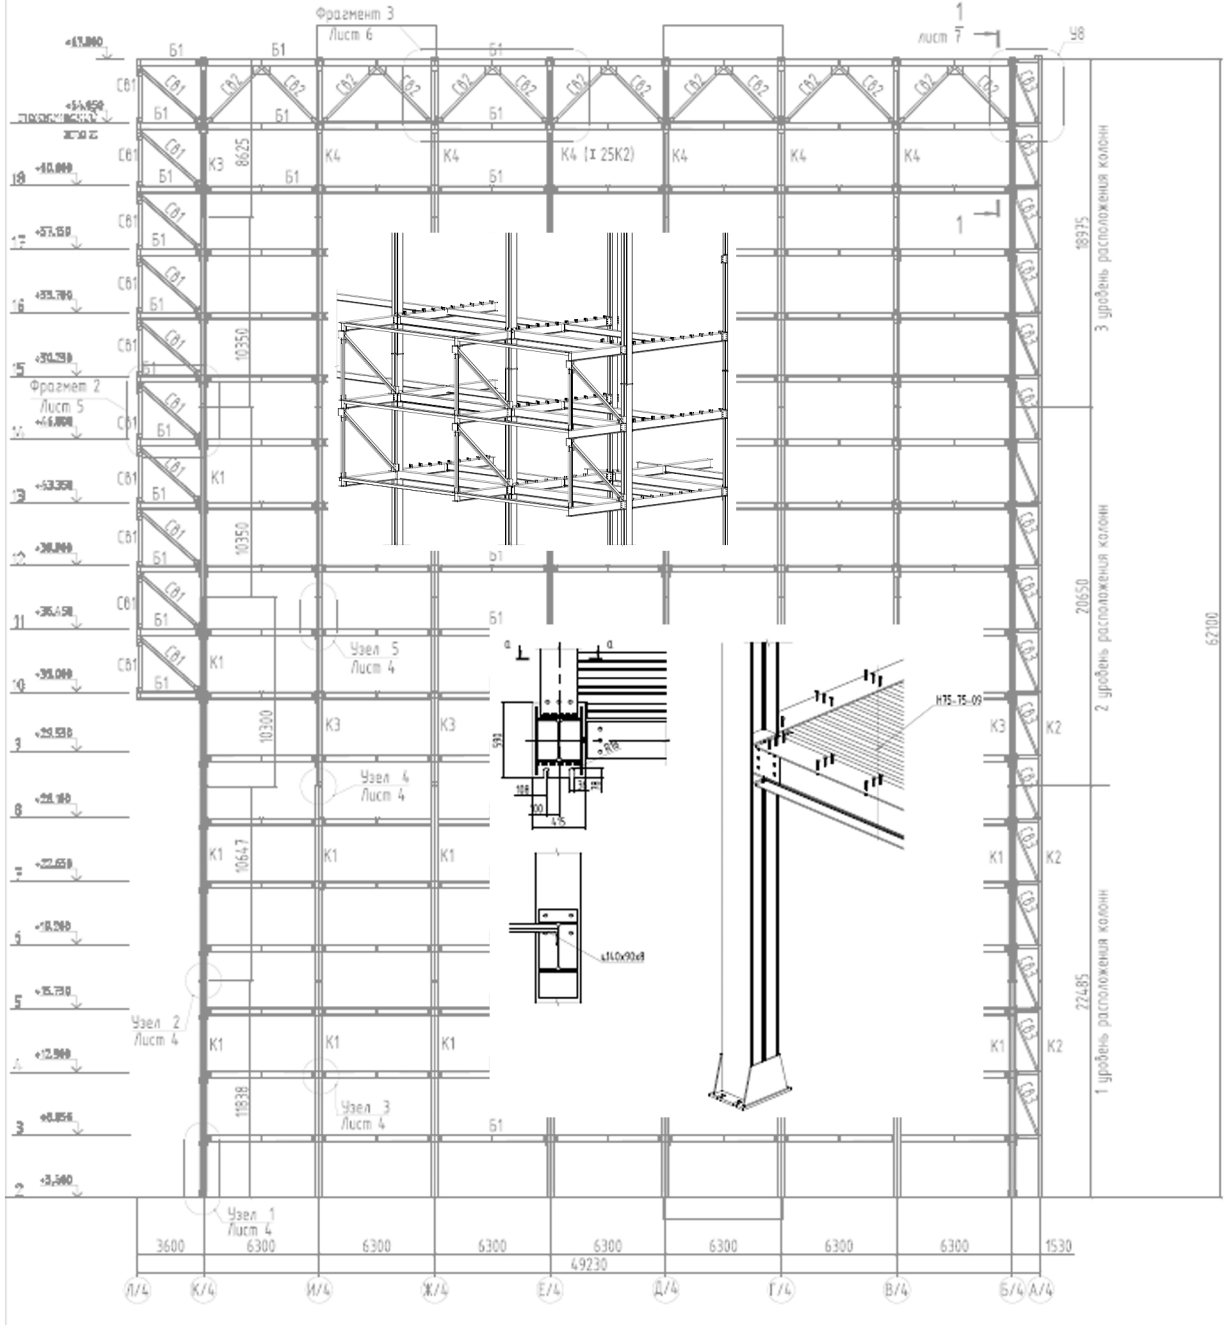

Адаптация монолитных конструкций жилого дома под стальные
Autocad. Scad. Revit

3 вариант

1. корректировка внутр. планировок квартир
2. коррект. наружного контура под **констр.***
с сохранением стилистики здания.
3. сокращение кол-ва отверстий ОВ-ВК однокомнатных квартир
4. корректировка отверстий ОВ-ВК квартир
5. увеличение ширины корпуса на *300* мм
6. изменения длины корпуса, уменьшение на *300* мм

К4 /план 3-9-го этажа

S=554.83
S=569.58

К4 план 10-18 этажа

S=614.96
S=569.58

Фасад А-А

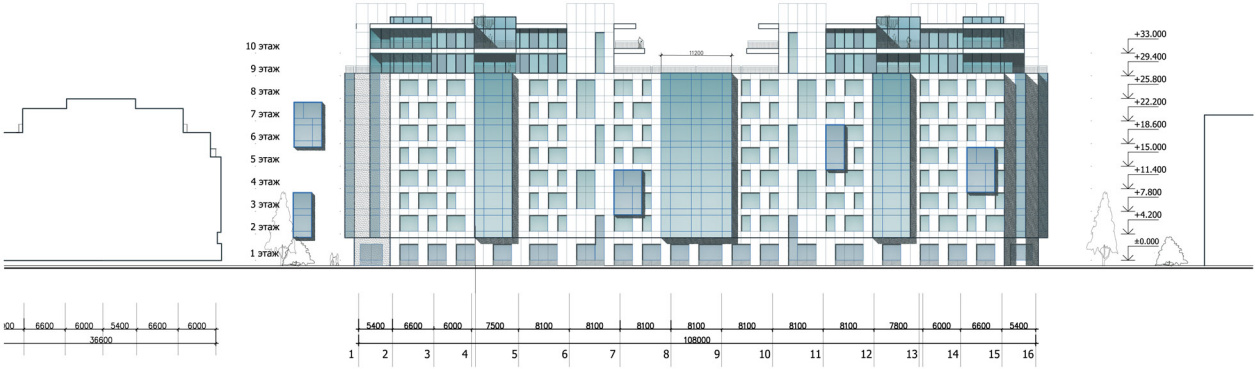

Фасад Б-Б

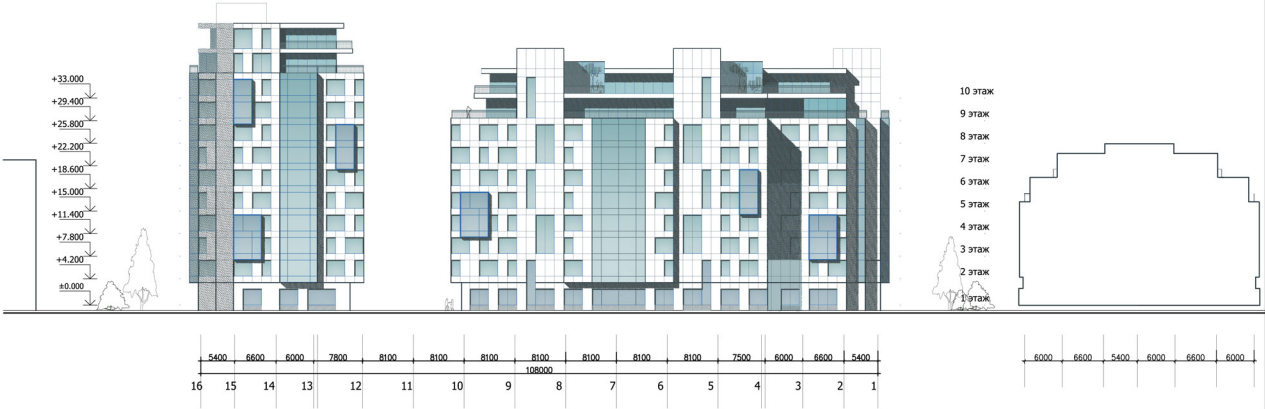

ММА + Фицрой Робинсон Интернэшнел 1-я Брестская ул. 13/14 оф.406 125190 Москва	Москва, ЦАО, ул. Большая Татарская, влад.13	Фасад А-А, Б-Б	2 вариант	

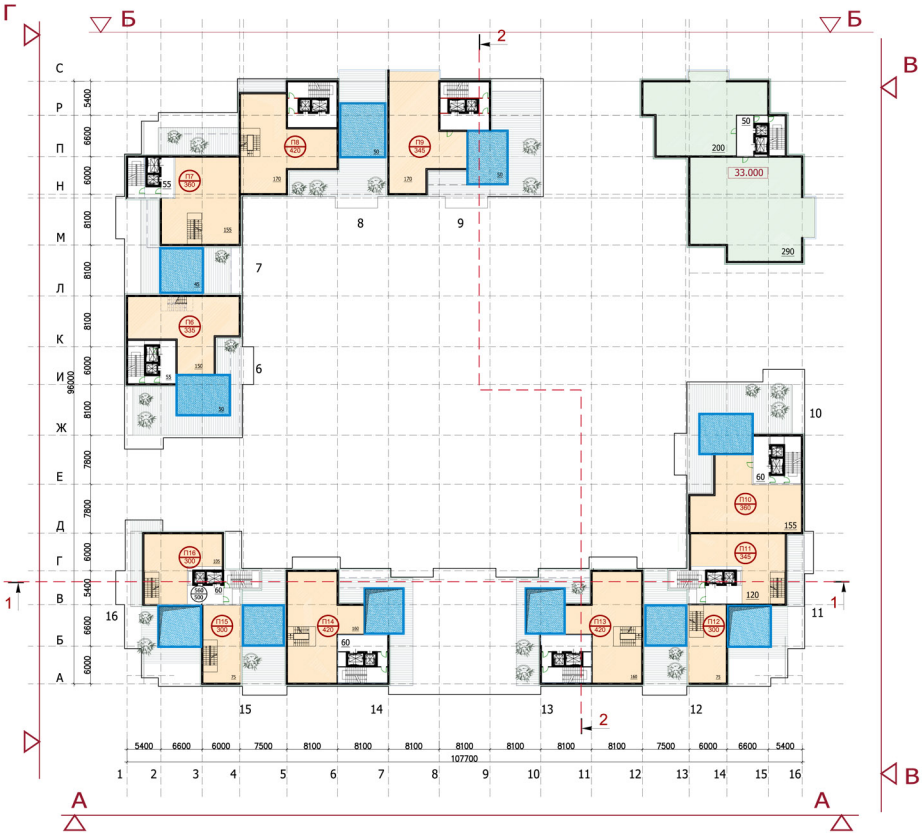

УСЛОВНЫЕ ОБОЗНАЧЕНИЯ

- Входные группы
- Пятикомнатные квартиры
- Двухуровневый пентхаус
- Зимний сад
- Эксплуатируемая кровля

ММА + Фицрой Робинсон Интернэшнел 1-я Брестская ул. 13/14 оф.406 125190 Москва	Москва, ЦАО, ул. Большая Татарская, влад.13	План этажа на отм. +33.000, +33.650	

Ритейл-парк
адресу: Московская область г. Жуковский, ул. Гудкова
Перспективные виды., Схема зонирования

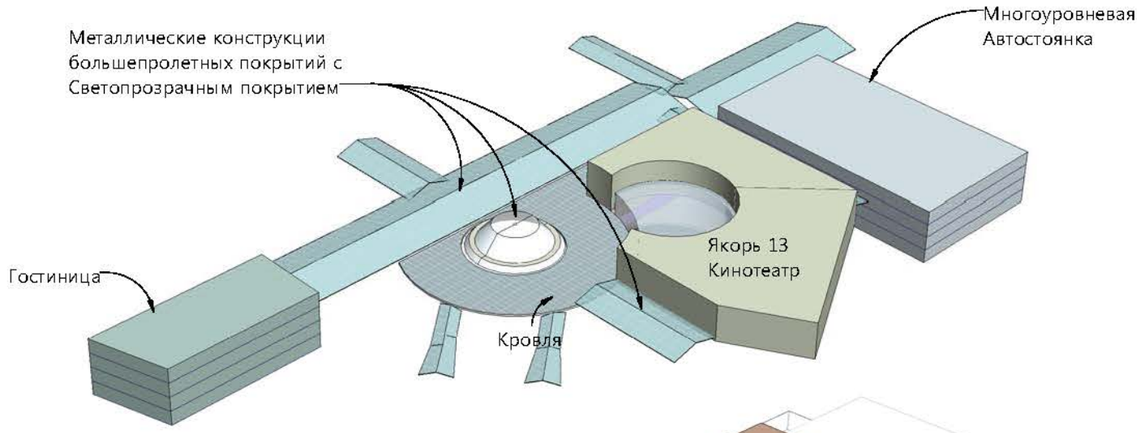

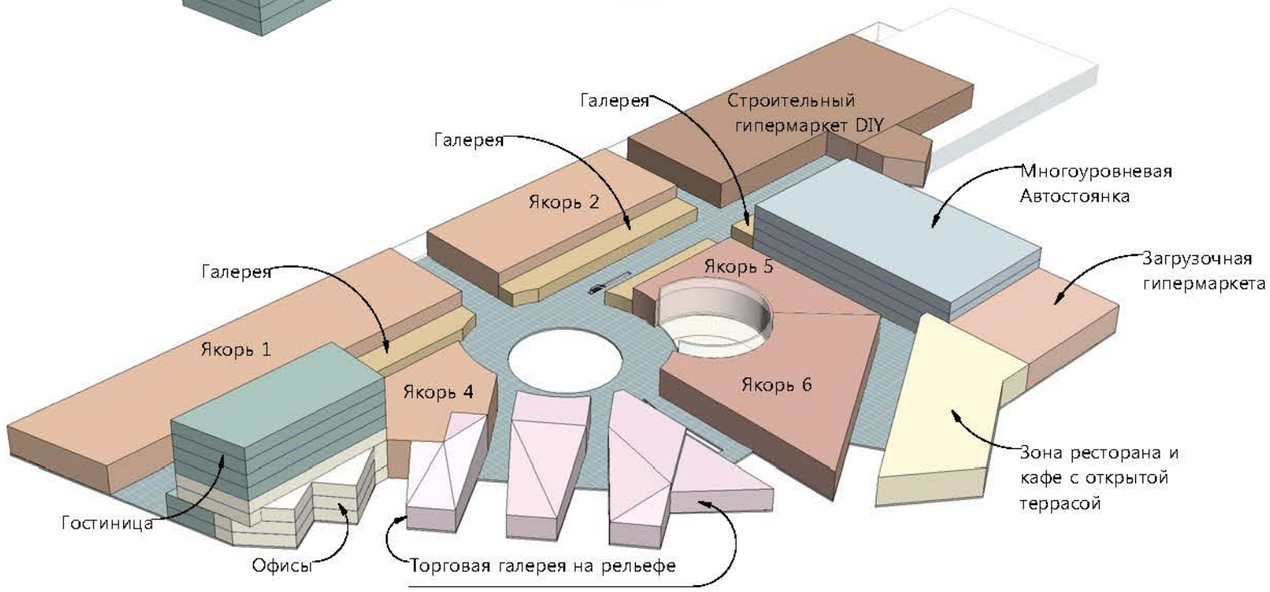

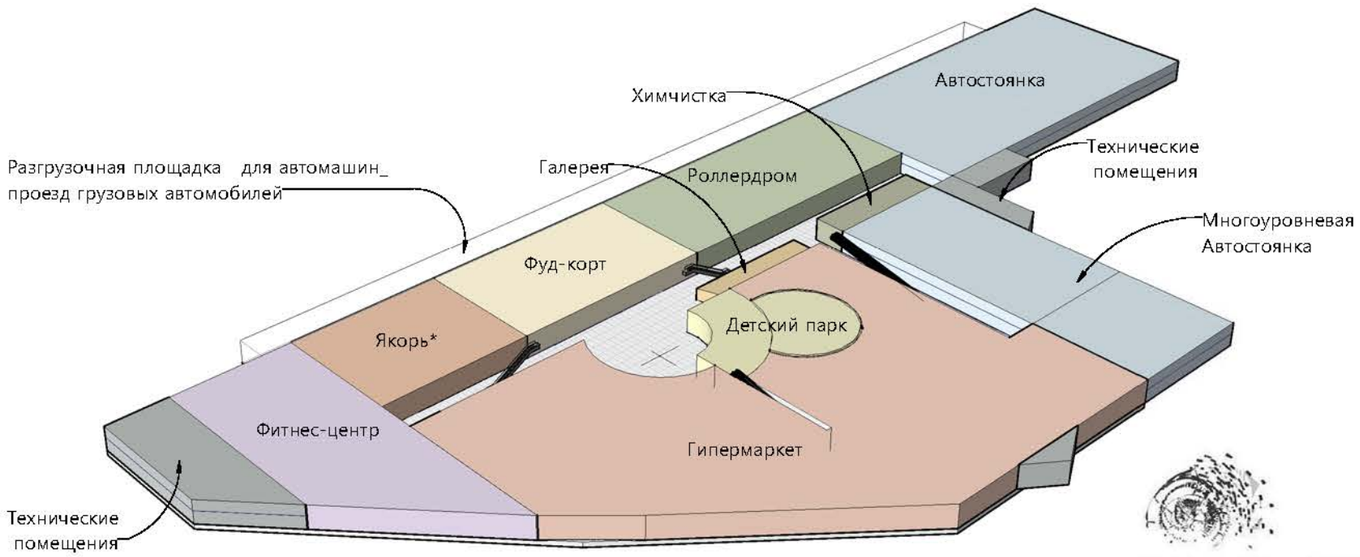

12, MYTNAYA STR., MOSCOW, RUSSIA, 119049
PHONE: +7 (499) 504 89 96
MAIL TO: SALIGRAMOFFICE@GMAIL.COM

SALIGRAM ARCHITECTURE, INTERIOR AND ENVIRONMENTAL DESIGN

+77.900
24 +73.500
23 +70.350
22 +67.200
21 +64.050
20 +60.900
19 +57.750
18 +54.600
17 +51.450
16 +48.300
15 +45.150
14 +42.000
13 +38.850
12 +35.700
11 +32.250
10 +29.400
9 +26.250
8 +23.150
7 +19.950
6 +16.800
5 +13.650
4 +10.500
3 +7.350
2 +4.200
1 ±0.000 185.00
183.4
2000
-1 -4.200
А
Б

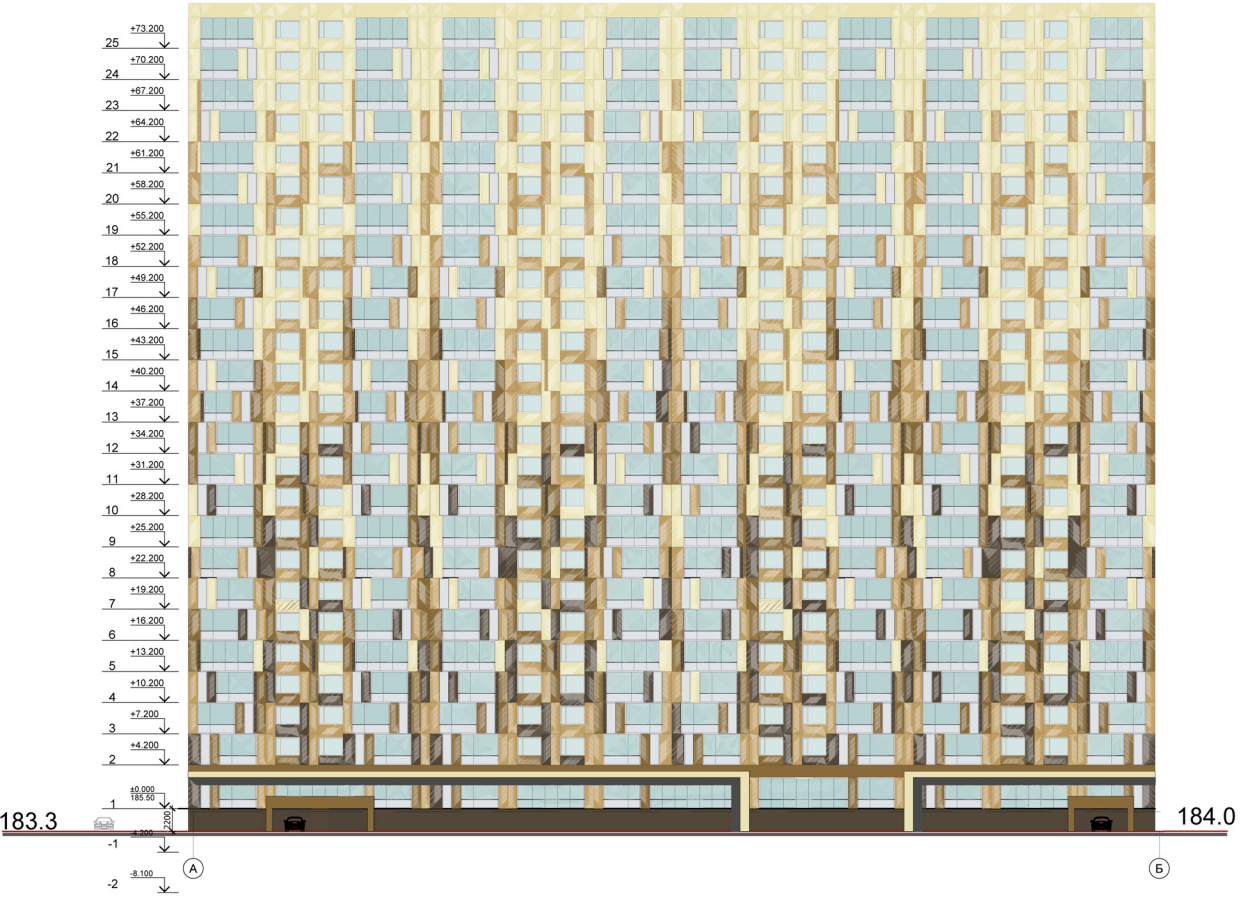
25 +73.200
24 +70.200
23 +67.200
22 +64.200
21 +61.200
20 +58.200
19 +55.200
18 +52.200
17 +49.200
16 +46.200
15 +43.200
14 +40.200
13 +37.200
12 +34.200
11 +31.200
10 +28.200
9 +25.200
8 +22.200
7 +19.200
6 +16.200
5 +13.200
4 +10.200
3 +7.200
2 +4.200
1 ±0.000 183.50
-1 -4.200
-2 -8.100
3200
183.3
184.0
А
Б

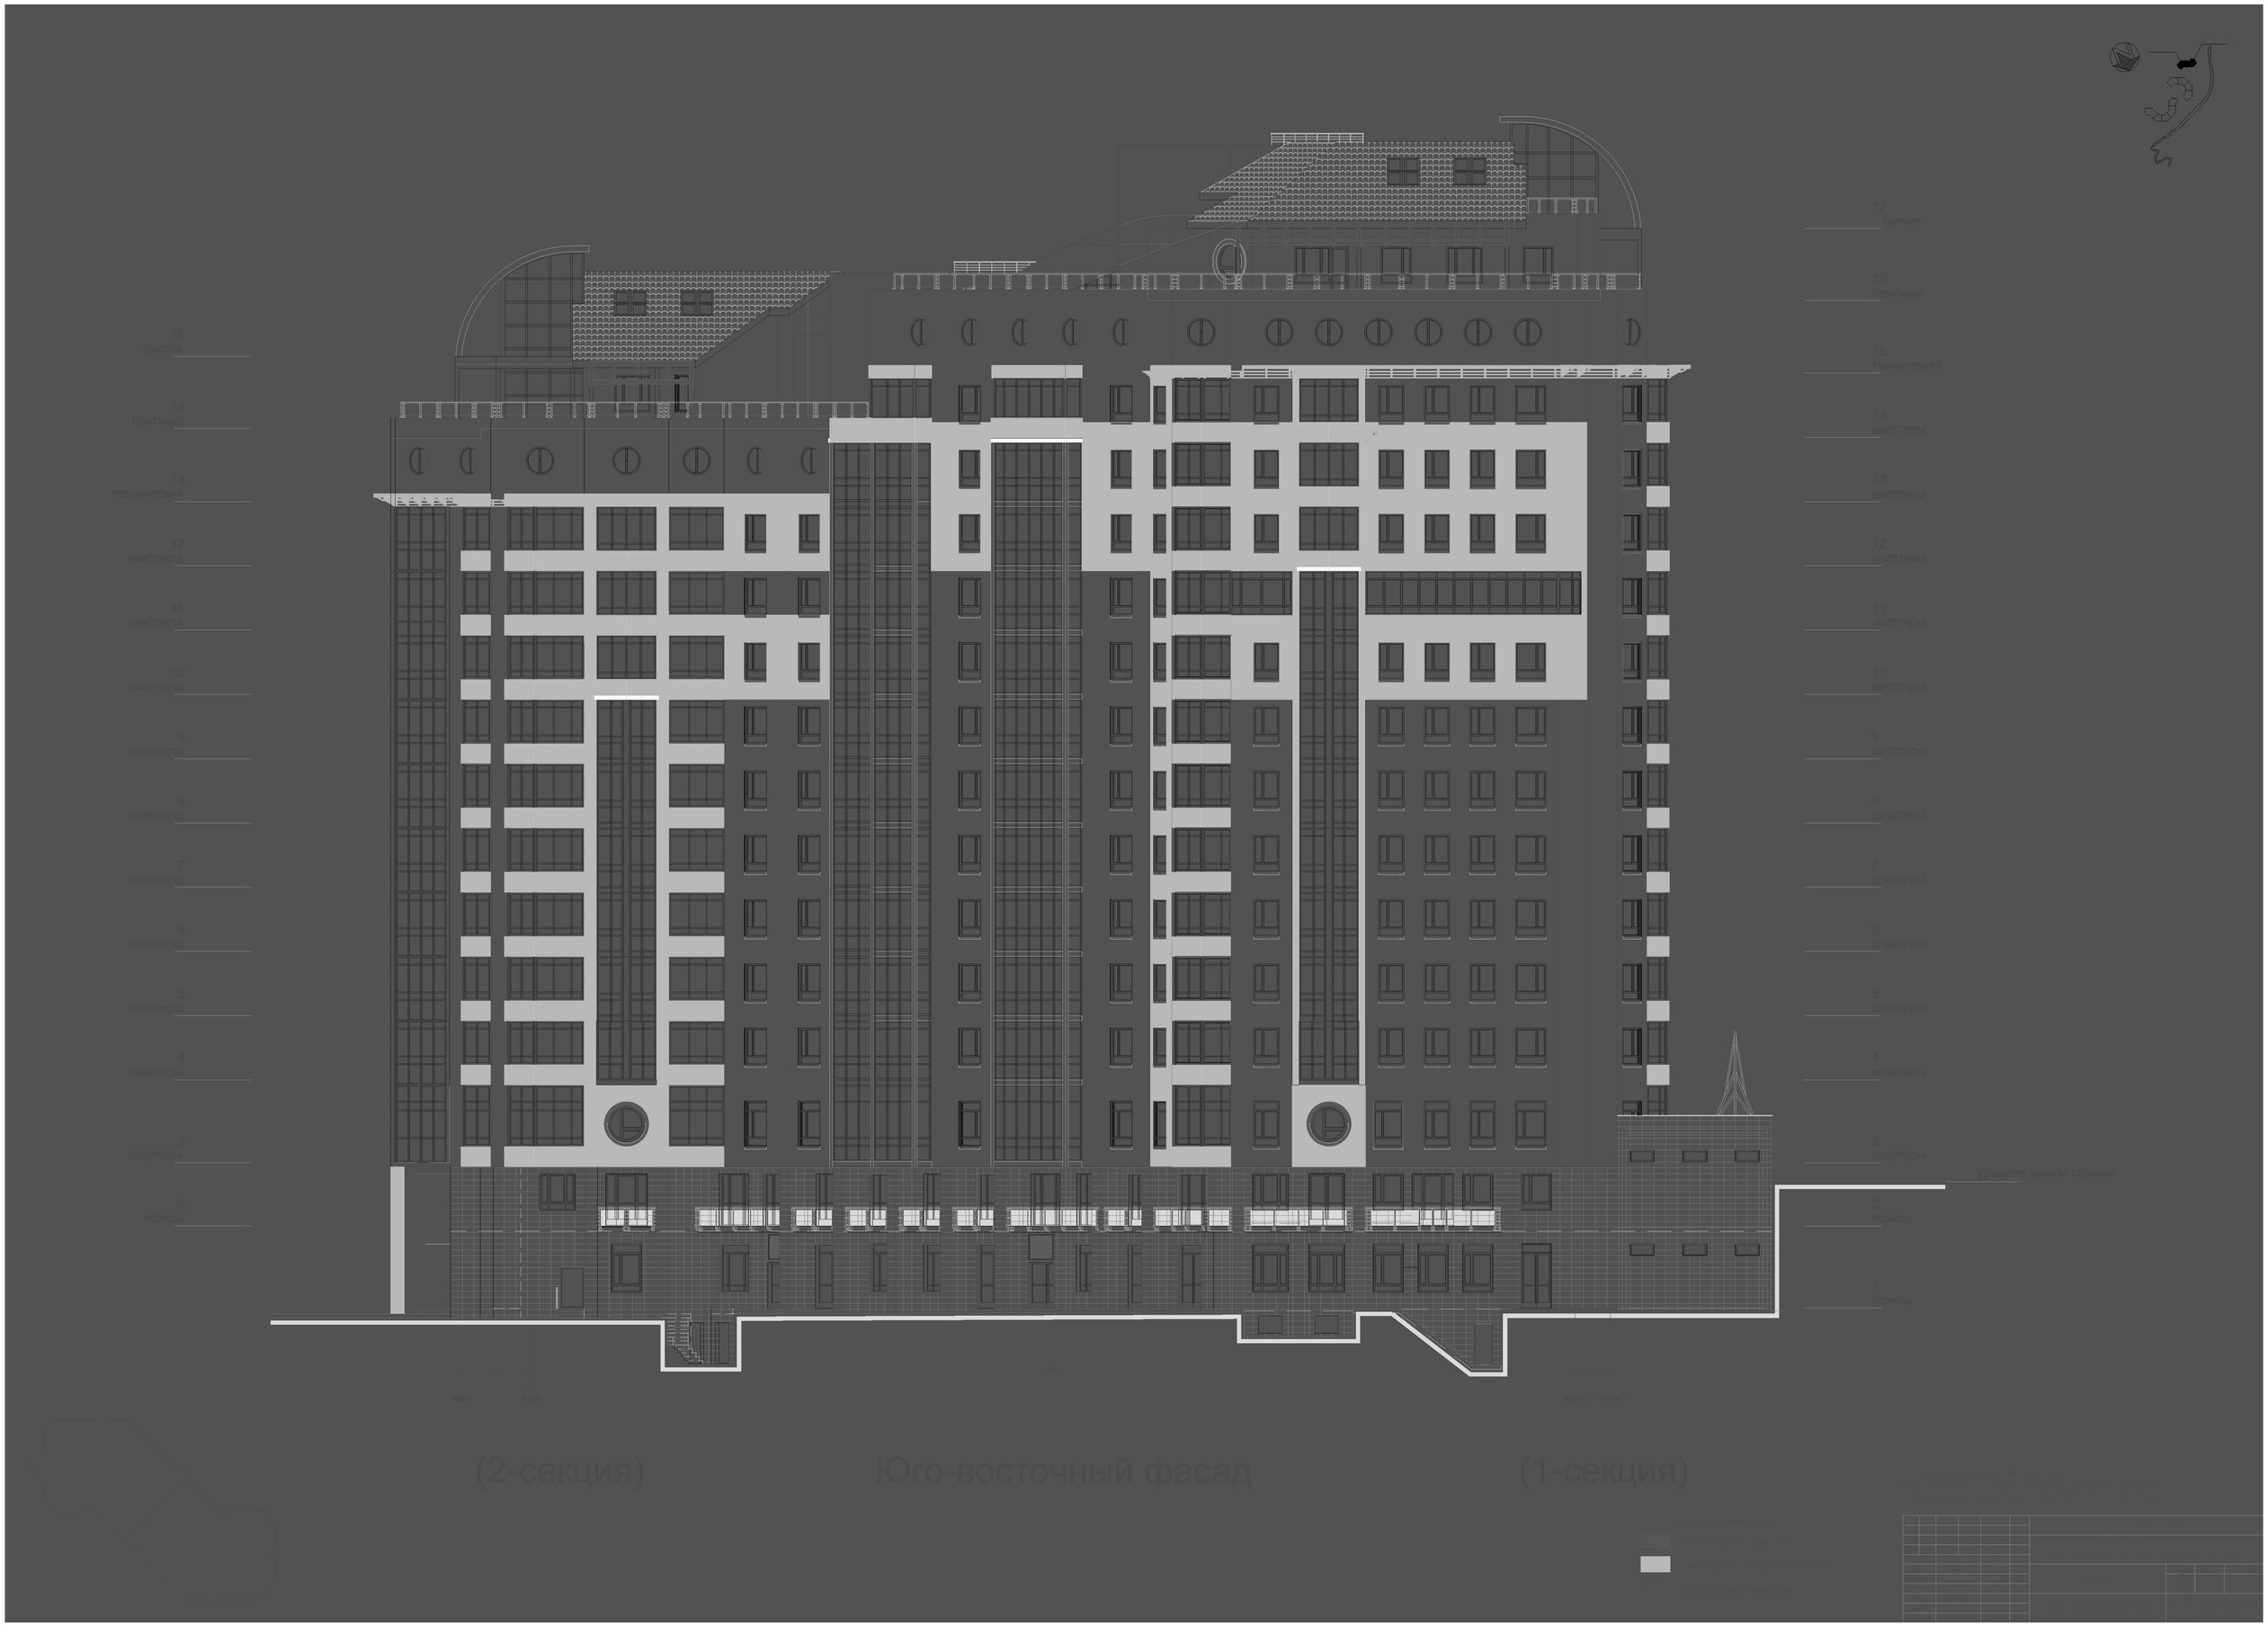
17
кровля
16
пентхаус
15
технический
14
квартиры
13
квартиры
12
квартиры
11
квартиры
10
квартиры
9
квартиры
8
квартиры
7
квартиры
6
квартиры
5
квартиры
4
квартиры
3
квартиры
2
офисы
1
офисы
15
кровля
14
пентхаус
13
технический
12
квартиры
11
квартиры
10
квартиры
9
квартиры
8
квартиры
7
квартиры
6
квартиры
5
квартиры
4
квартиры
3
квартиры
2
офисы
уровень земли гаража
(2-секция)
Юго-восточный фасад
(1-секция)

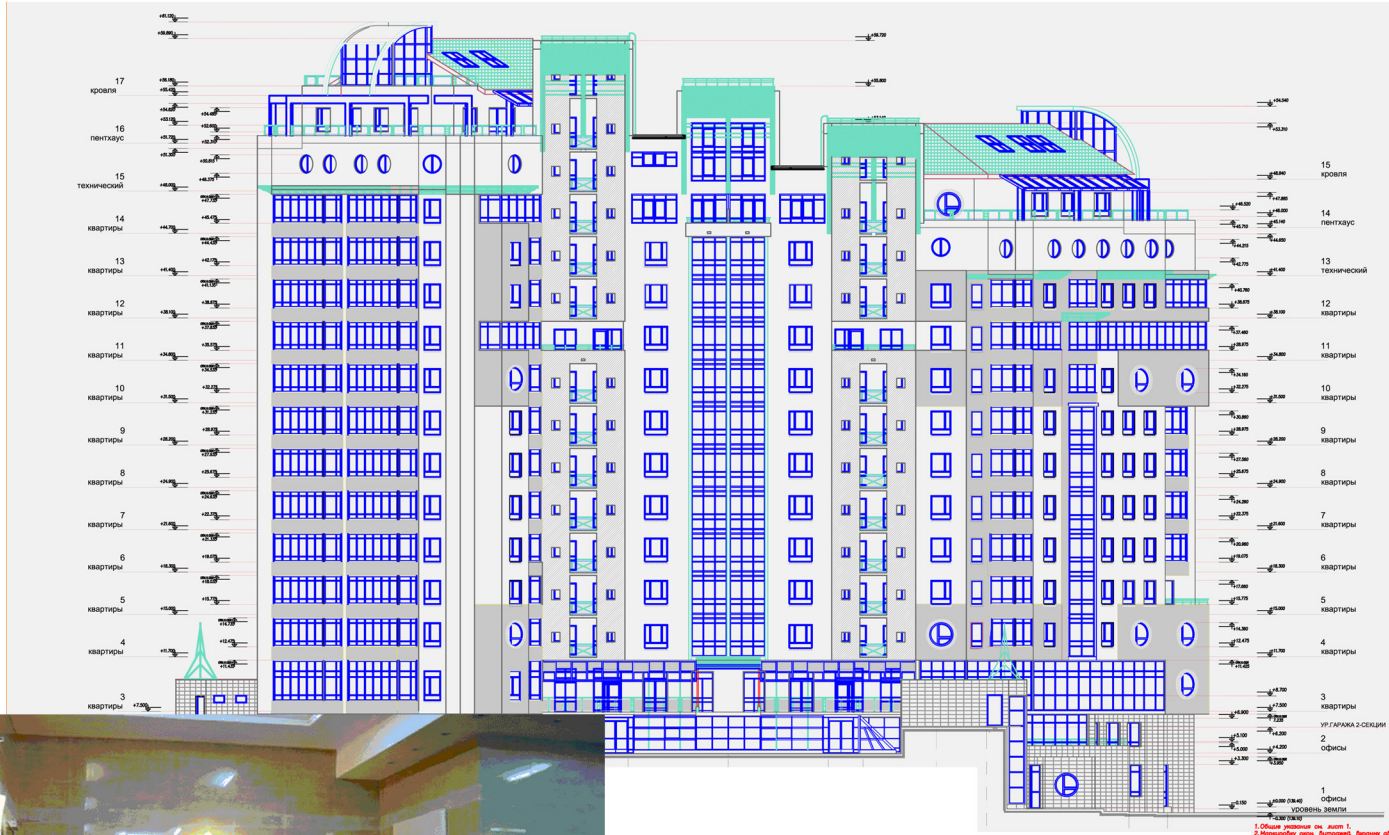

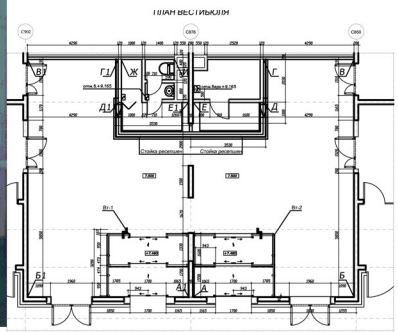

1. Общие указания см. лист 1.
2. Маркировку окон, витражей, дверных дверей и спецификацию к ним см. АР-1 л. 2 – 3,5
3. Крепление ограждения лестничных клеток 11 этажа, открытого балкона 5 этажа и центрального балкона 14 этажа (СО2, СО3, СВ78) смотрите лист 16 АР-01 (обвязочный брус ограждения СГ-9 смотрите лист 20 АР-01) обвязочный брус ограждения ср 1215 мм с наклонным поясом. Стойки наружного ограждения прибрать к металлоконструкциям, горизонтально ограждения с шагом 900мм.
4. Трубы бетонных усиливы не показаны.

						001-01-АР-II	
Изм.	Кол.	Лист	N док.	Подпись	Дата		
Гл. инженер проекта						Жилой комплекс на ул. Маяков пр. 726; 6а 1	
Гл. архитектор проекта						Корпус 1	Стадия Лист Листов П 2
Разраб.						Северный фасад	ЗАО"СК Стройинвест" г. Москва
Проверил							
Согласов.							

Условные обозначения изделий и оборудования на первую и вторую секции.

Поз	Обозначение	Наименование	Кол-во	Примечание
1	ДБн-1	Деревянный дверной блок	2	Серия 001-01-АР
2	Дор-1	Алюминиевая раздвижная дверь	2	См. лист 15
3	ДВн3,3 ДВн3	Двери остекленные REI 30, REI 120,3	2	См. лист 17
4	ДВ-5а	Деревянный блок REI 120,3	2	См. лист 35
5	ДВ-6	Деревянный блок REI 120,3	1	См. лист 35
6	ДБр-1	Дверь раздвижная REI 120,3	1	См. лист 35
7	Вн-1 Вн-2	Алюминиевая витражная конструкция	1 1	См. лист 15

Условные обозначения изделий и оборудования

- Встраиваемый светильник
- Потолочный светильник
- Настенный светильник
- Громкоговоритель
- Извещатель дымовой
- Извещатель ручной
- Пункт вкл. потолочных и настенных осветительных приборов
- Розетка для электрооборудования
- Маркировка изделий и оборудования

Условные обозначения материалов

1– Керамический гранит 30x60 "Sigma-PR-Crema"
2– Керамический гранит 30x60 "Grasan R Crema"
3– Декоративная штукатурка Russ-2000 R02
4– Керамический гранит 15x30 "Zocalo Grasan Crema"
5– Керамический гранит 7,5x30 арт.«Gobra Crema"
6– Подвесной потолок "Ecophon Light Coffer"
6.1– Подвесной потолок 60x60 "Oasis plus"
6.2– Гипсокартонные плиты
7– Керамический гранит 2x30 арт.«Twin Beige"
8– Керамическая плитка 33x33 "Bertoria Bay"
9– Керамический гранит 10x40 "Tiro Zaser PR Burgona"
9.1– Керамический гранит 10x10 "Tiro Zaser PR Burgona"
10– Напольный гранит 40x40 "Tenera"
11– Напольный гранит 40x40 "Кутаиниоиа"

1. Общие указания см. лист 1.
2. Данный лист смотри с ведомостью материалов лист 5.1.
3. Данный лист смотри с листом 16.
4. Обвязку черновиков торцов витражей и монтаж потолка выполнить только после монтажа витражной конструкции.
5. Обвязку гипсокар. окрашивать выполнить после монтажа см.тех. оборудования.
6. Показы спецификации изделий и оборудования дана в кружочках.
7. Количество осветительных приборов определяется после расчета ЭО.

2001-03

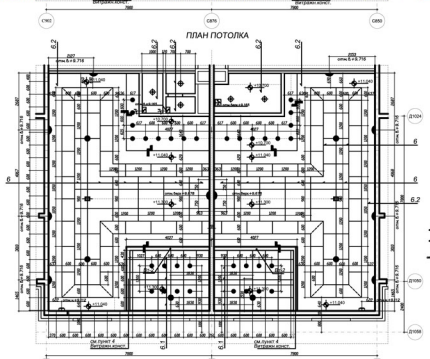

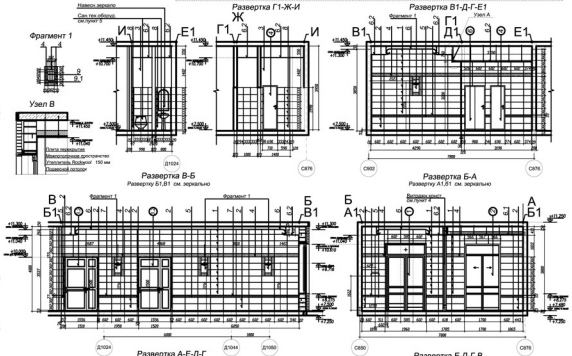

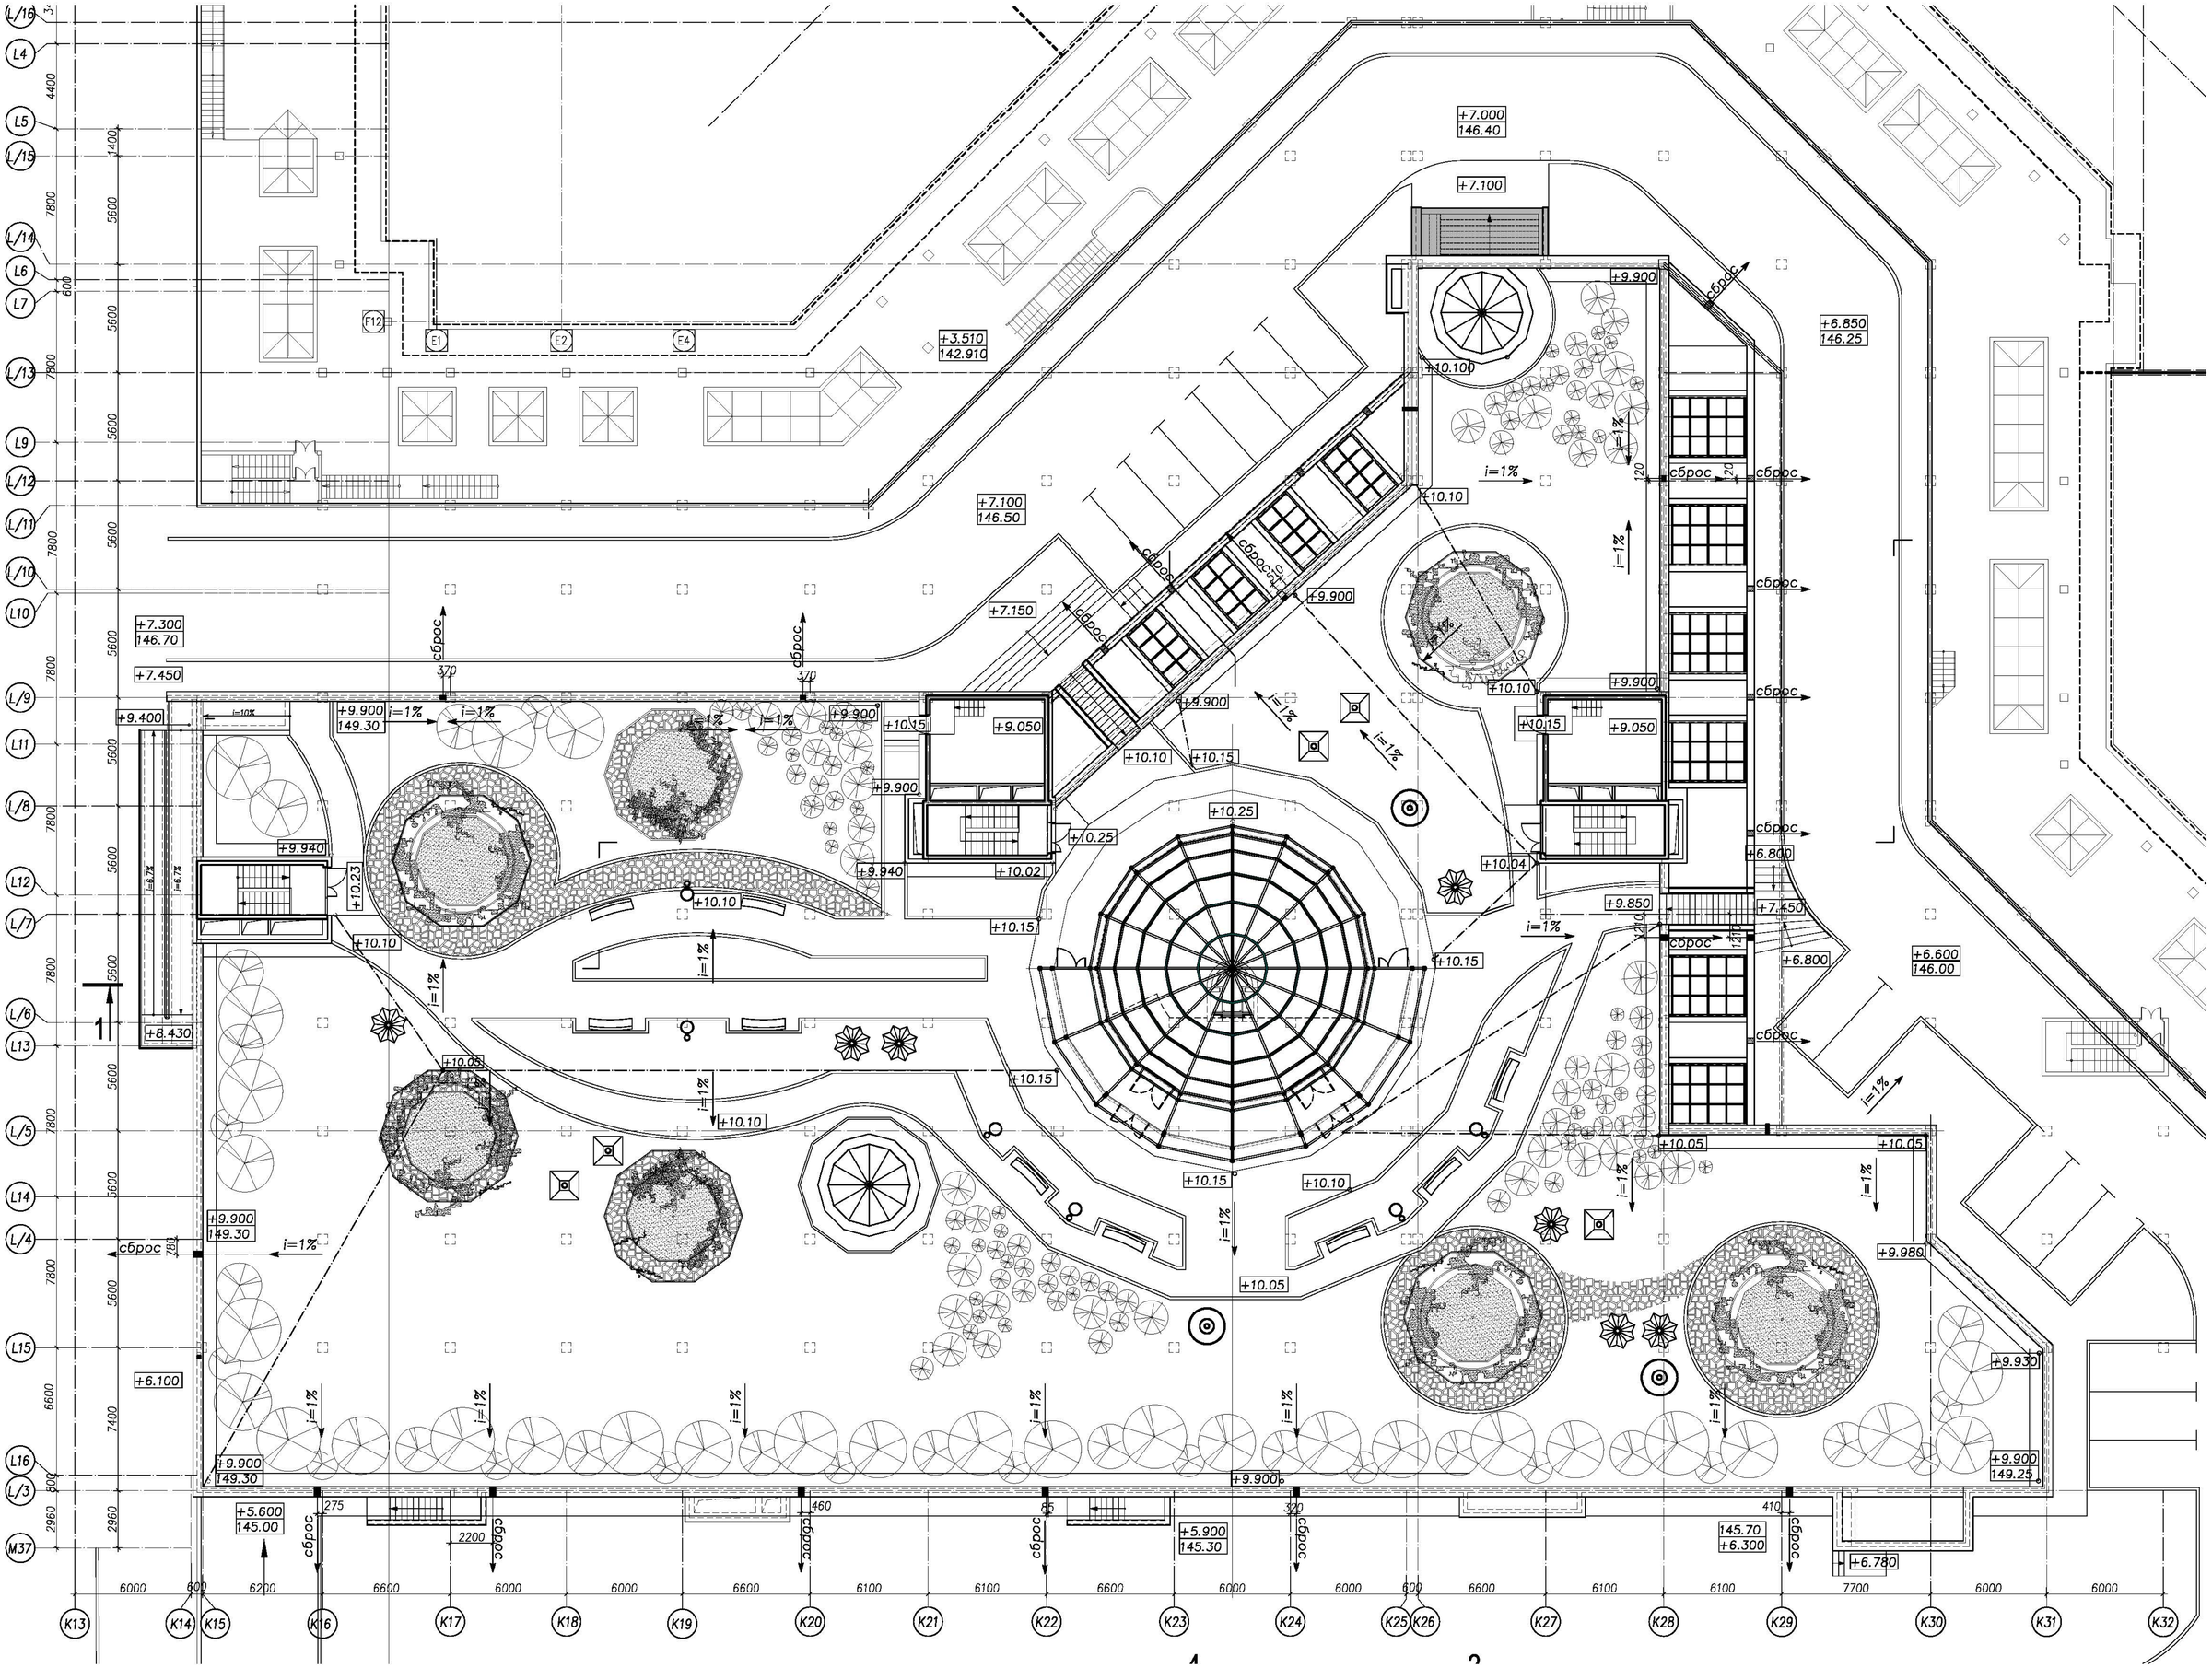
+7.000
146.40
+7.100
+6.850
146.25
+3.510
142.910
+7.100
146.50
+7.300
146.70
+7.450
+9.400
+9.900
149.30
+9.940
+8.430
+6.100
+5.600
145.00
+5.900
145.30
145.70
+6.300
+6.780
+6.600
146.00
+9.850
+6.800
+7.450
+9.980
+9.930
+9.900
149.25
+10.10
+10.15
+10.25
+10.02
+10.04
+10.05
+10.23
+9.050
сброс
i=1%
i=10%
i=6.7%
F12
E1
E2
E4
L/16
L4
L5
L/15
L/14
L6
L7
L/13
L9
L/12
L/11
L/10
L10
L/9
L11
L/8
L12
L/7
L/6
L13
L/5
L14
L/4
L15
L16
L/3
M37
K13
K14
K15
K16
K17
K18
K19
K20
K21
K22
K23
K24
K25
K26
K27
K28
K29
K30
K31
K32