Зал Конгресс холла

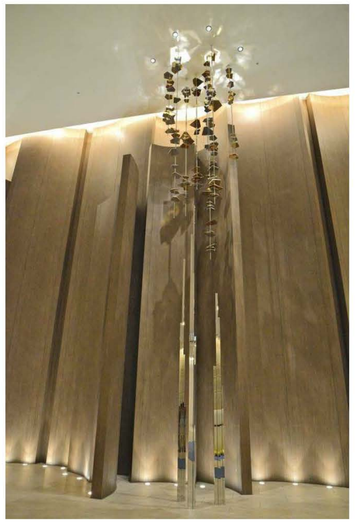

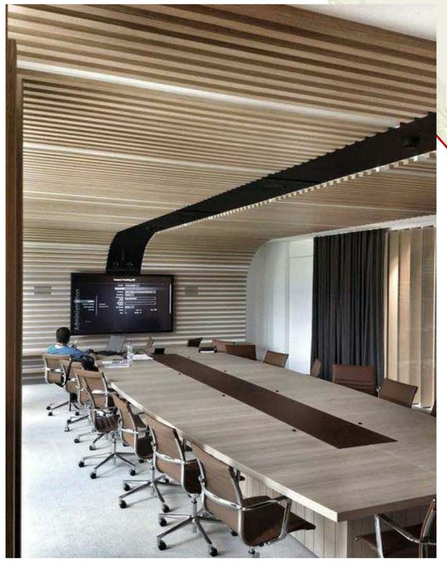

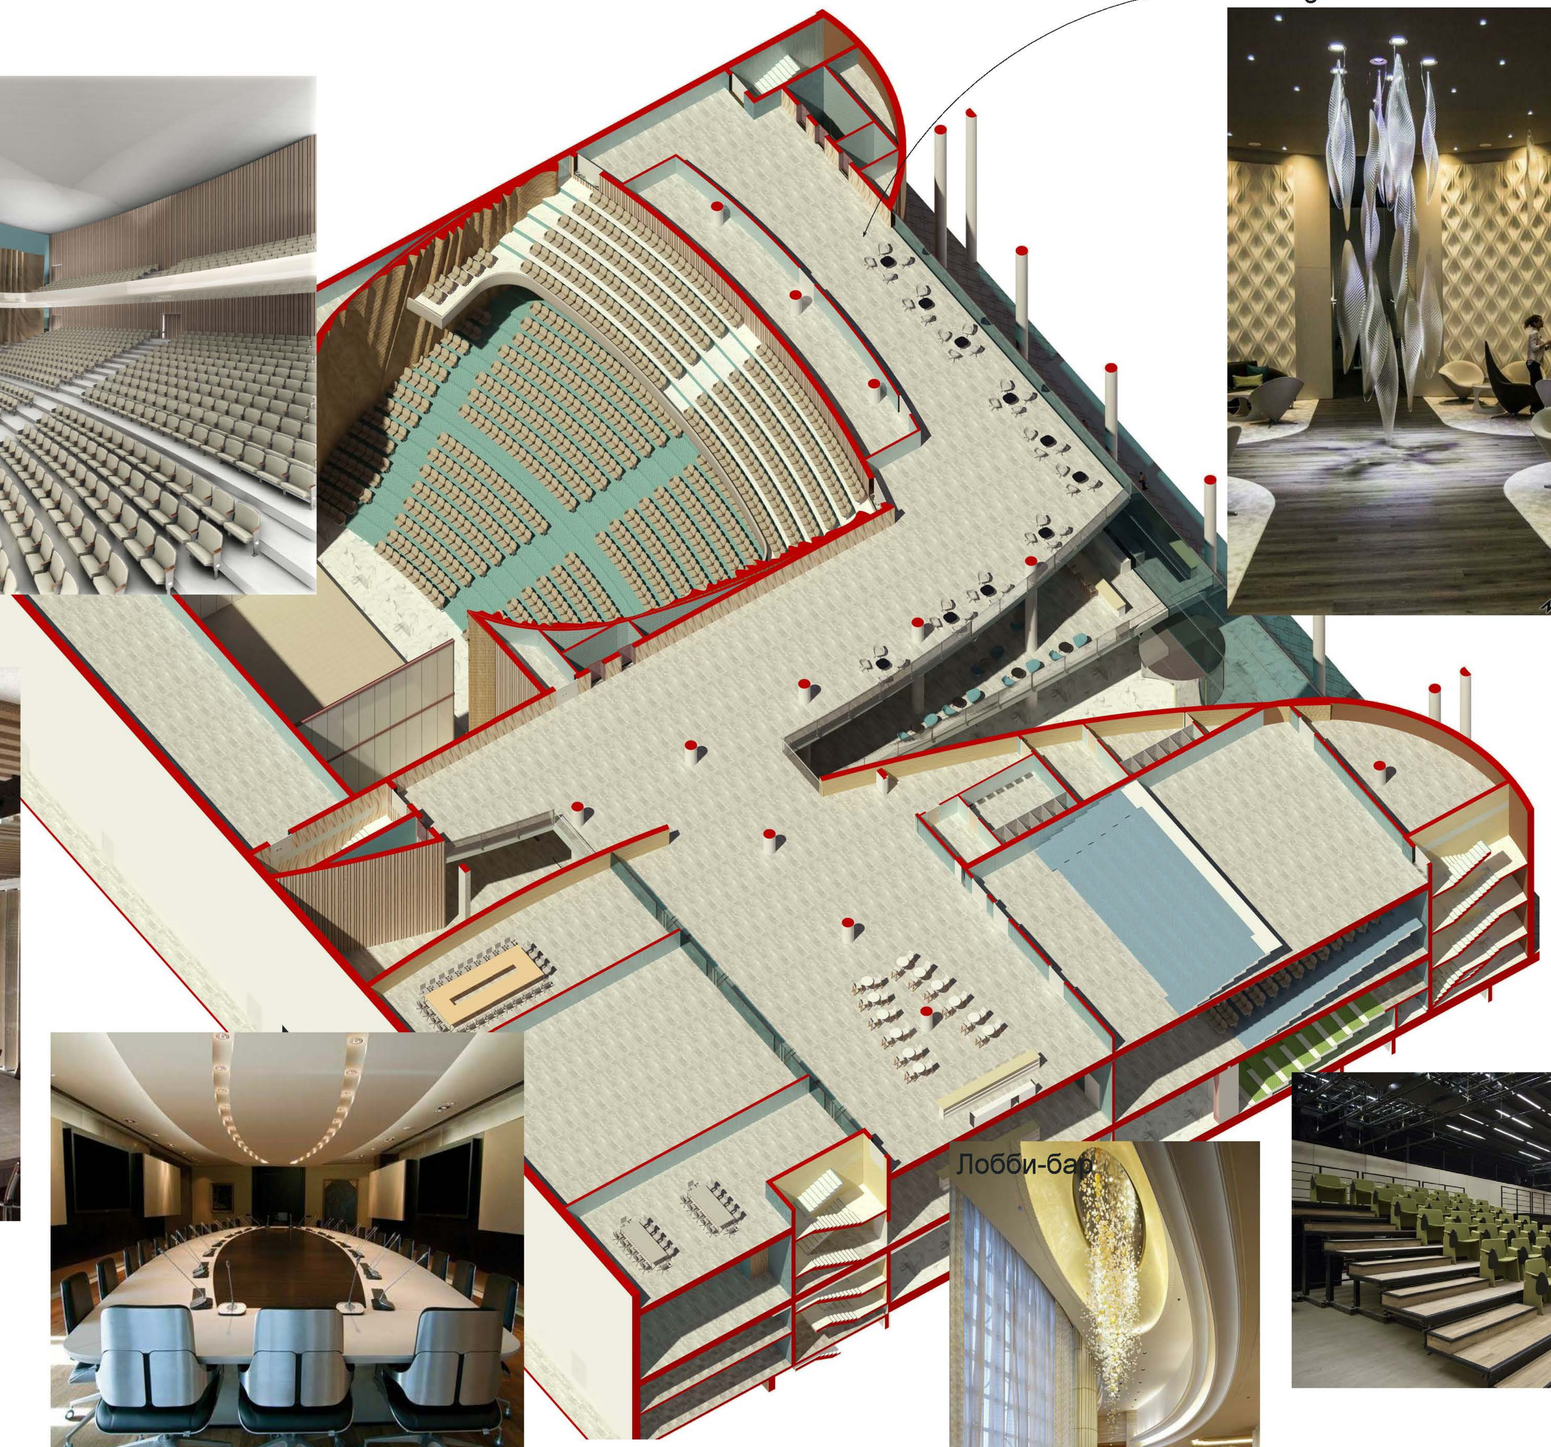

Lounge зона

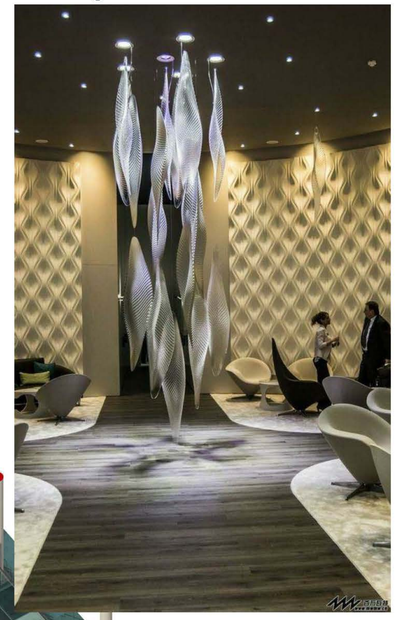

Трансформируемый
многофункциональный зал

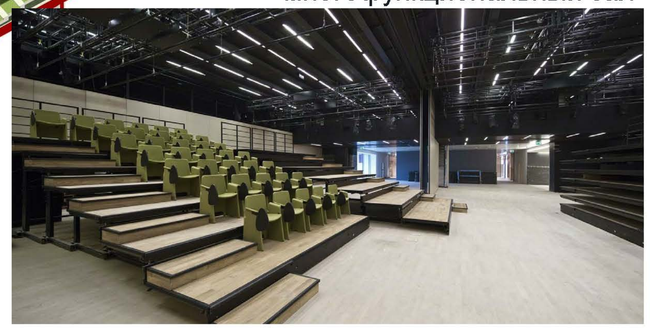

Лобби-бар

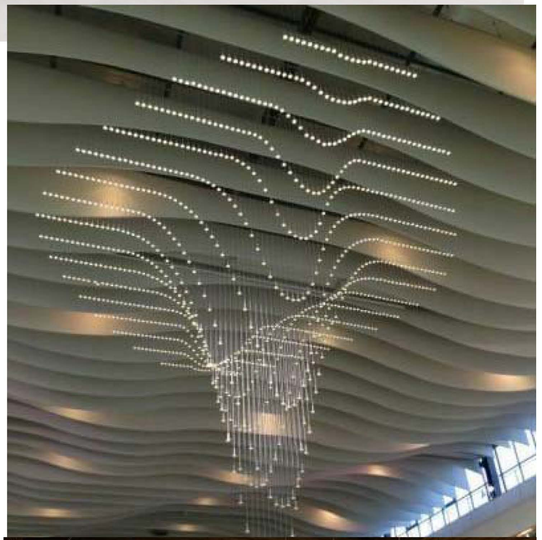

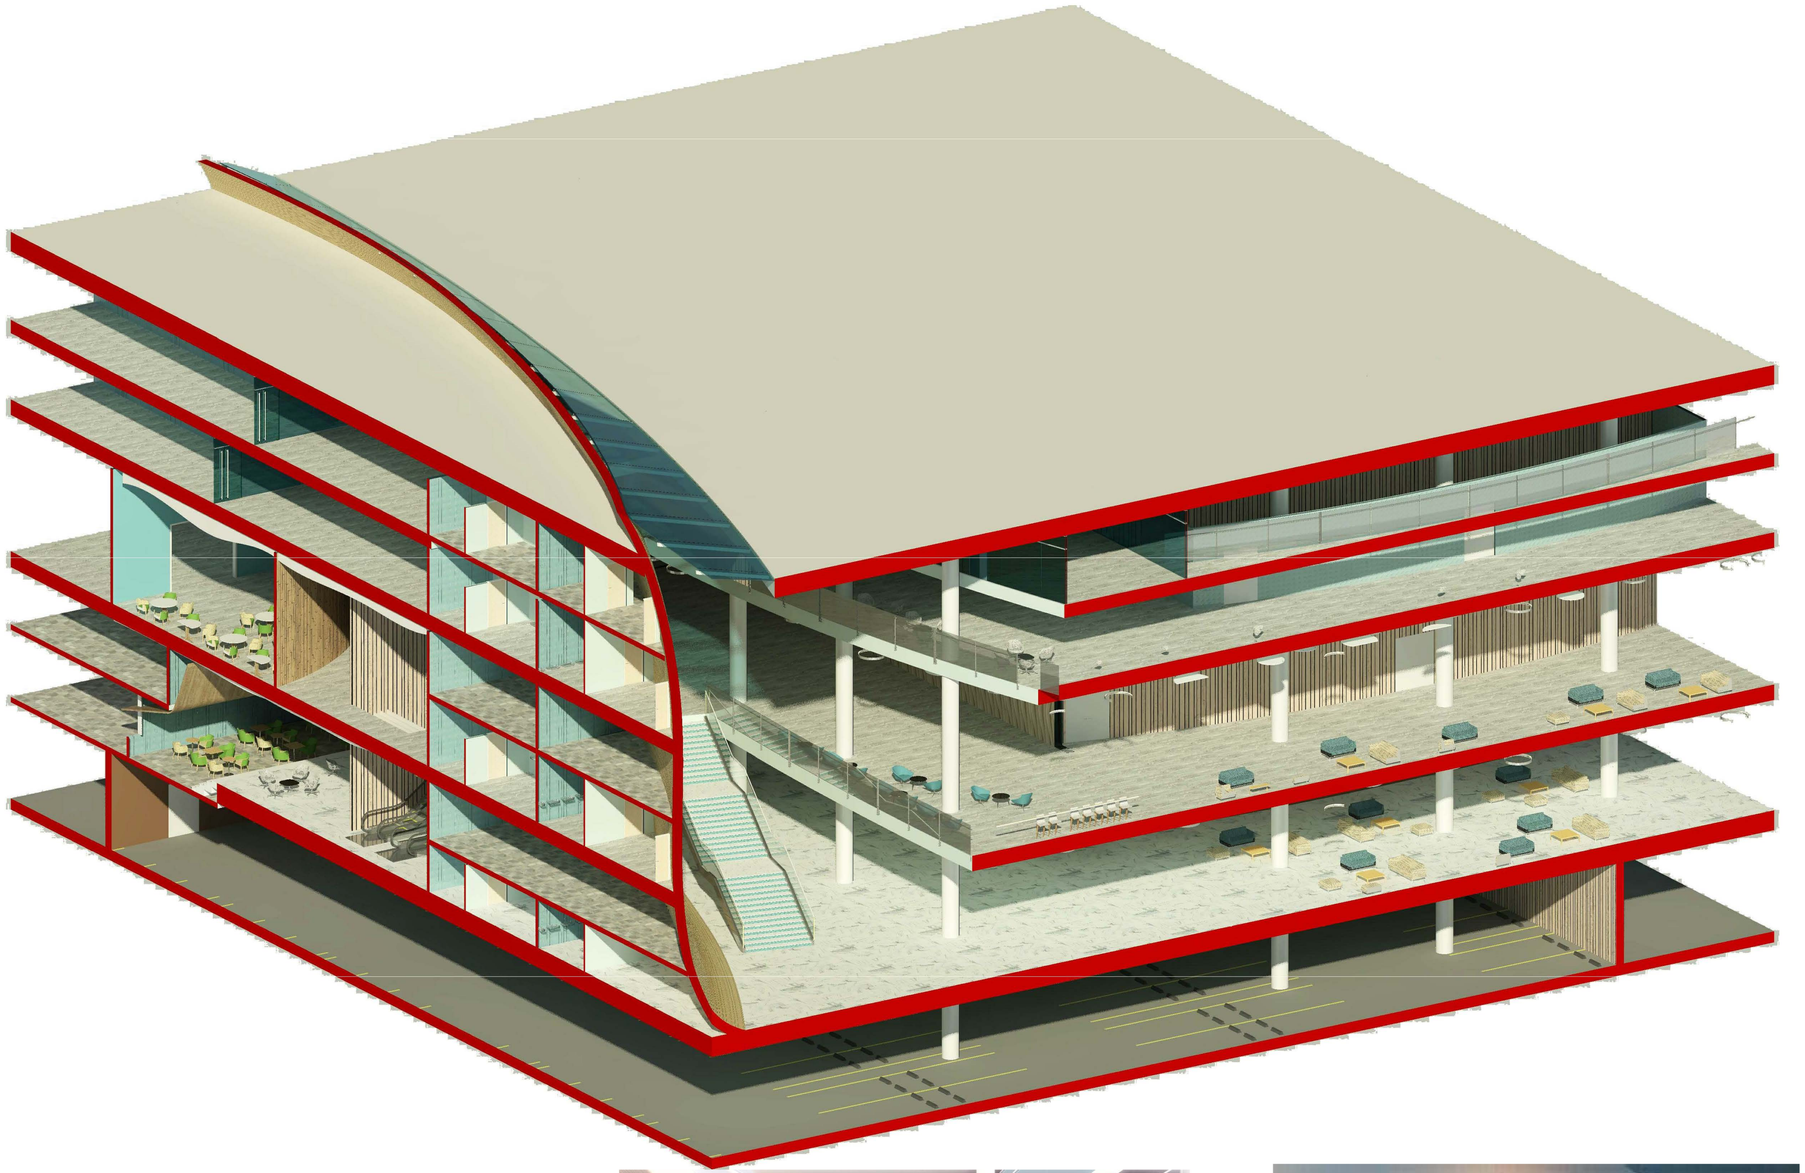

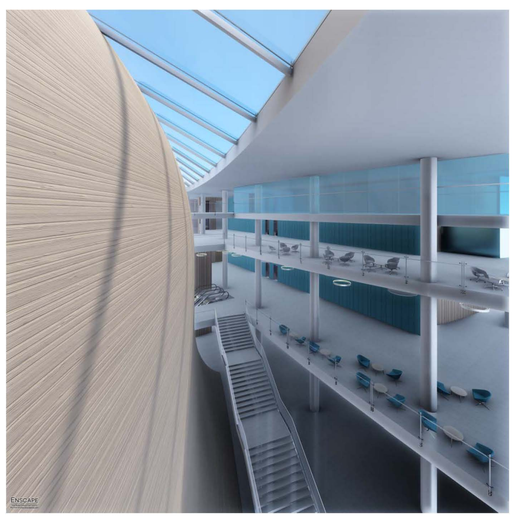

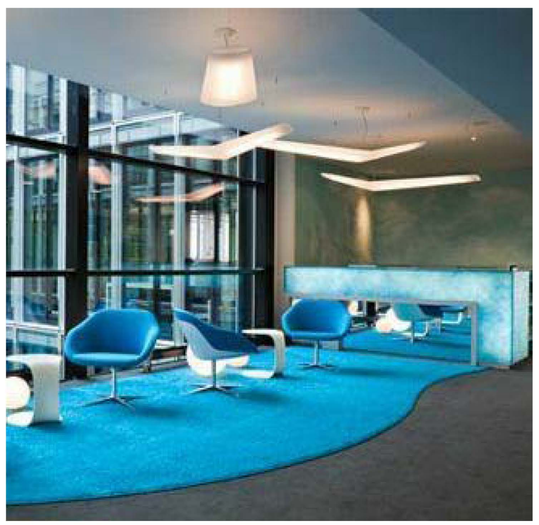

Производственные помещения предприятия питания

Кафе

Ресторан

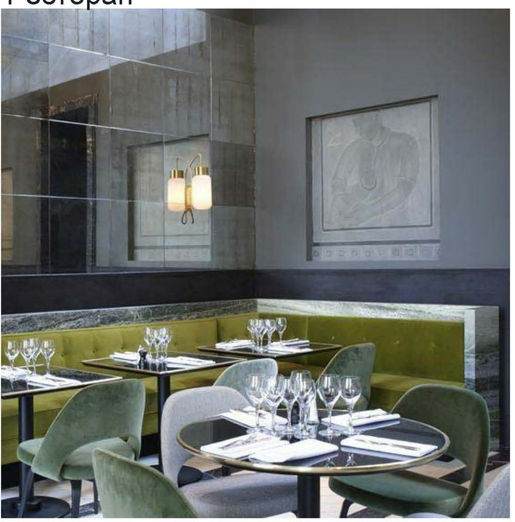

Lounge зона

Трансформируемый многофункциональный зал

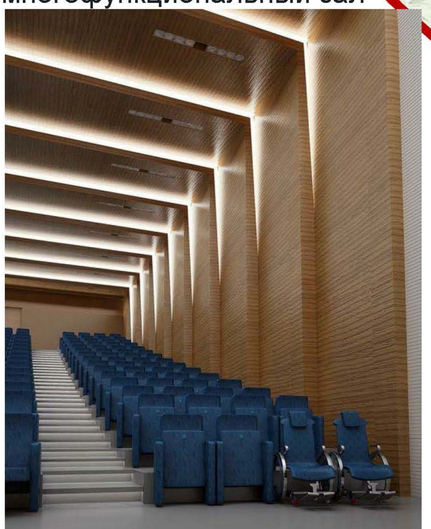

Лобби-бар

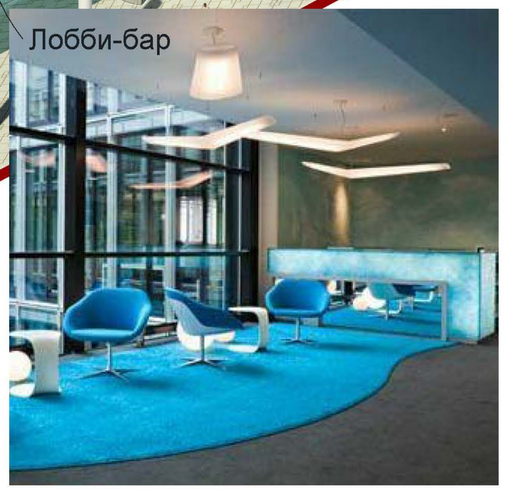

Сцена

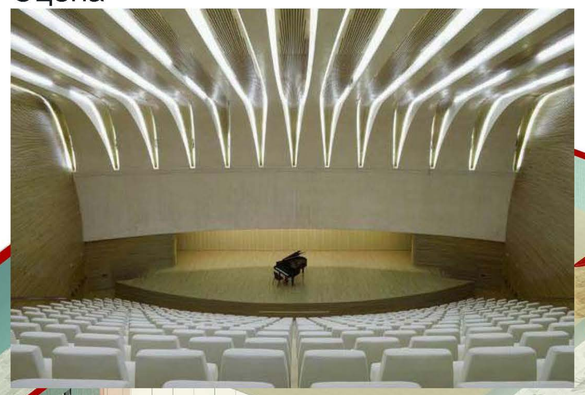

Lounge зона

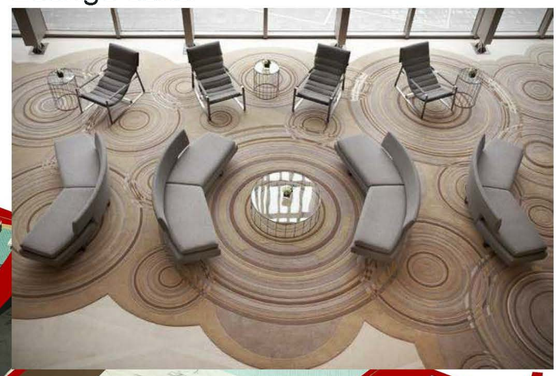

Производственные помещения предприятия питания

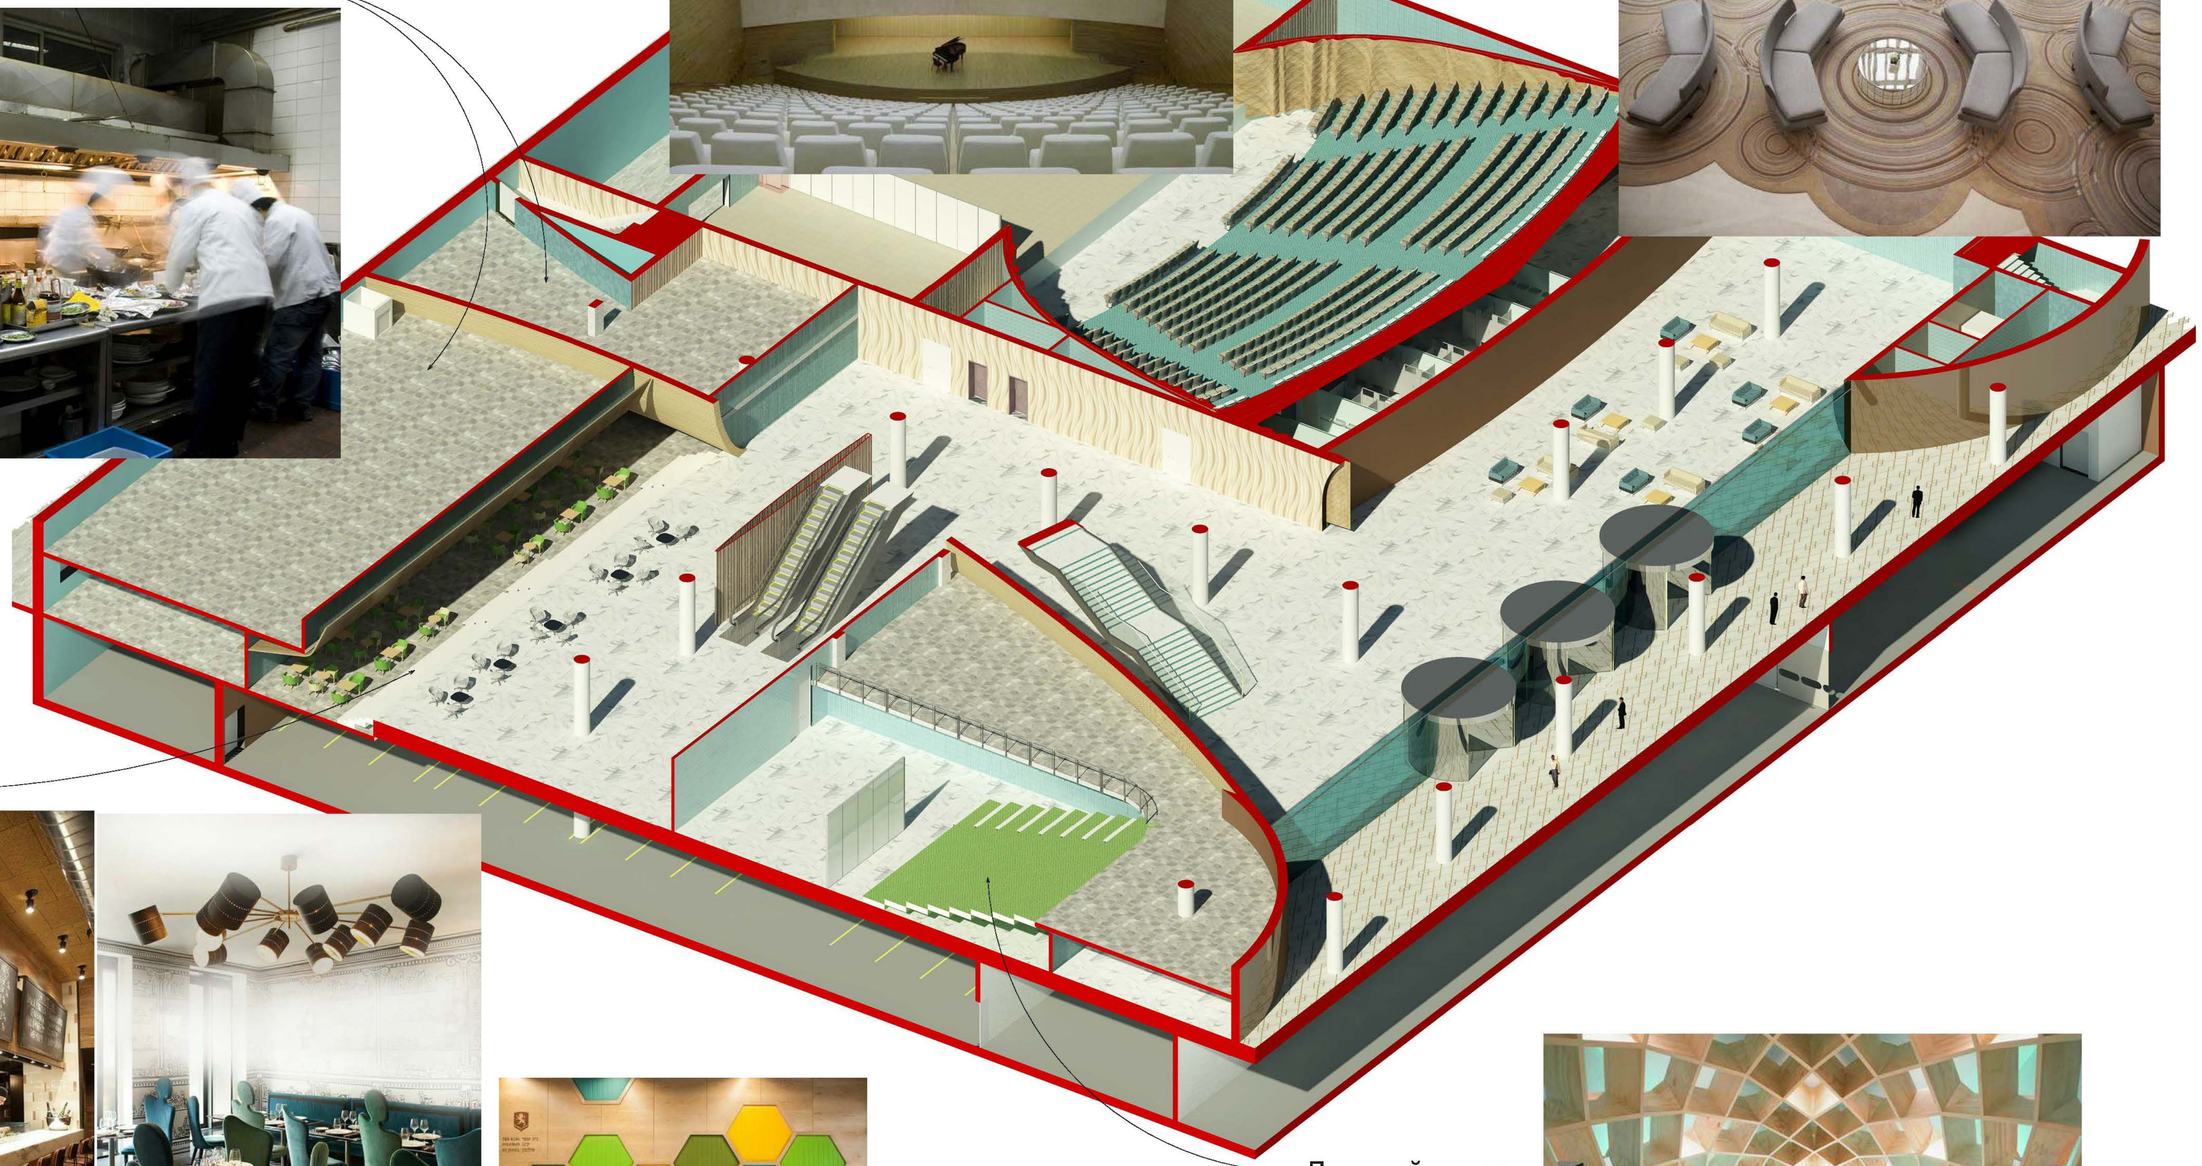

Кафетерий

Детский центр

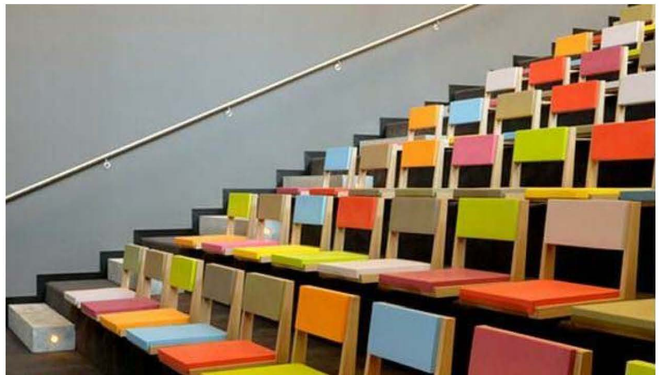

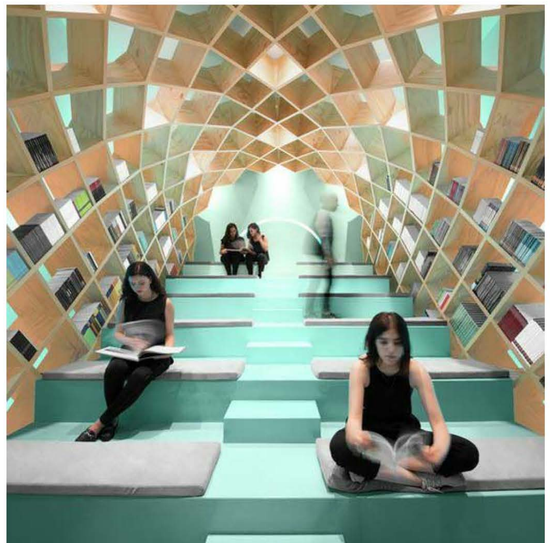

Зал Конгресс холла

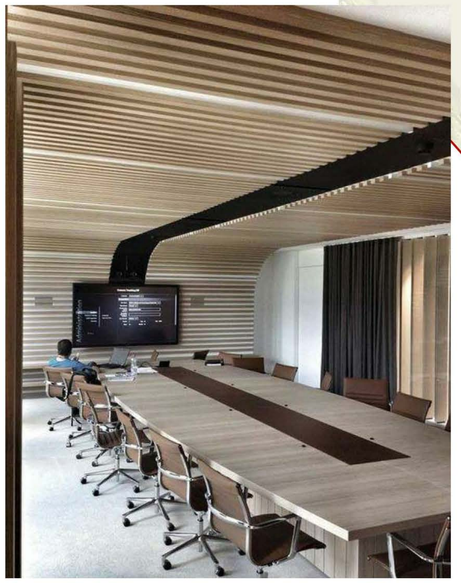

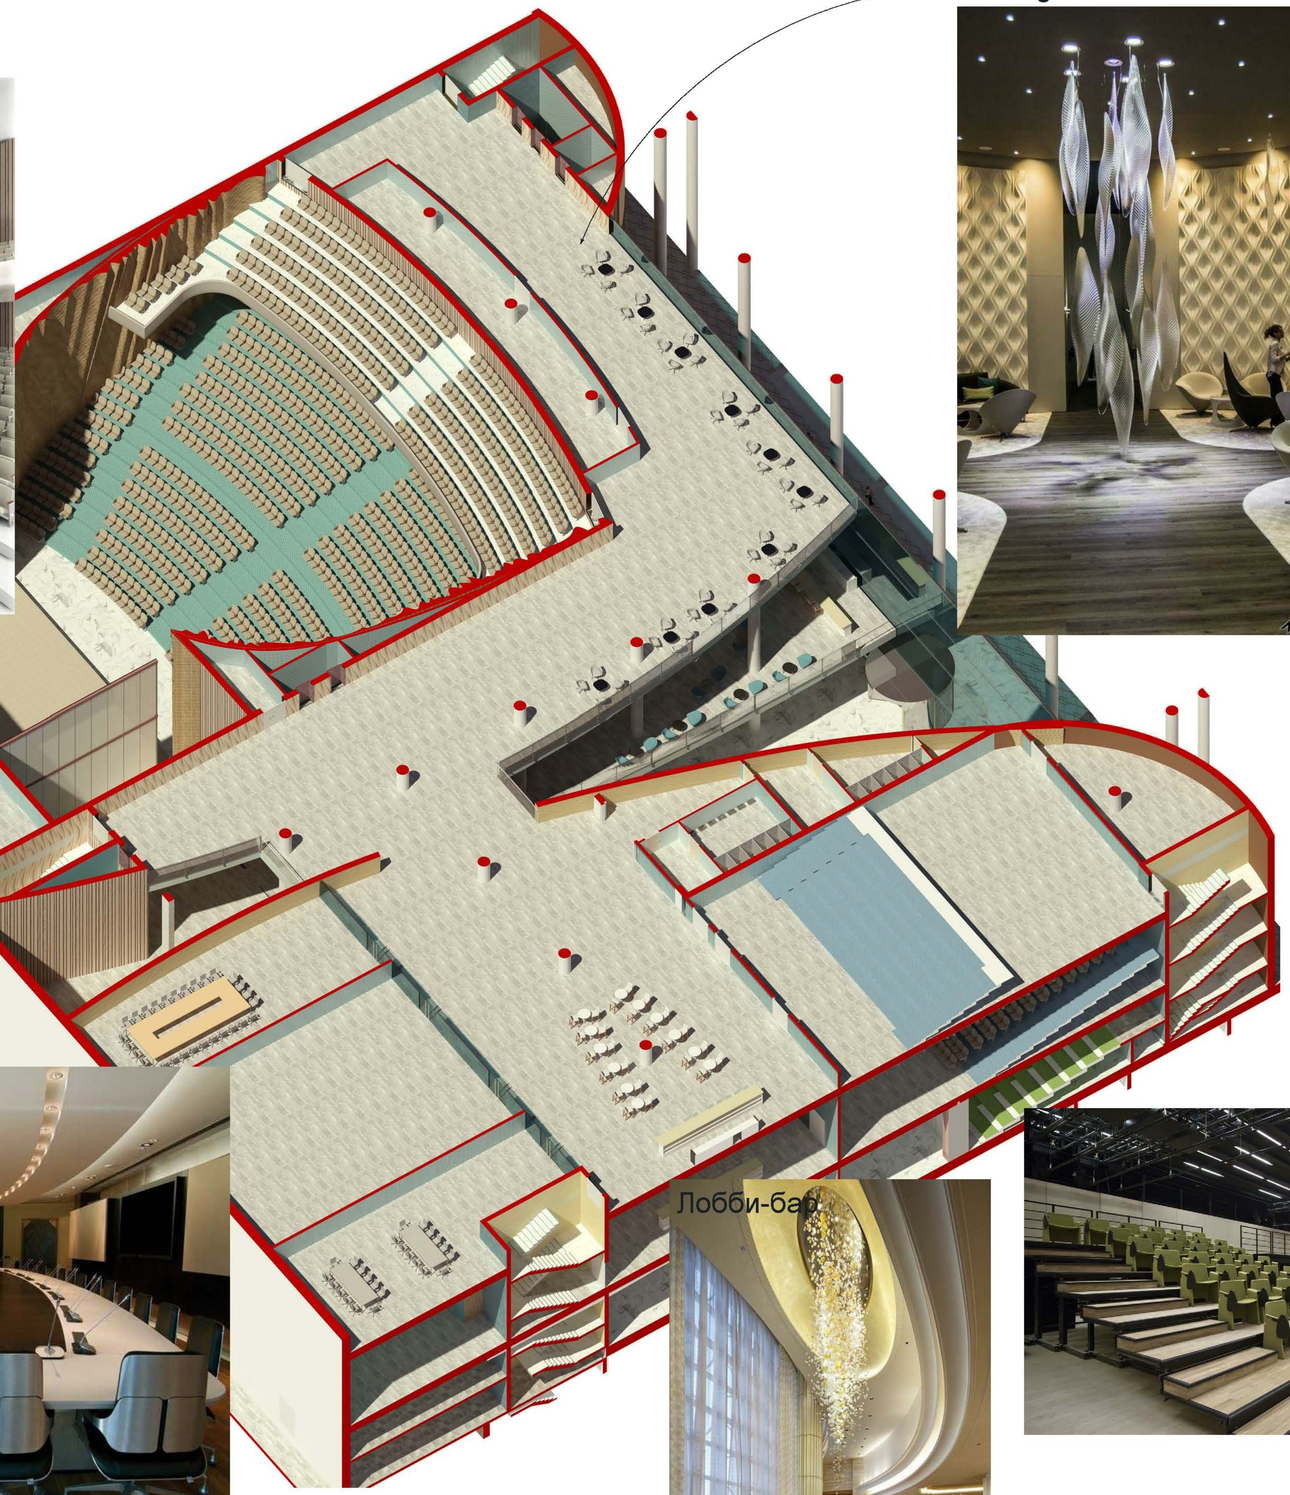

Lounge зона

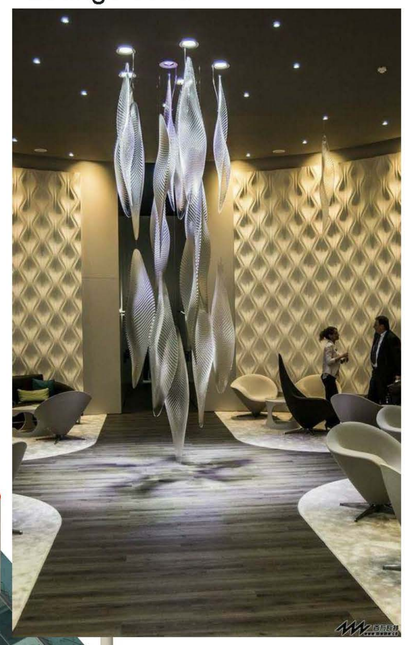

Трансформируемый многофункциональный зал

Лобби-бар

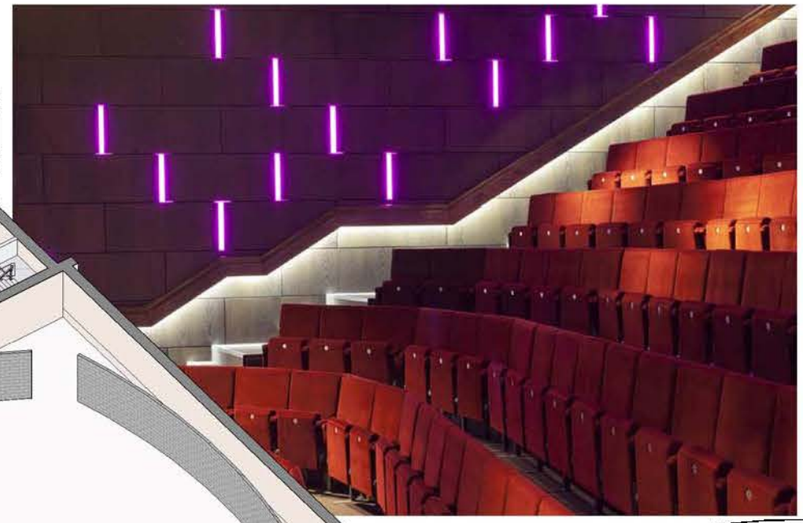

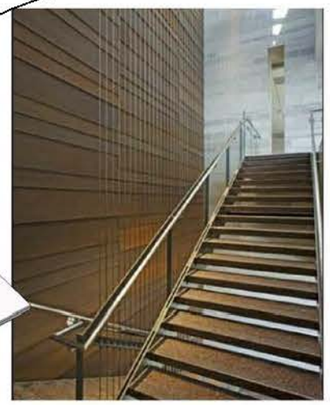

Фойе_Лонж зона

Универсальный зал (игровой,спортивный,для танцев, ивентарные)

Декоративные элементы фасадаиз полимербетона

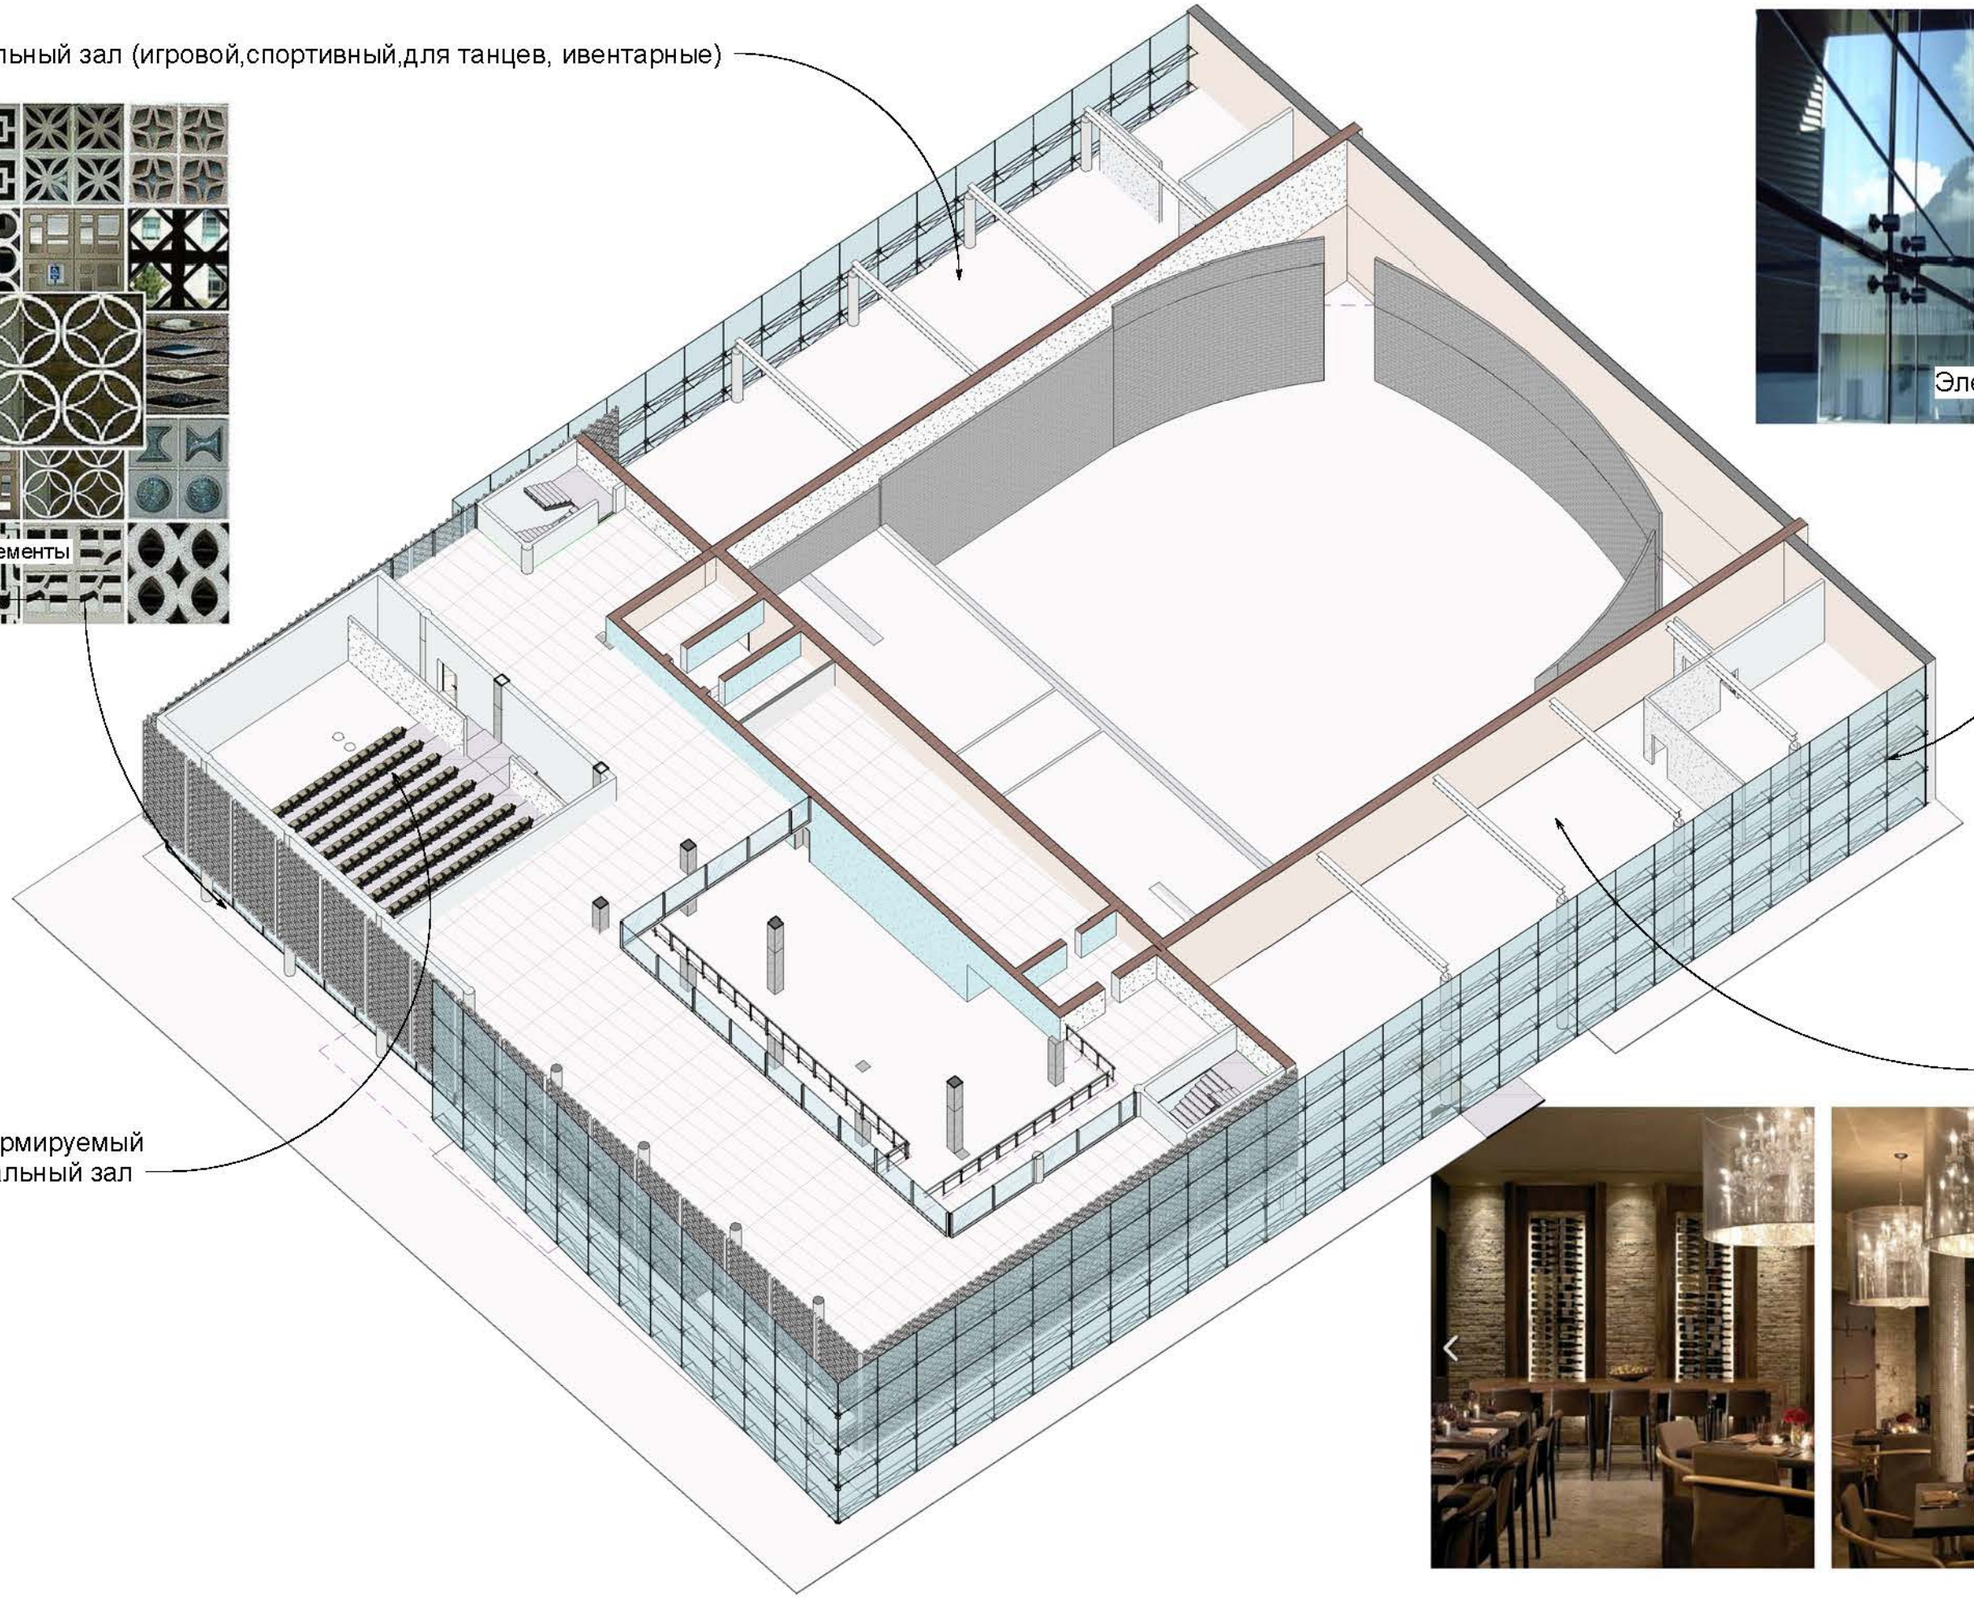

Элемент Фасада

Трансформируемый универсальный зал

Кафе-ресторан

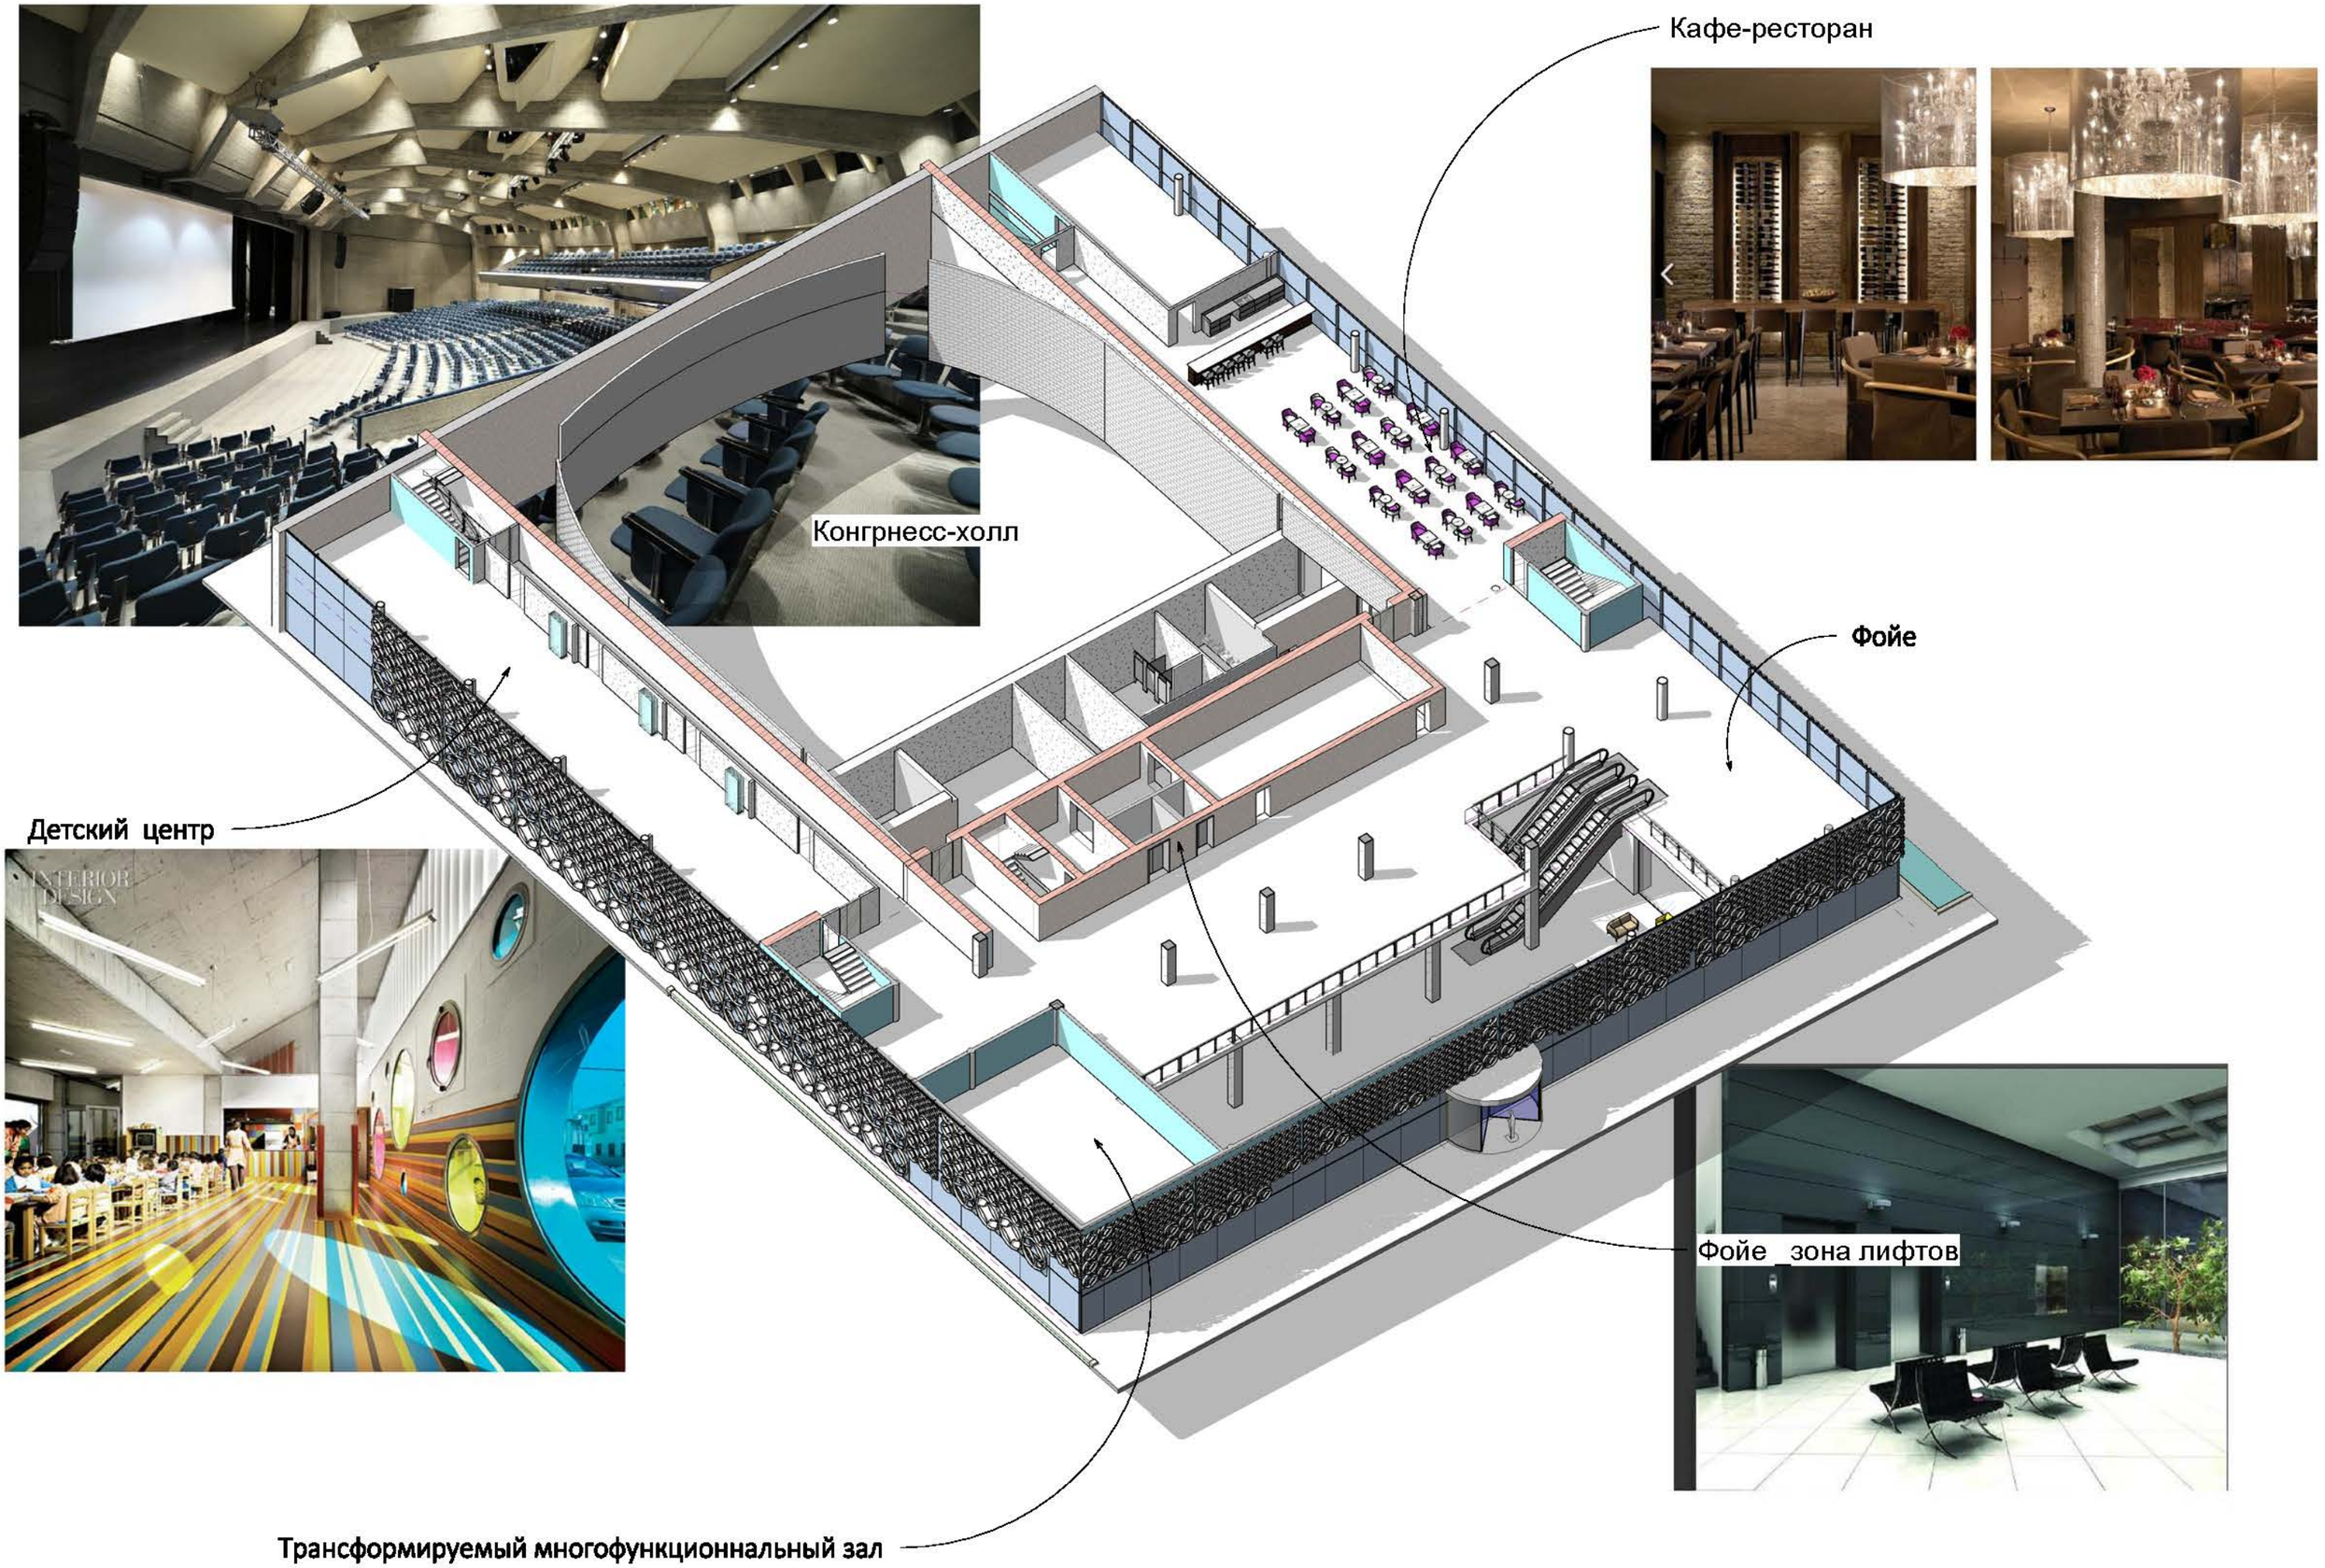
Кафе-ресторан
Конгрнесс-холл
Фойе
Детский центр
Фойе _зона лифтов
Трансформируемый многофункционнальный зал

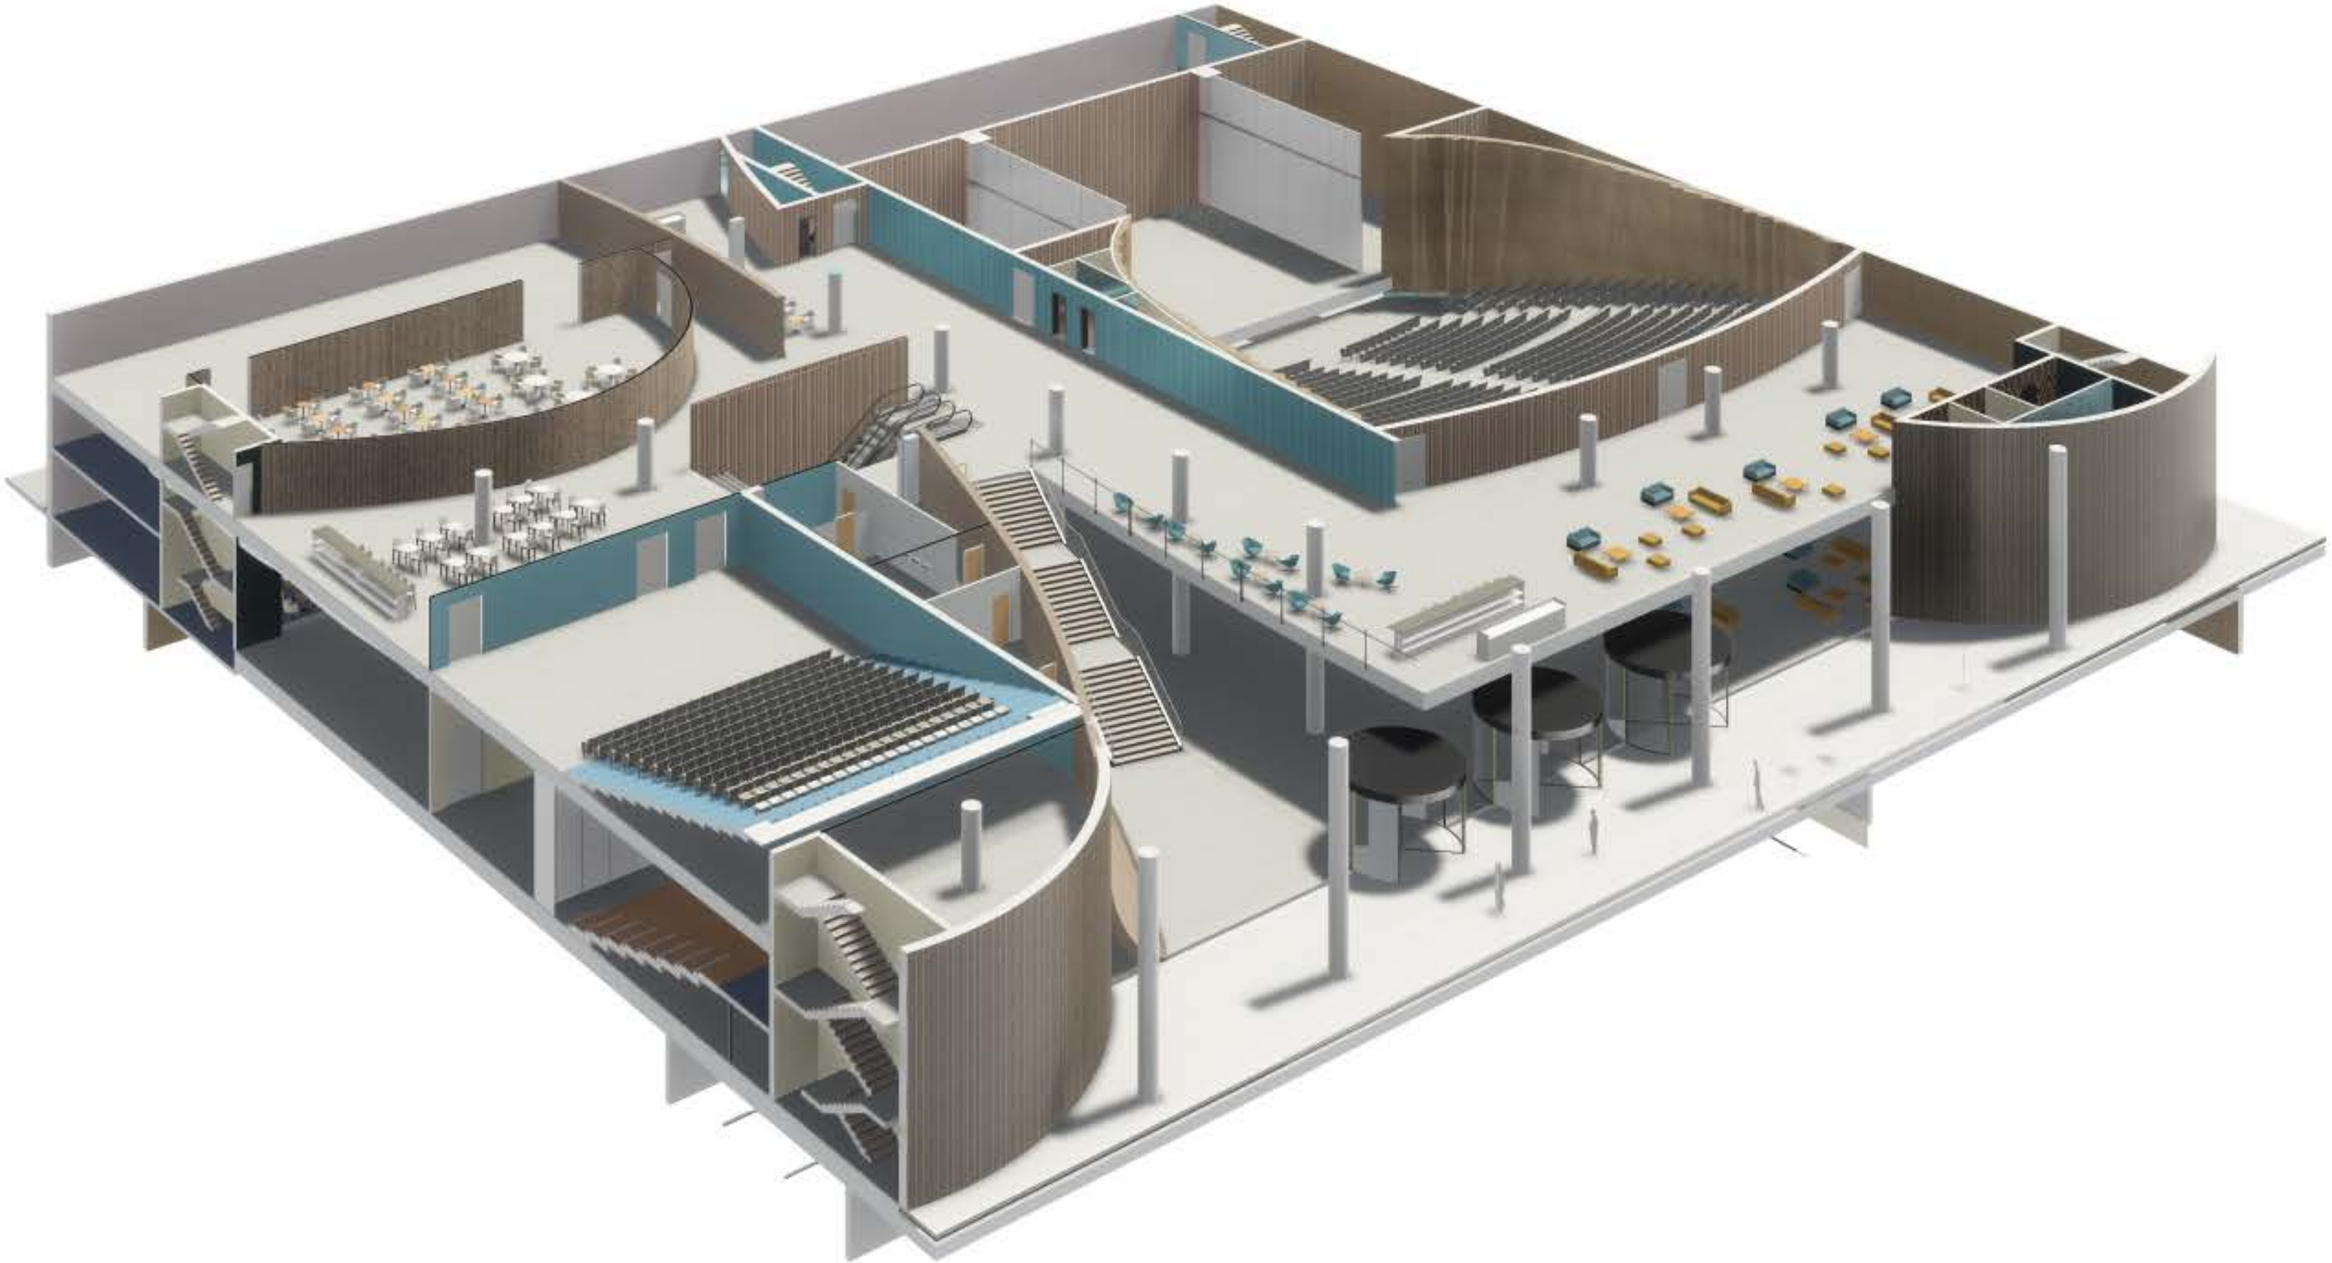

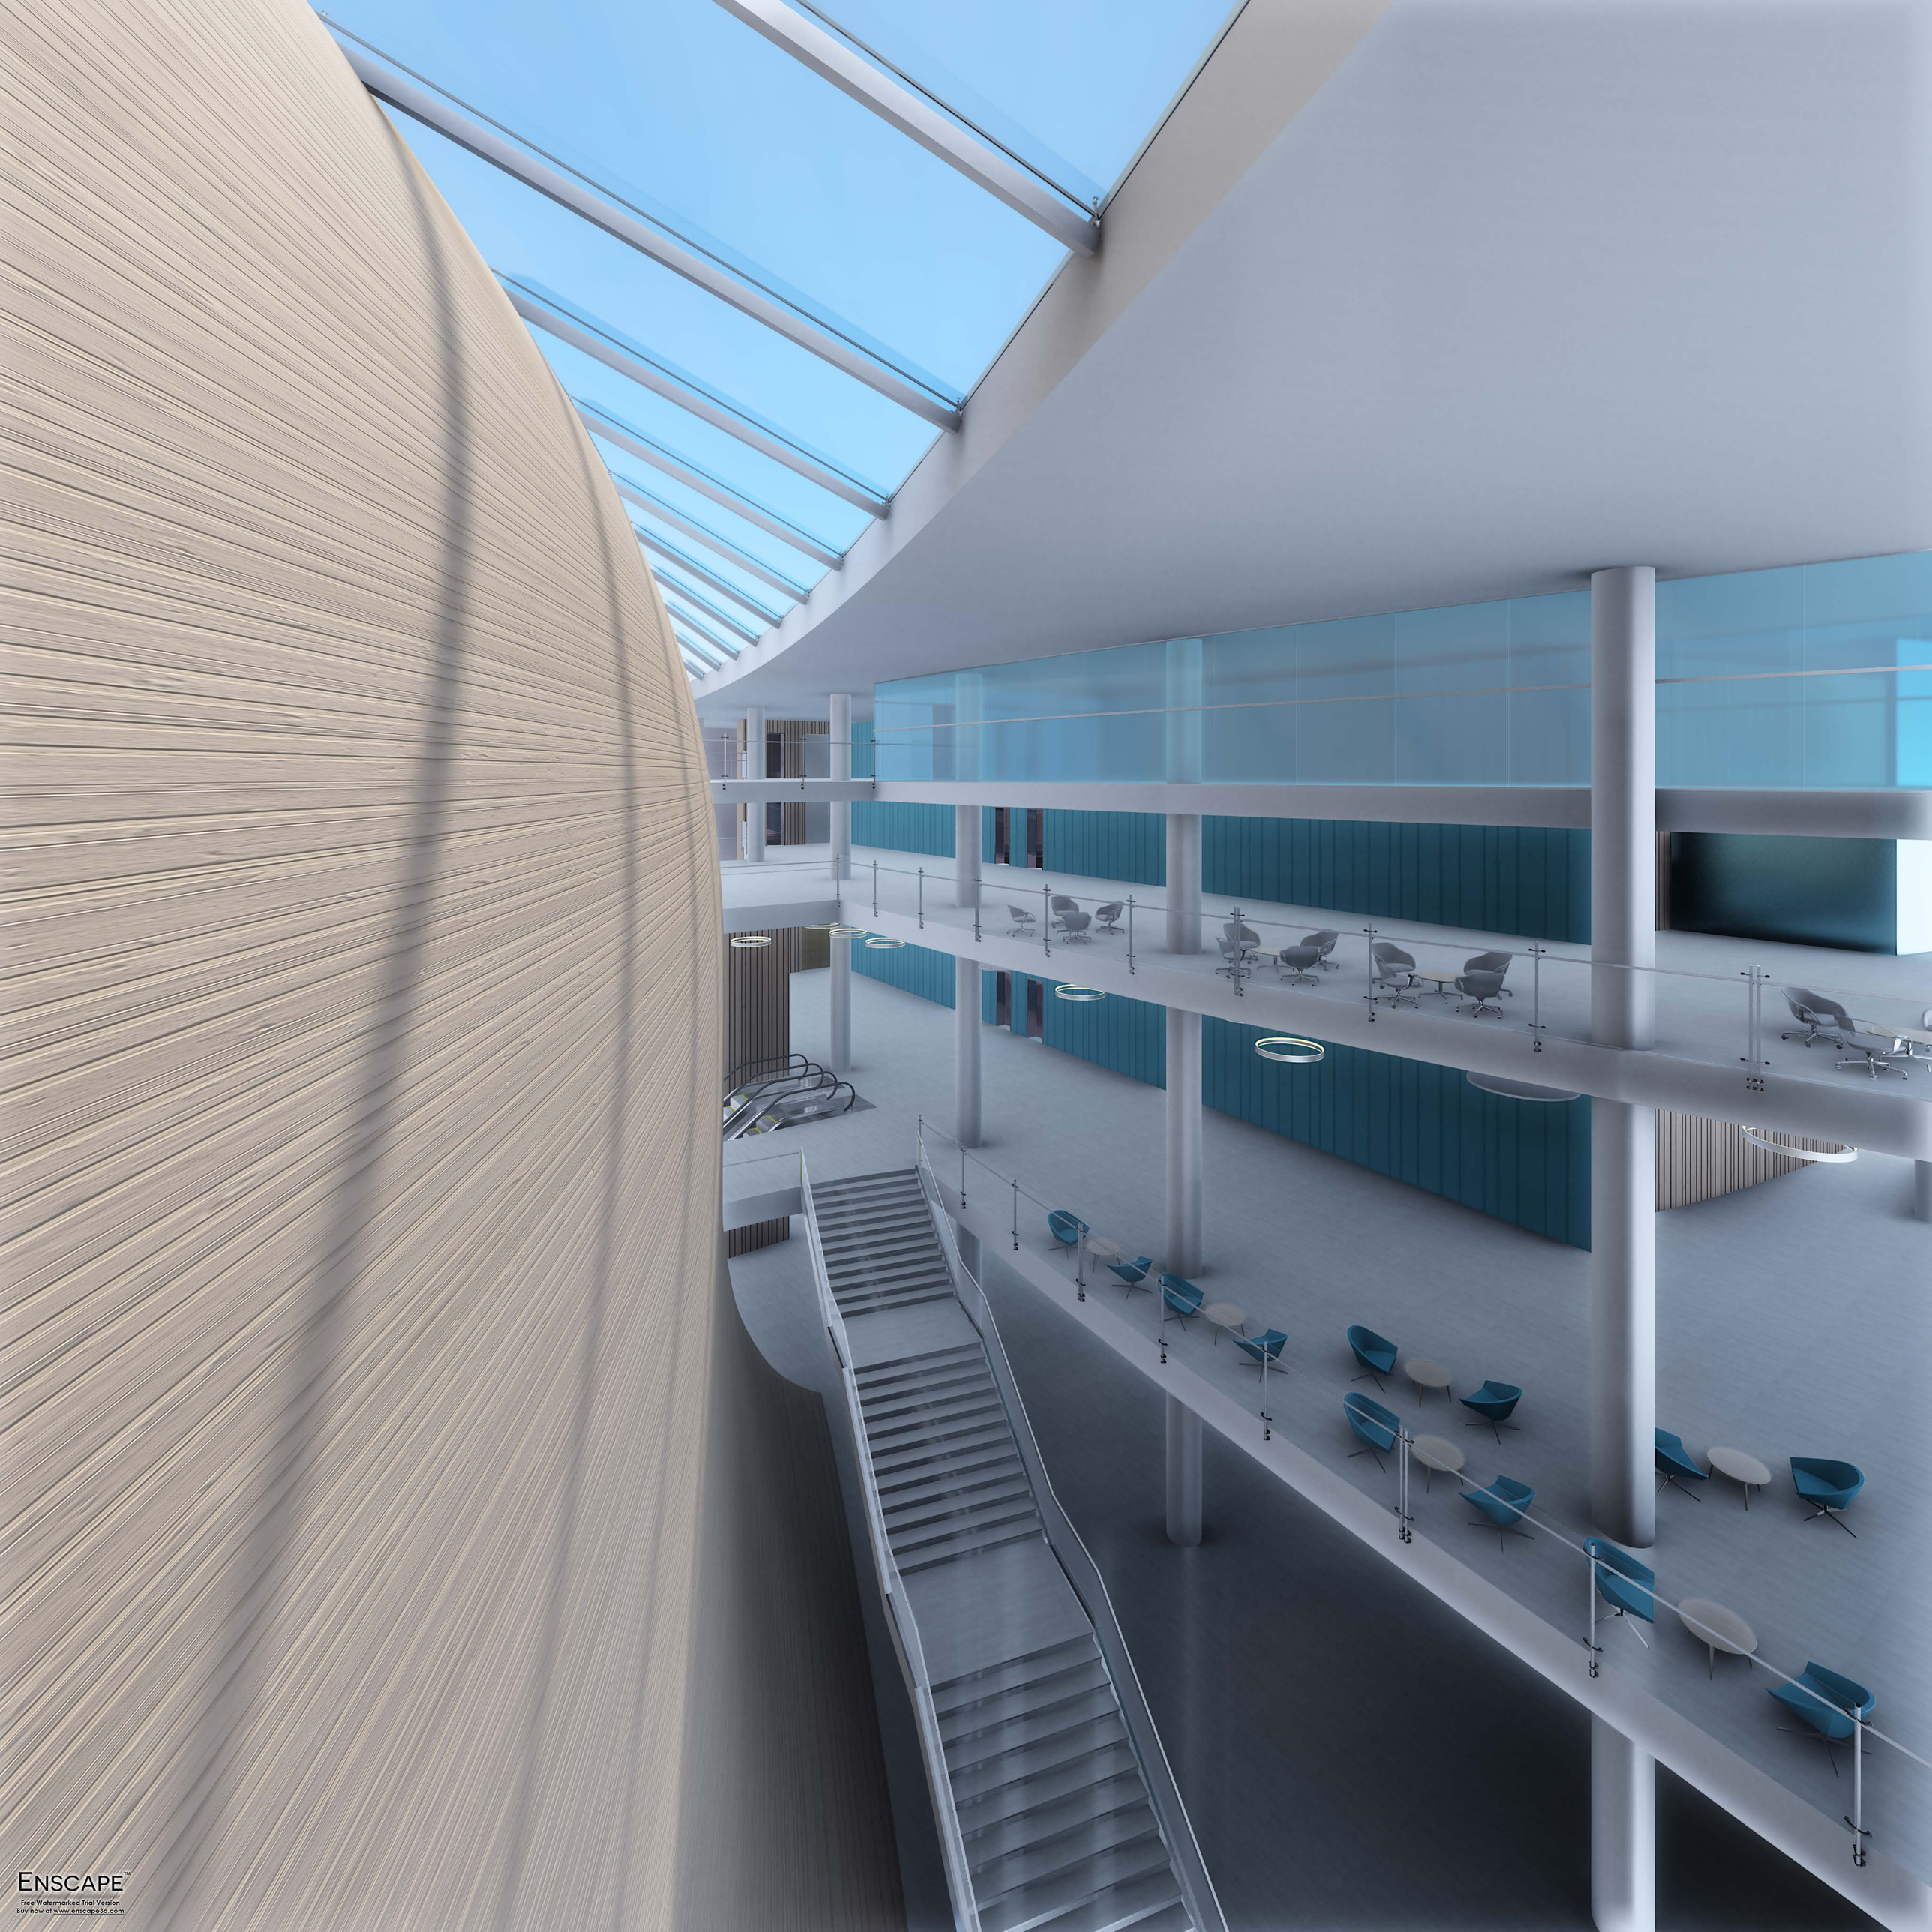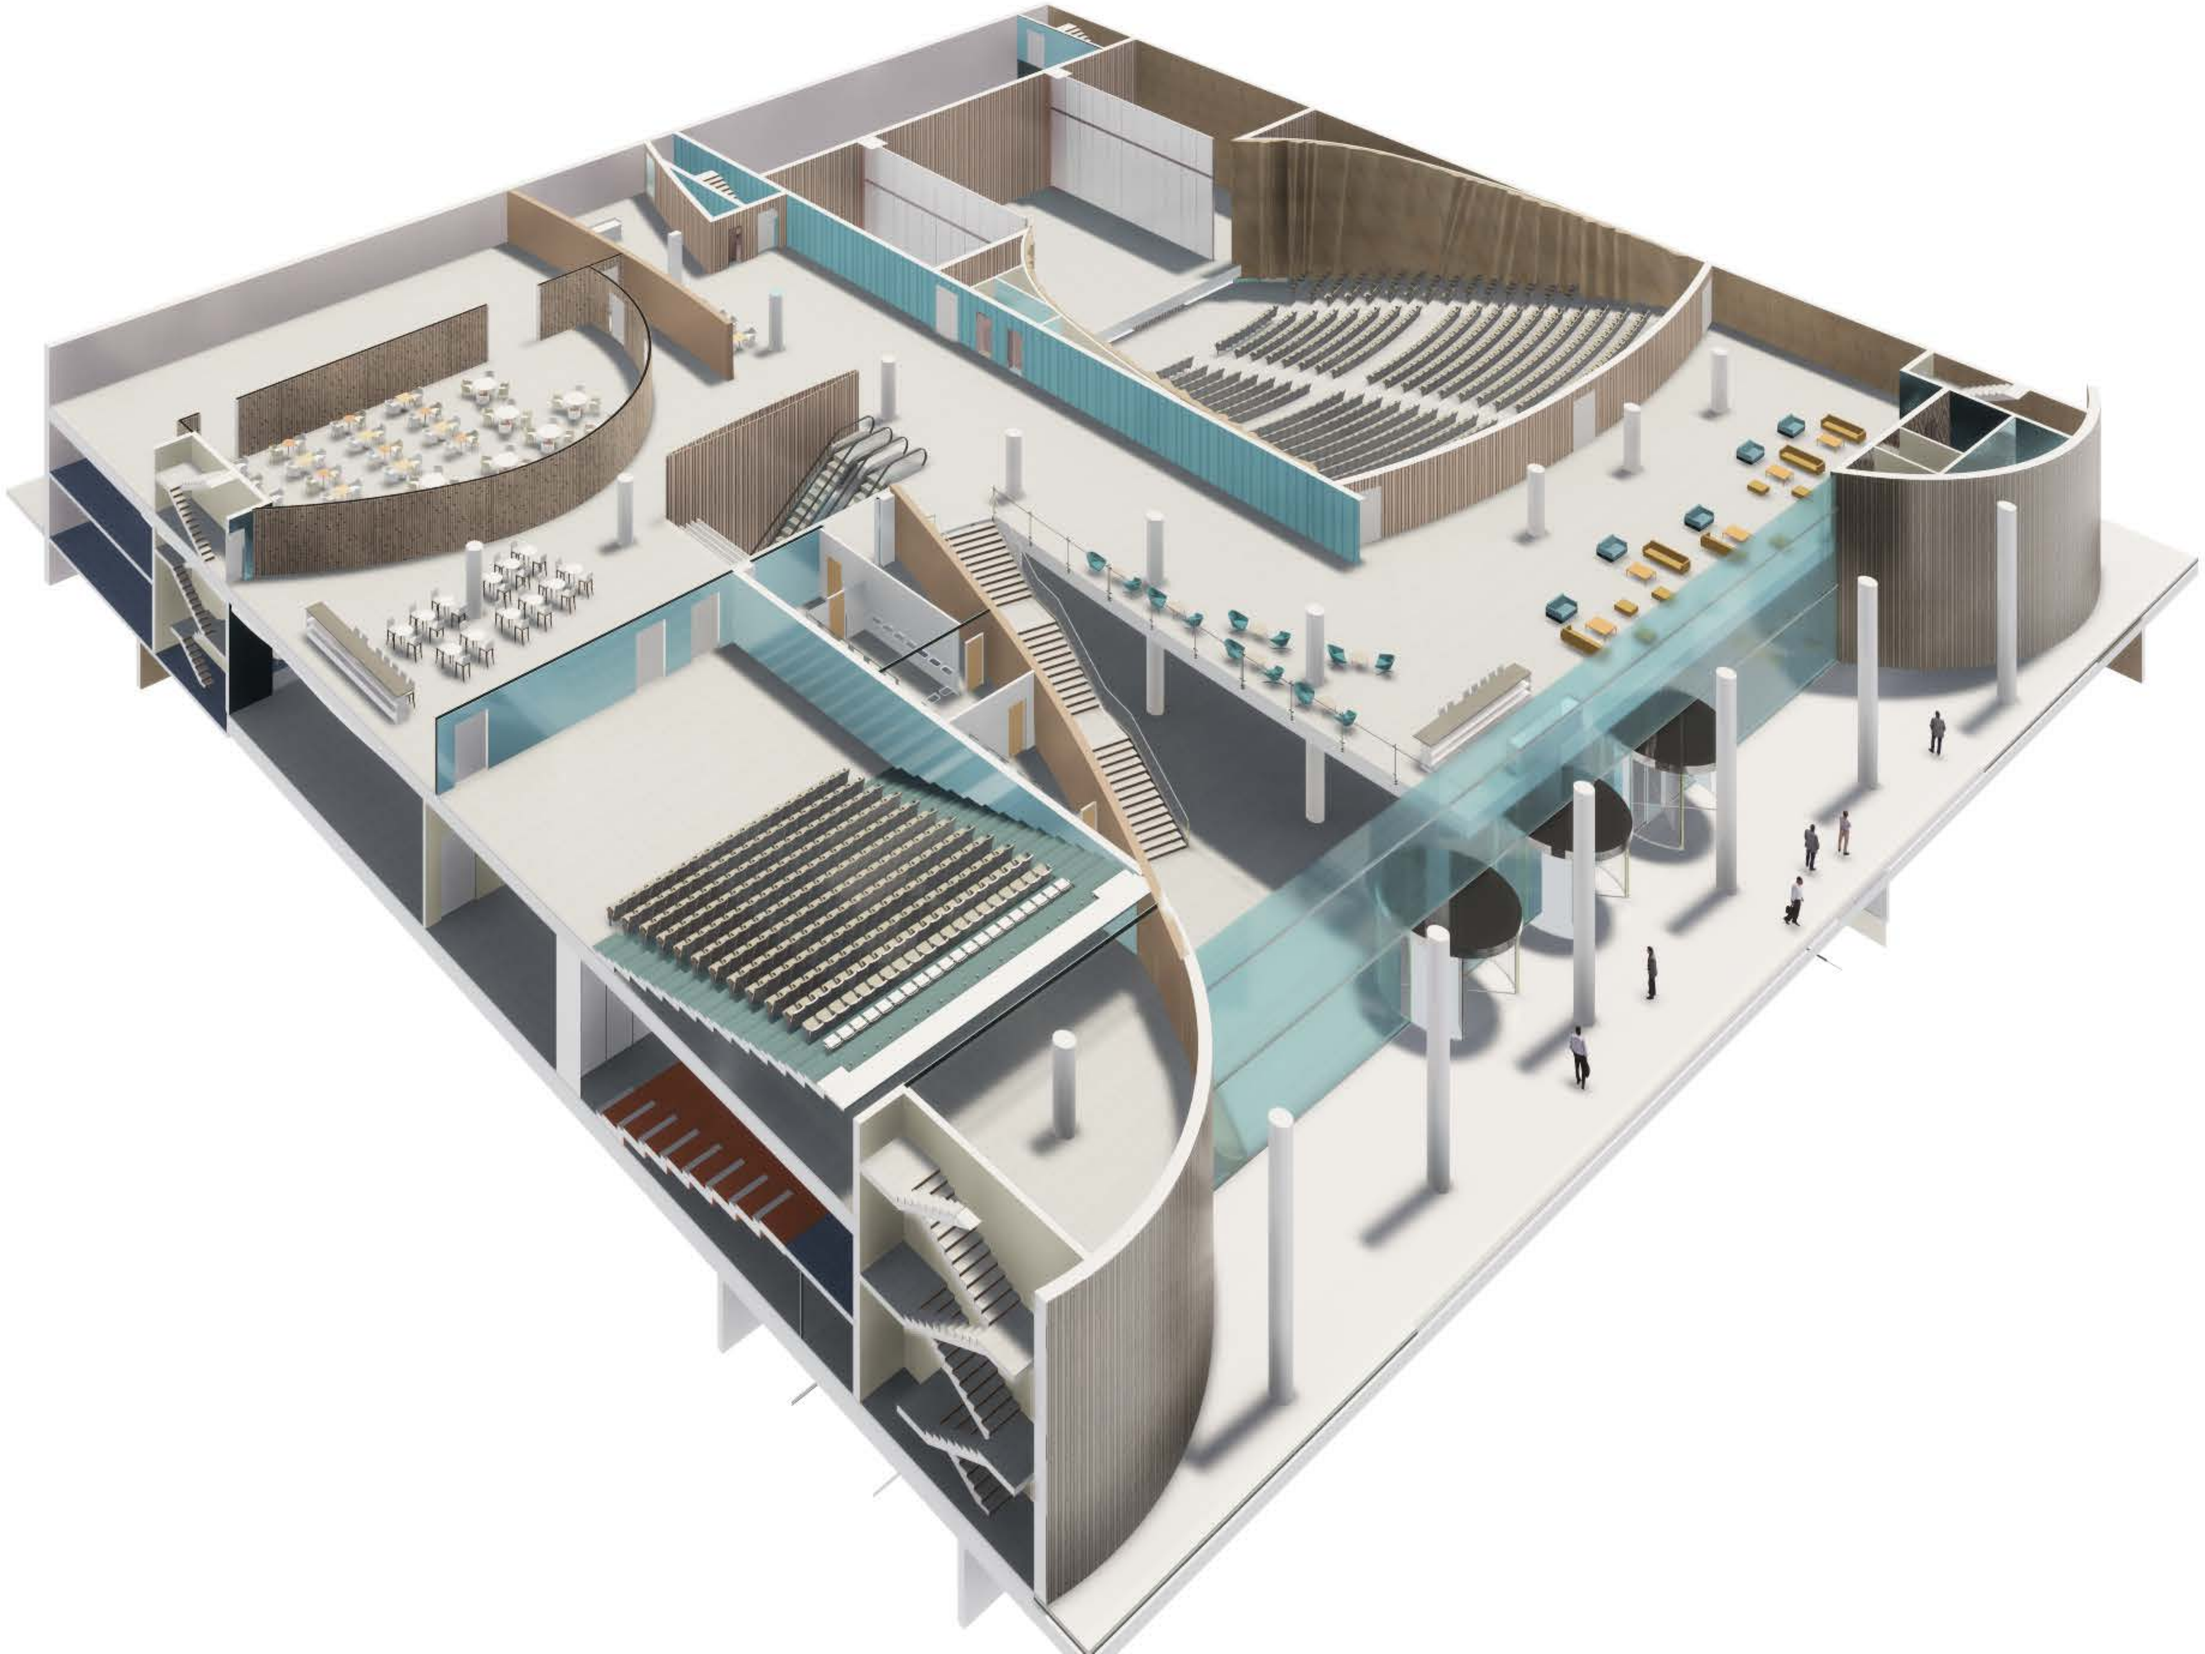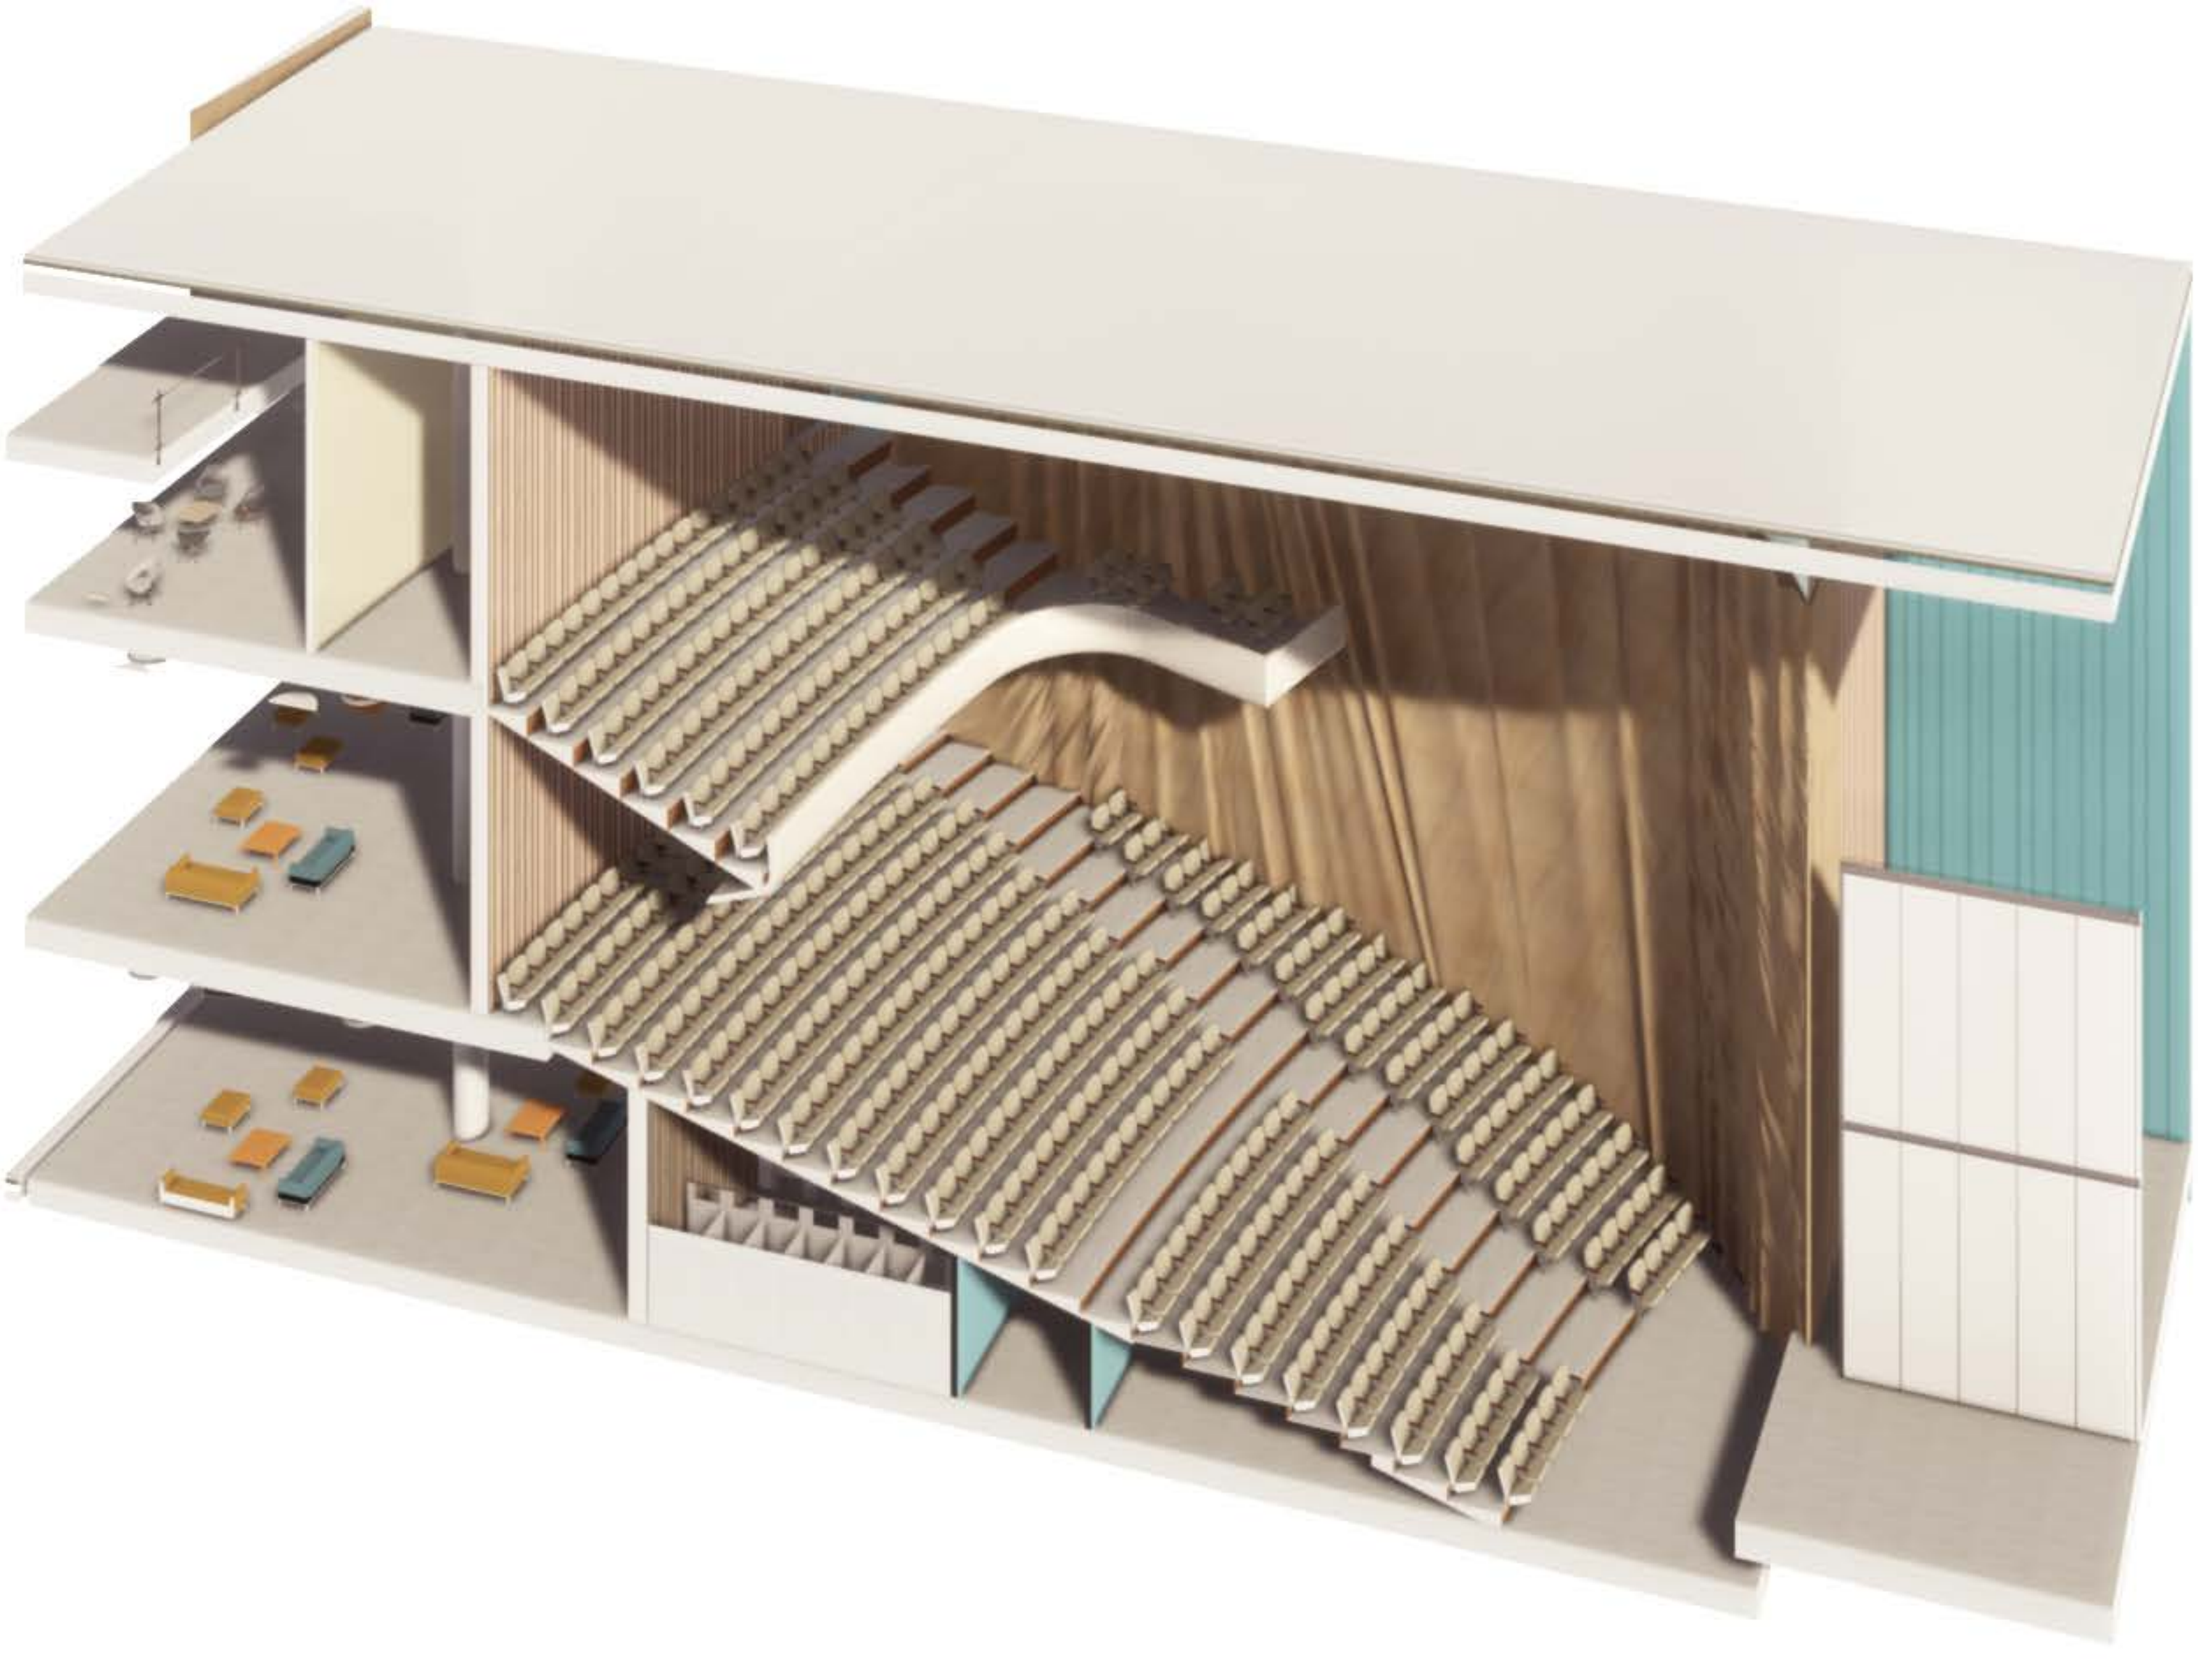
ENSCAPE™
Free Watermarked Trial Version
Buy now at www.enscape3d.com