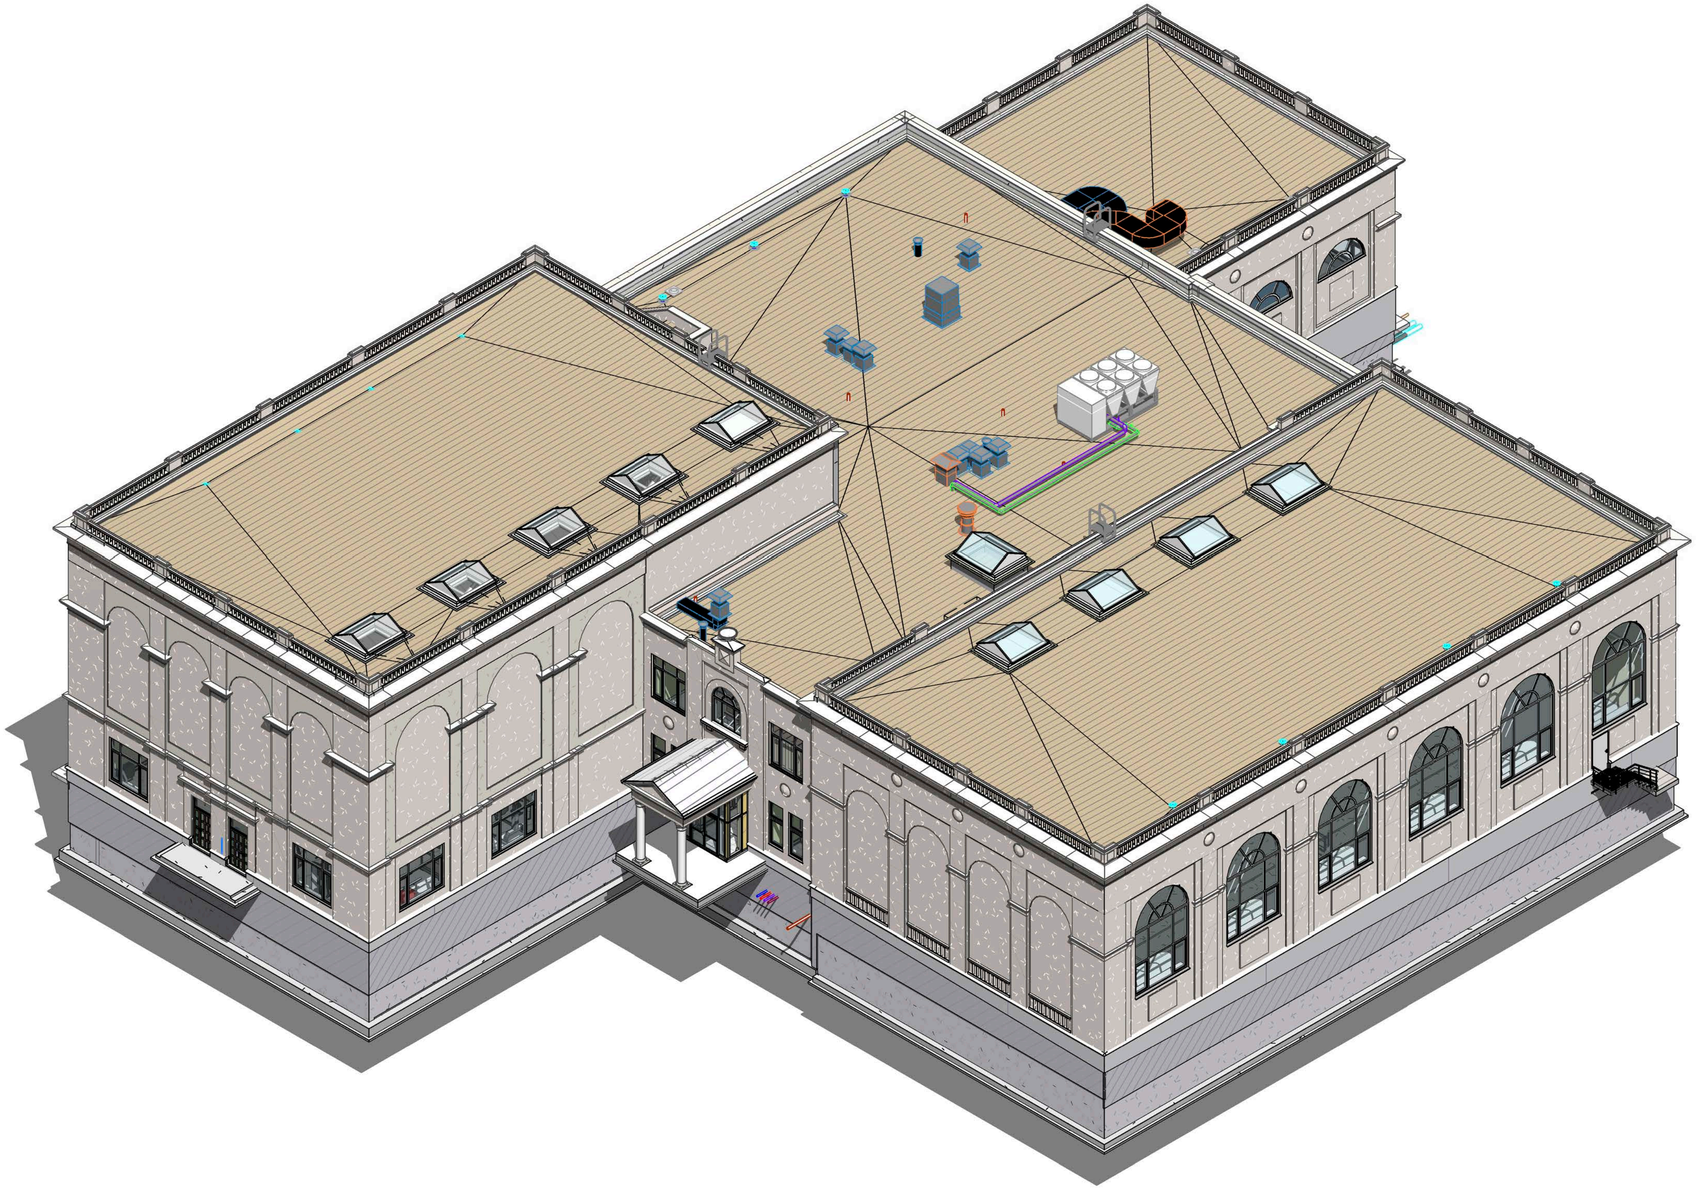

NO.
PTS
F
HOME
GUEST
PERIOD
BONUS
BONUS
FOULS
PLAYER
FOULS
T.O.L.
T.O.L.

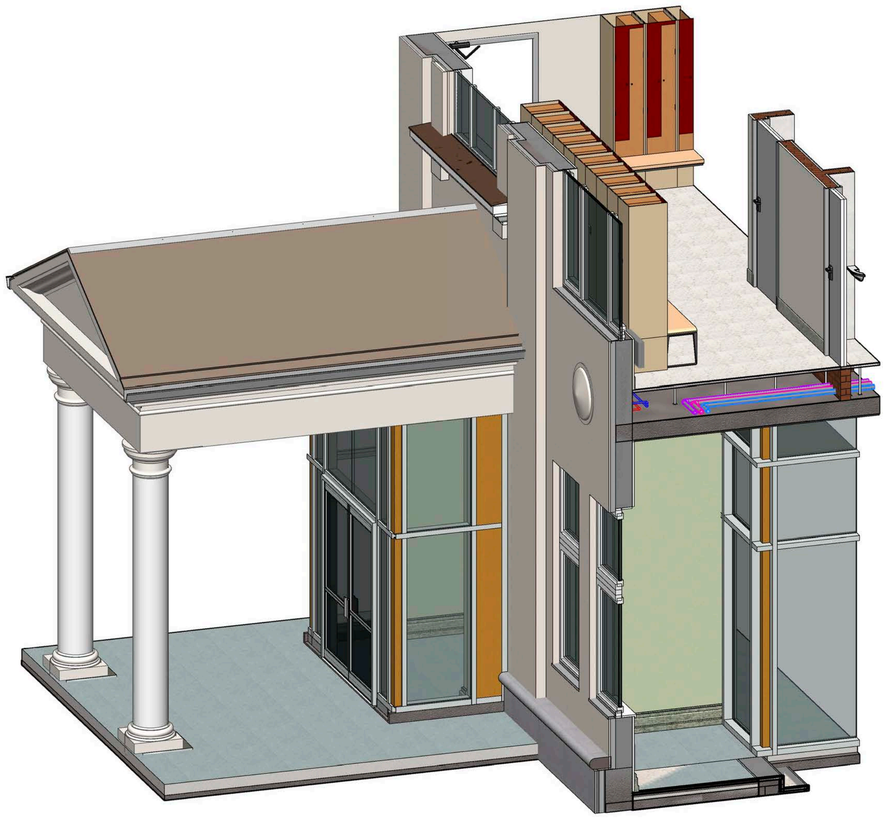

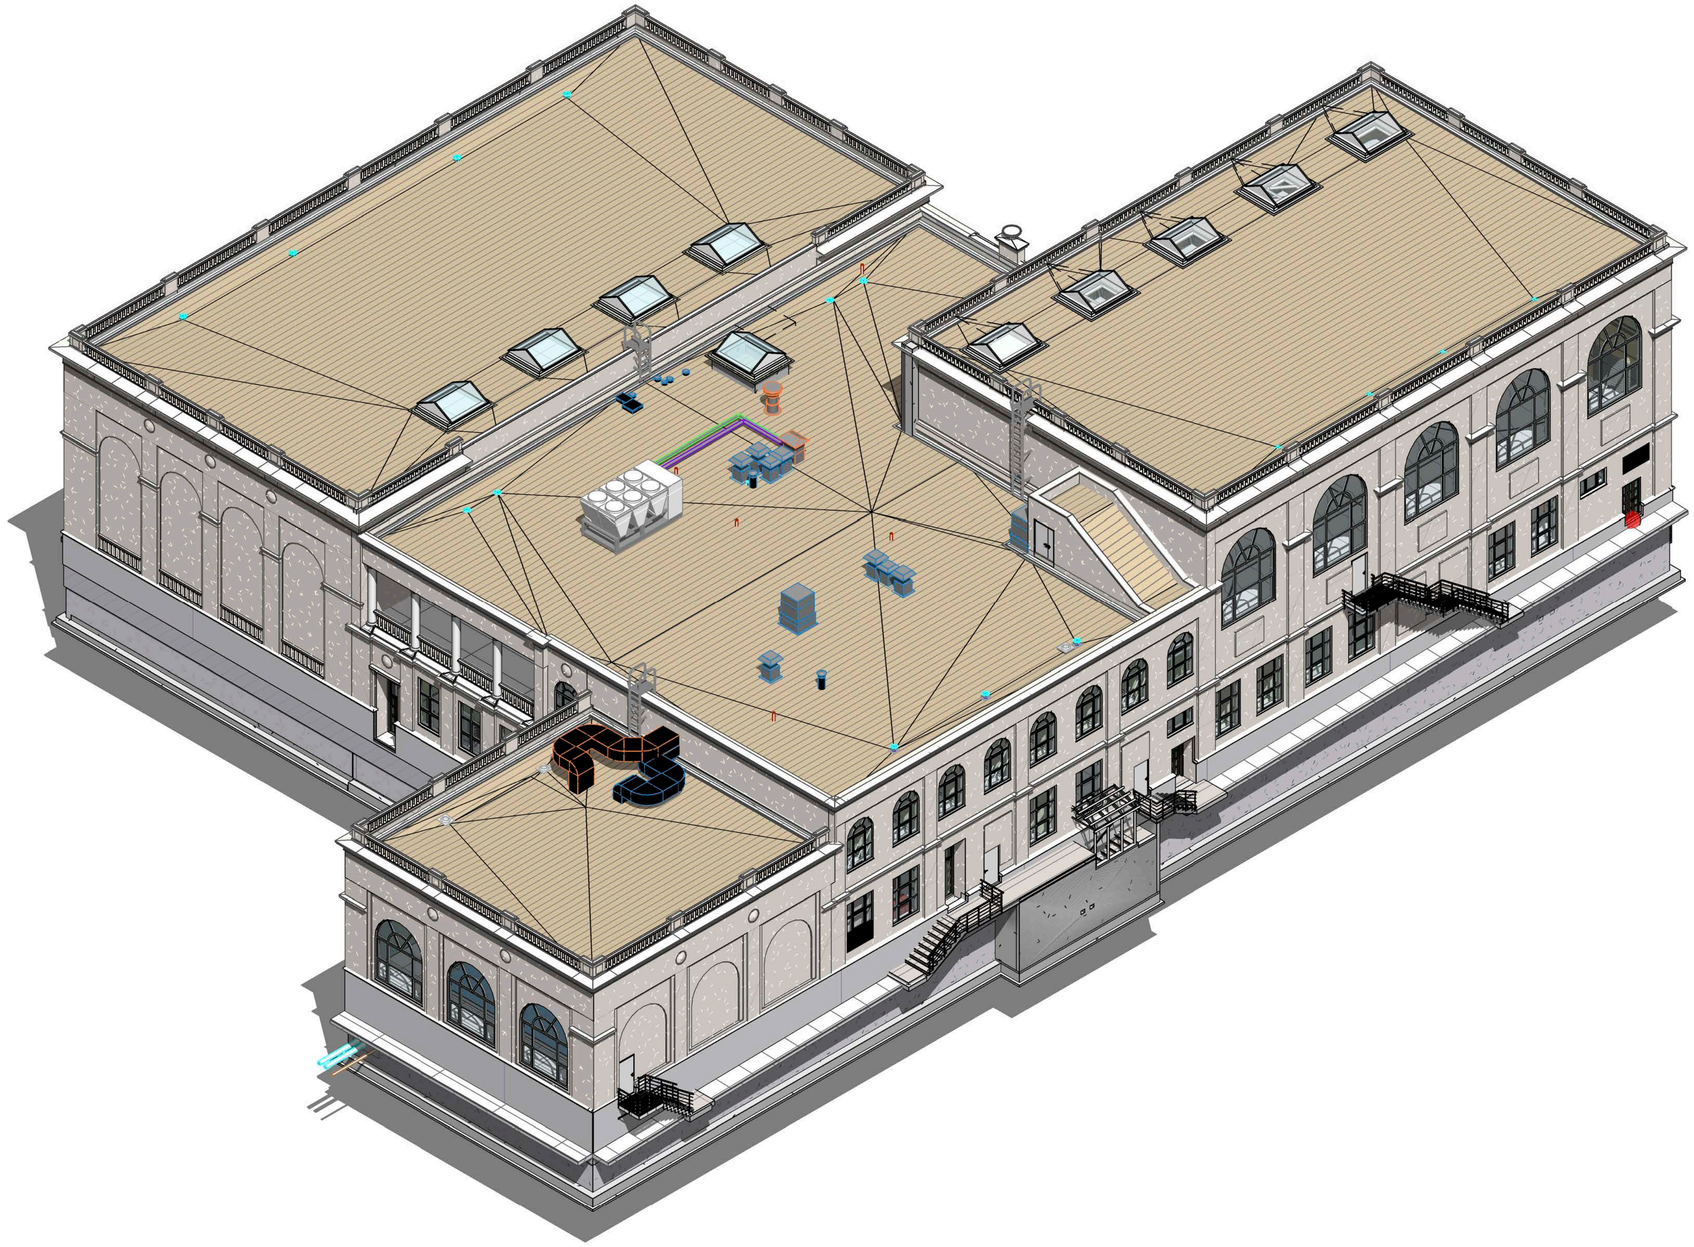

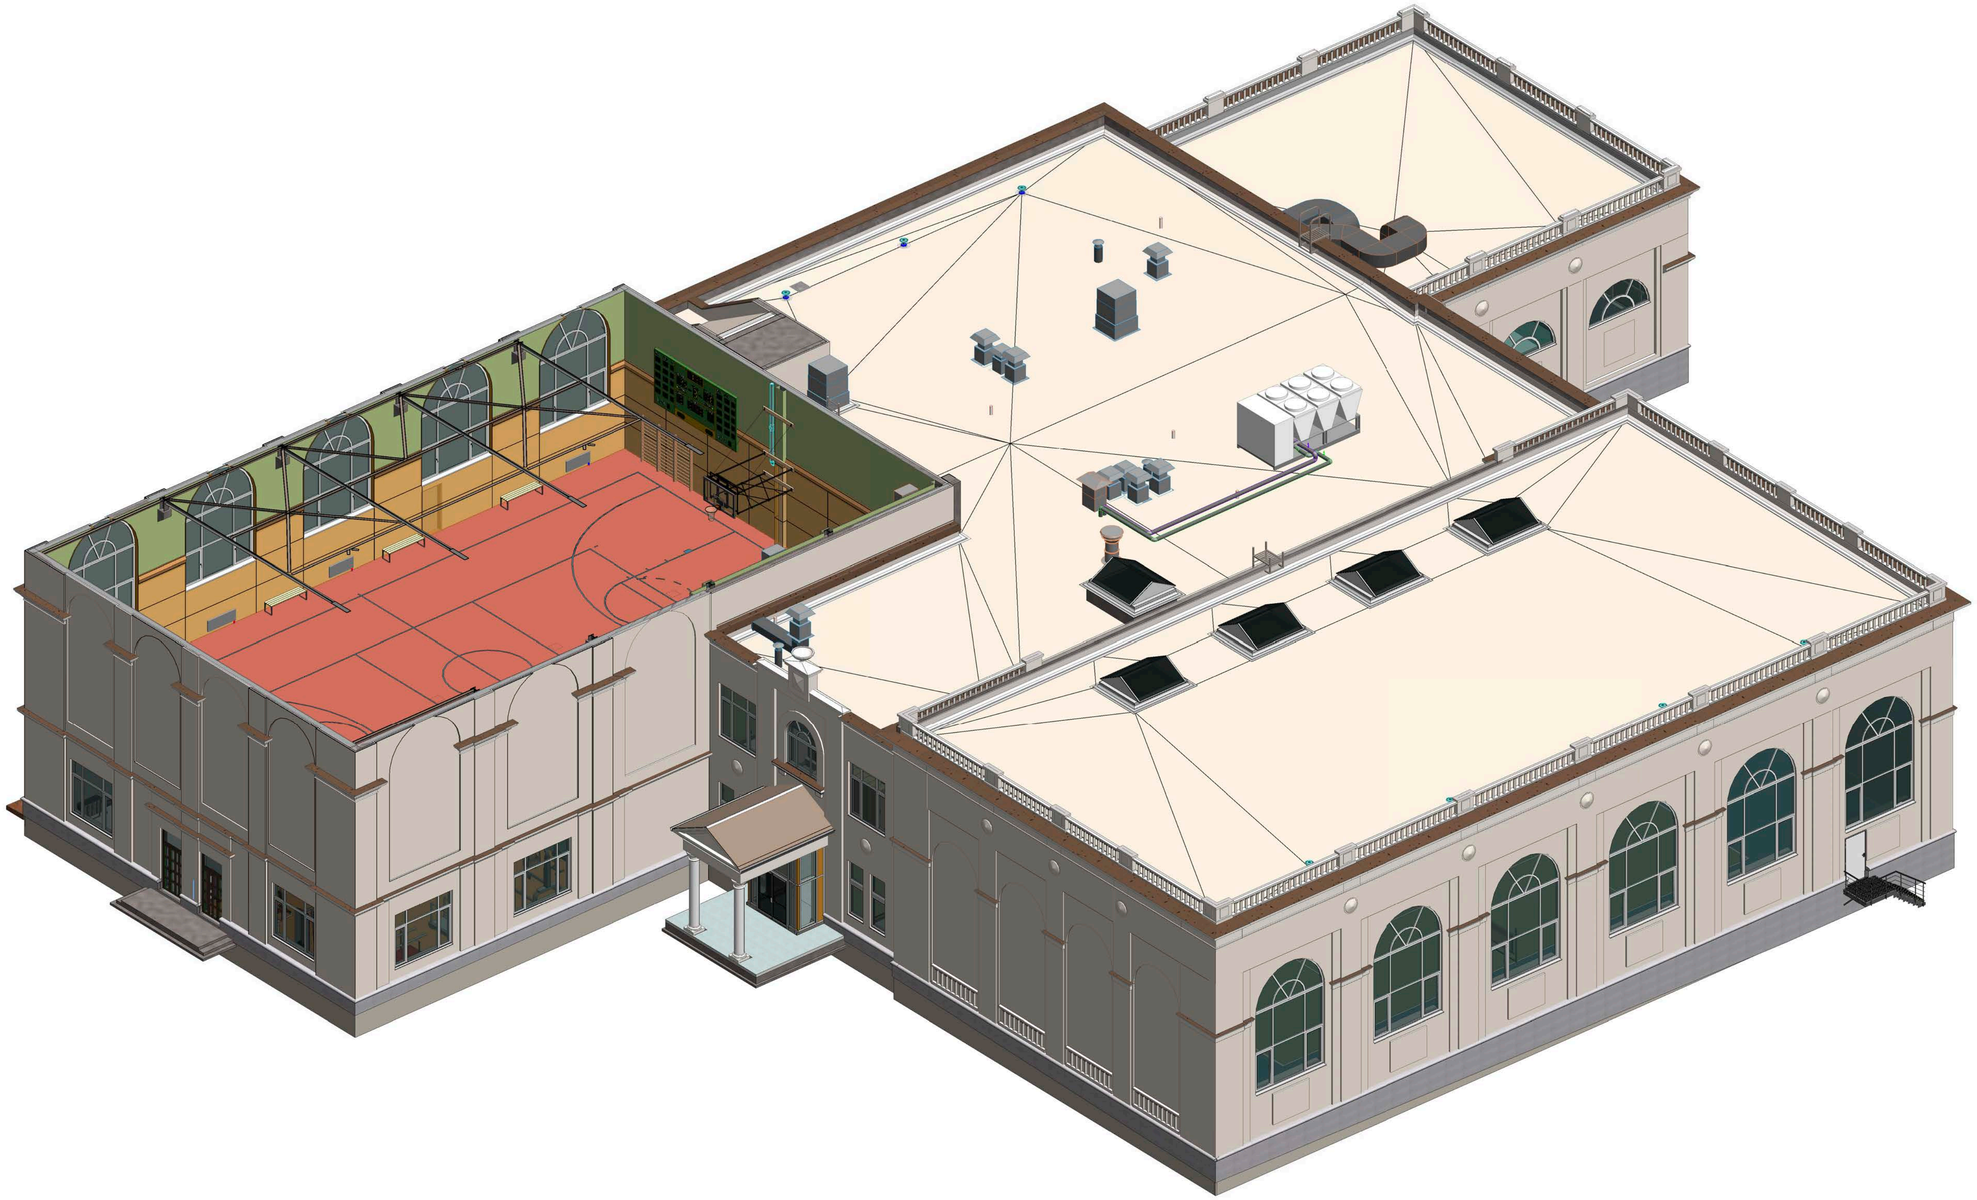

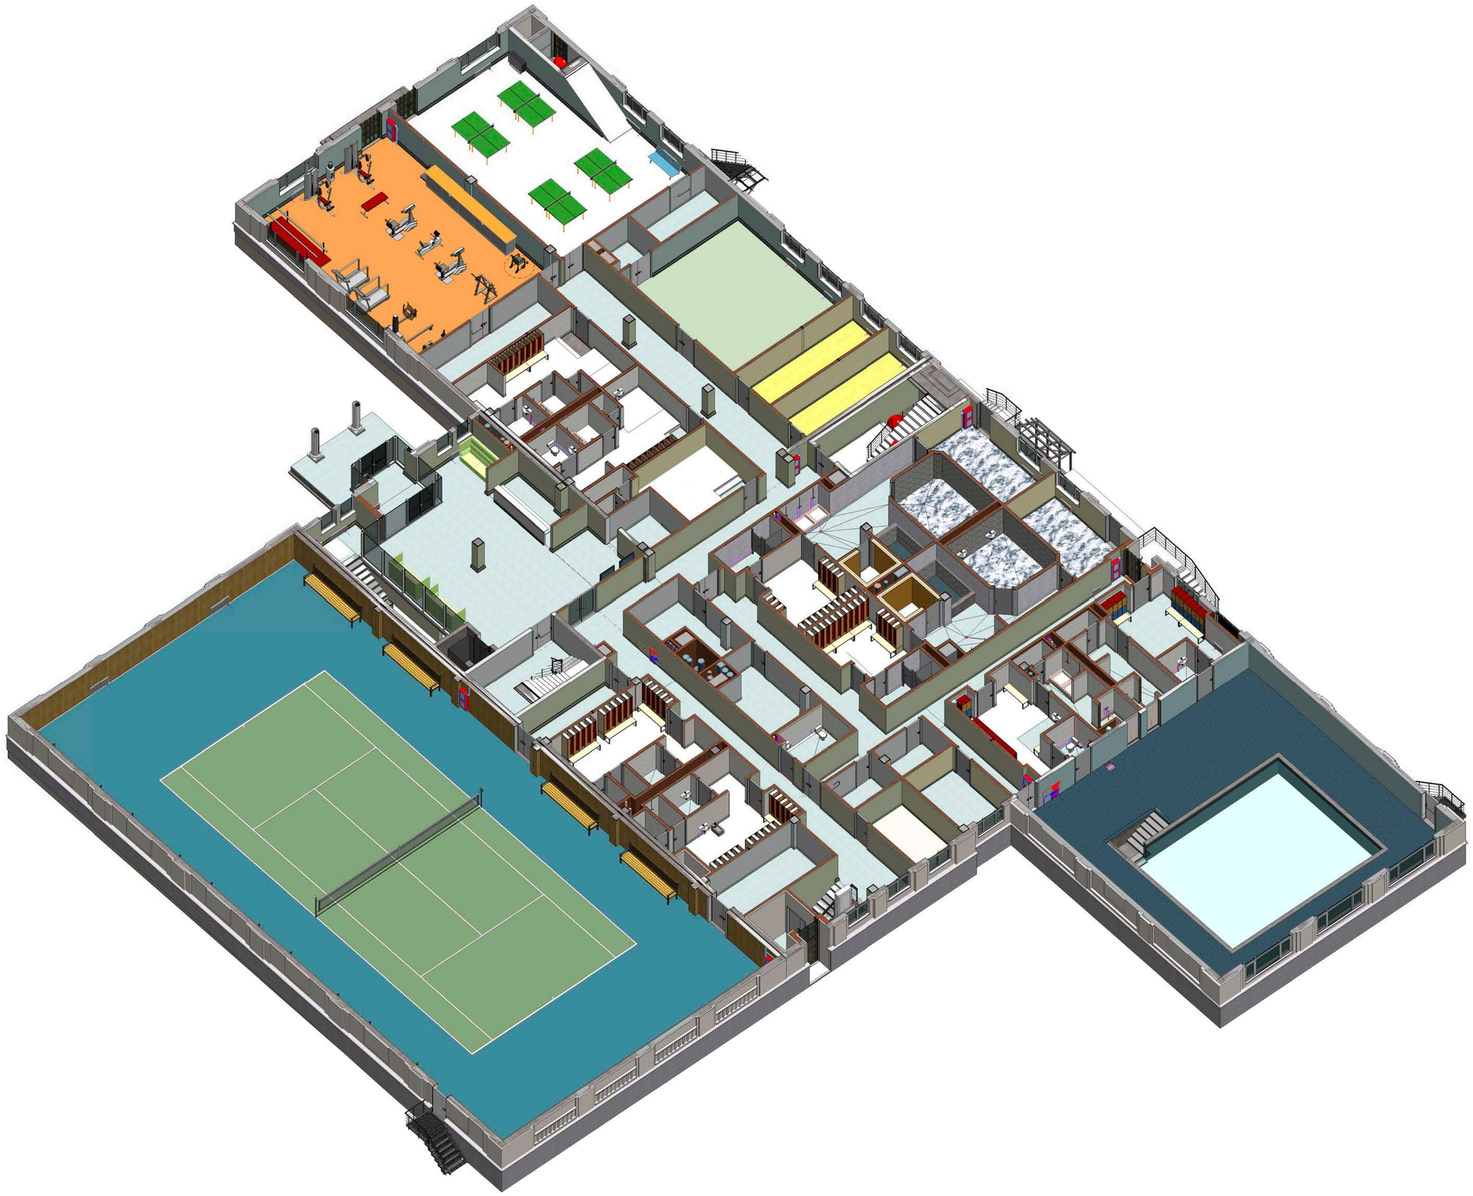

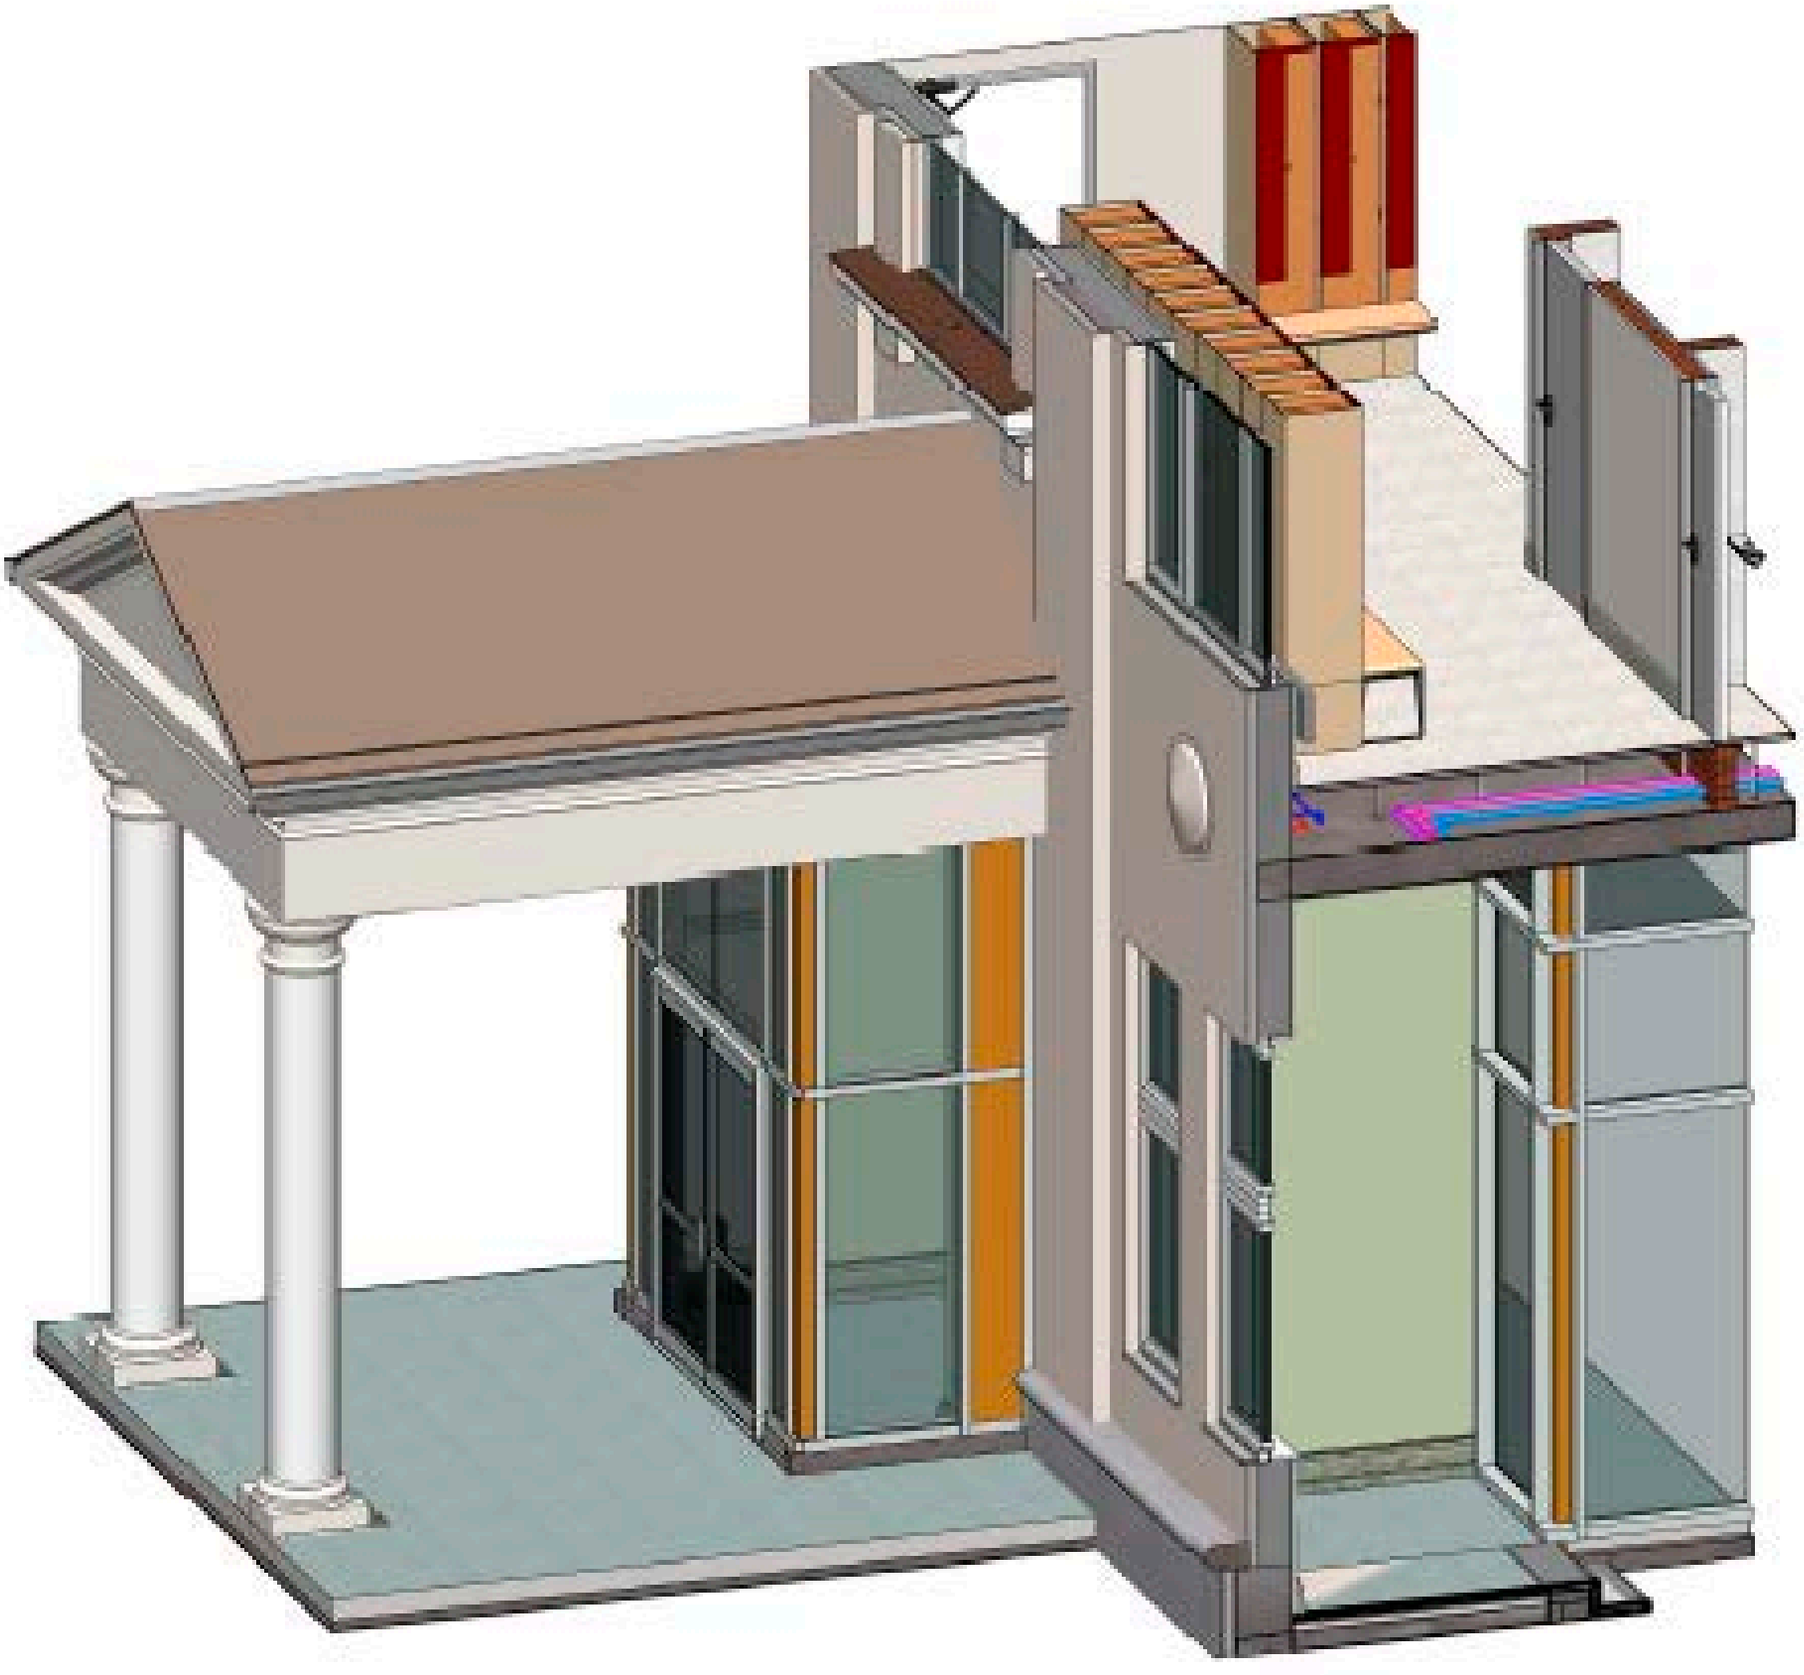

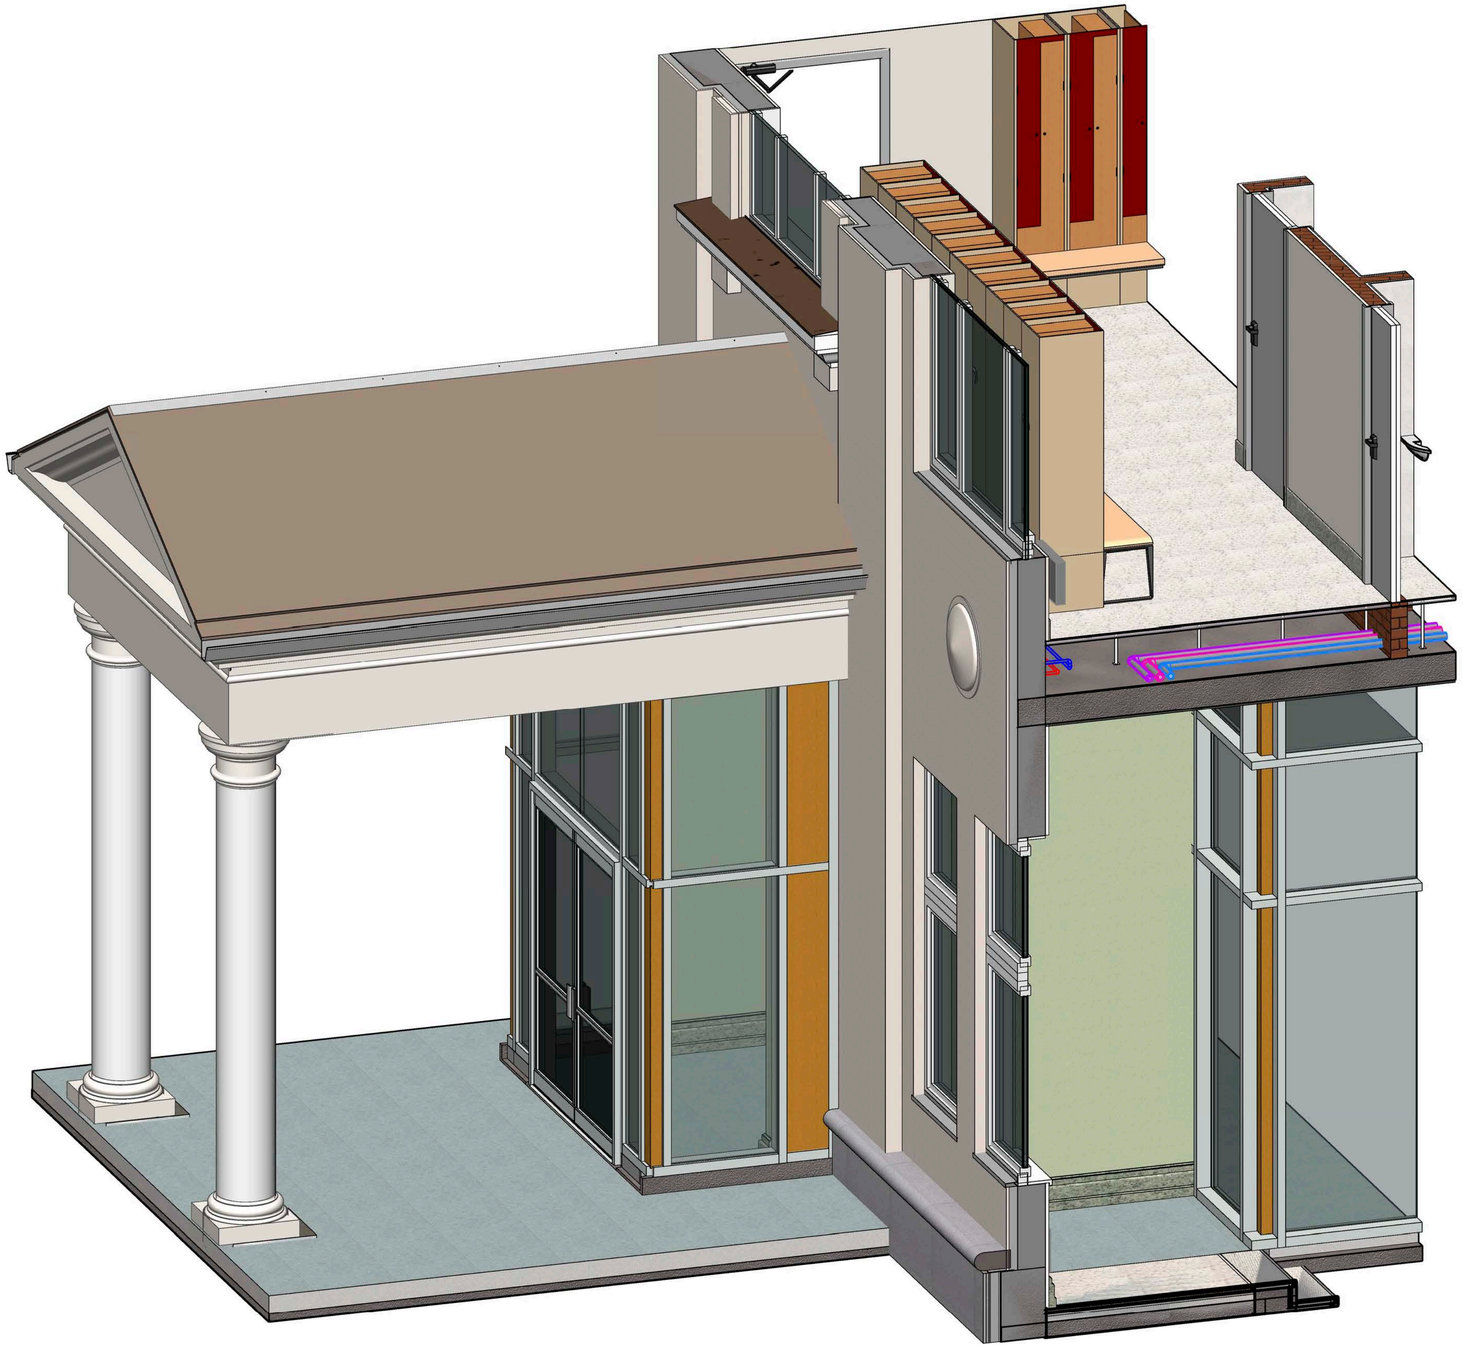

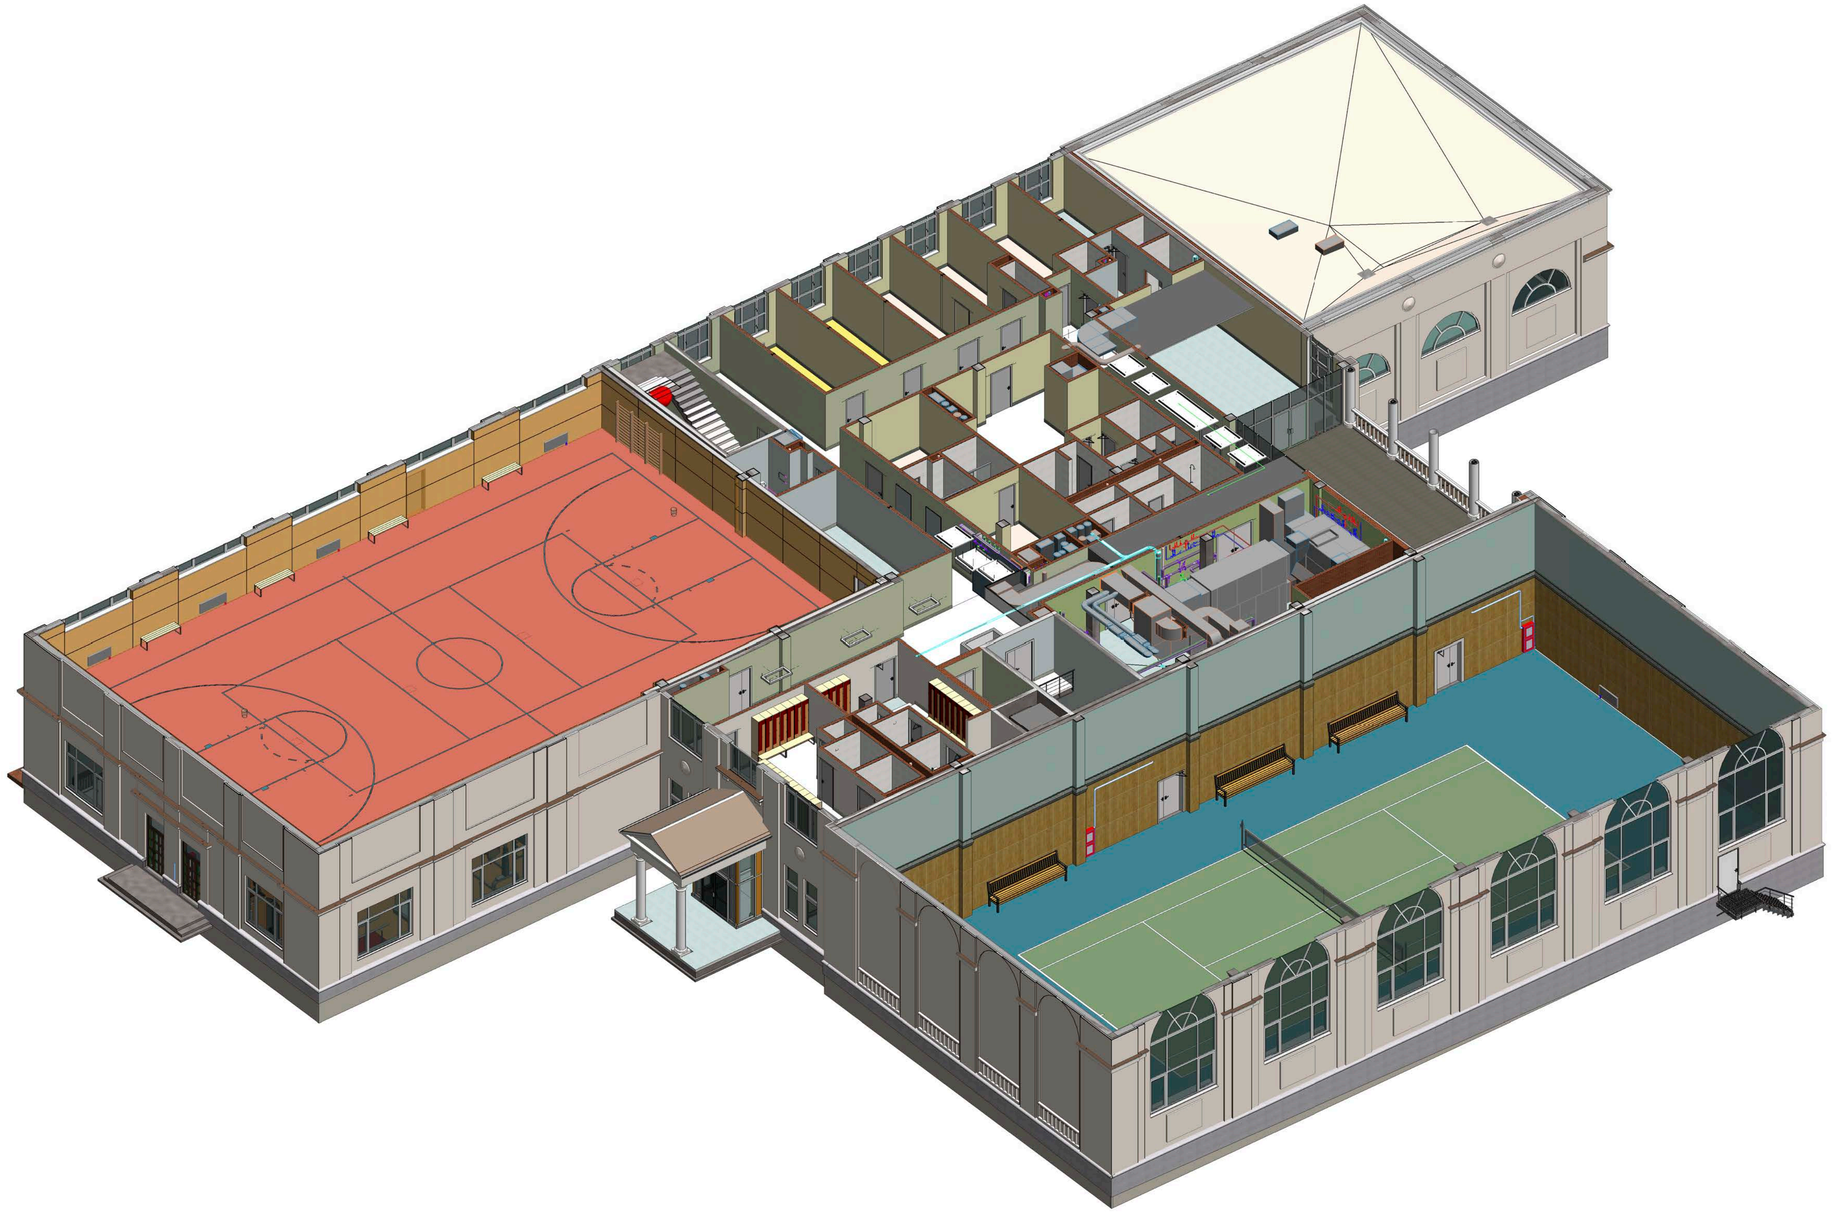

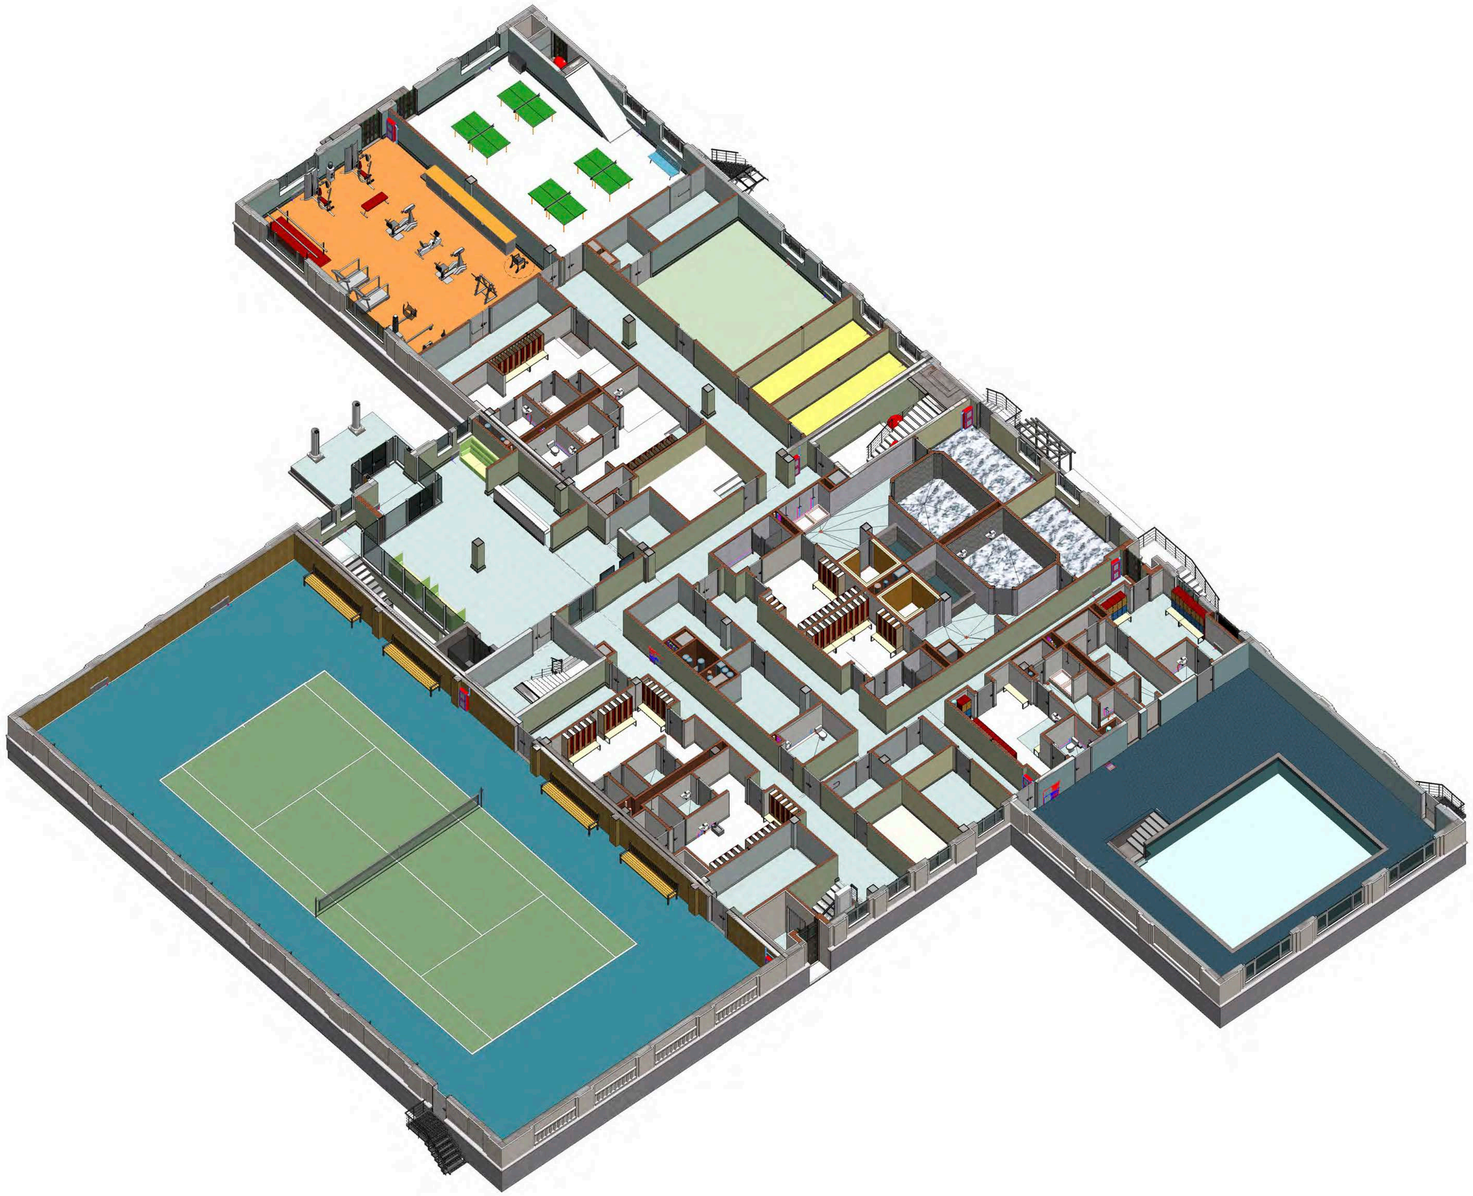

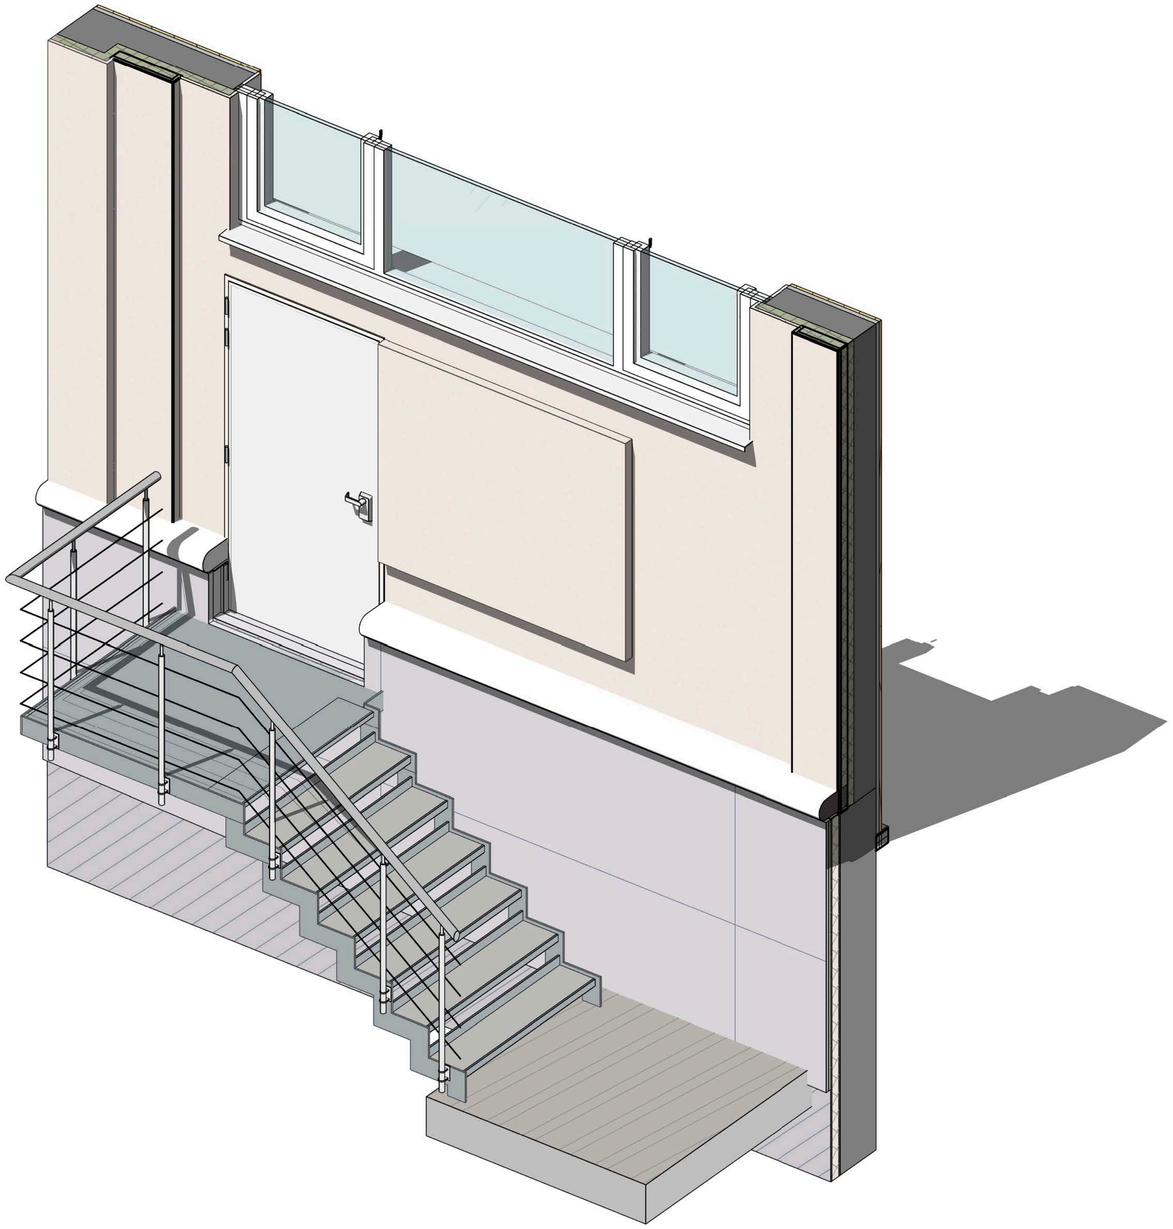

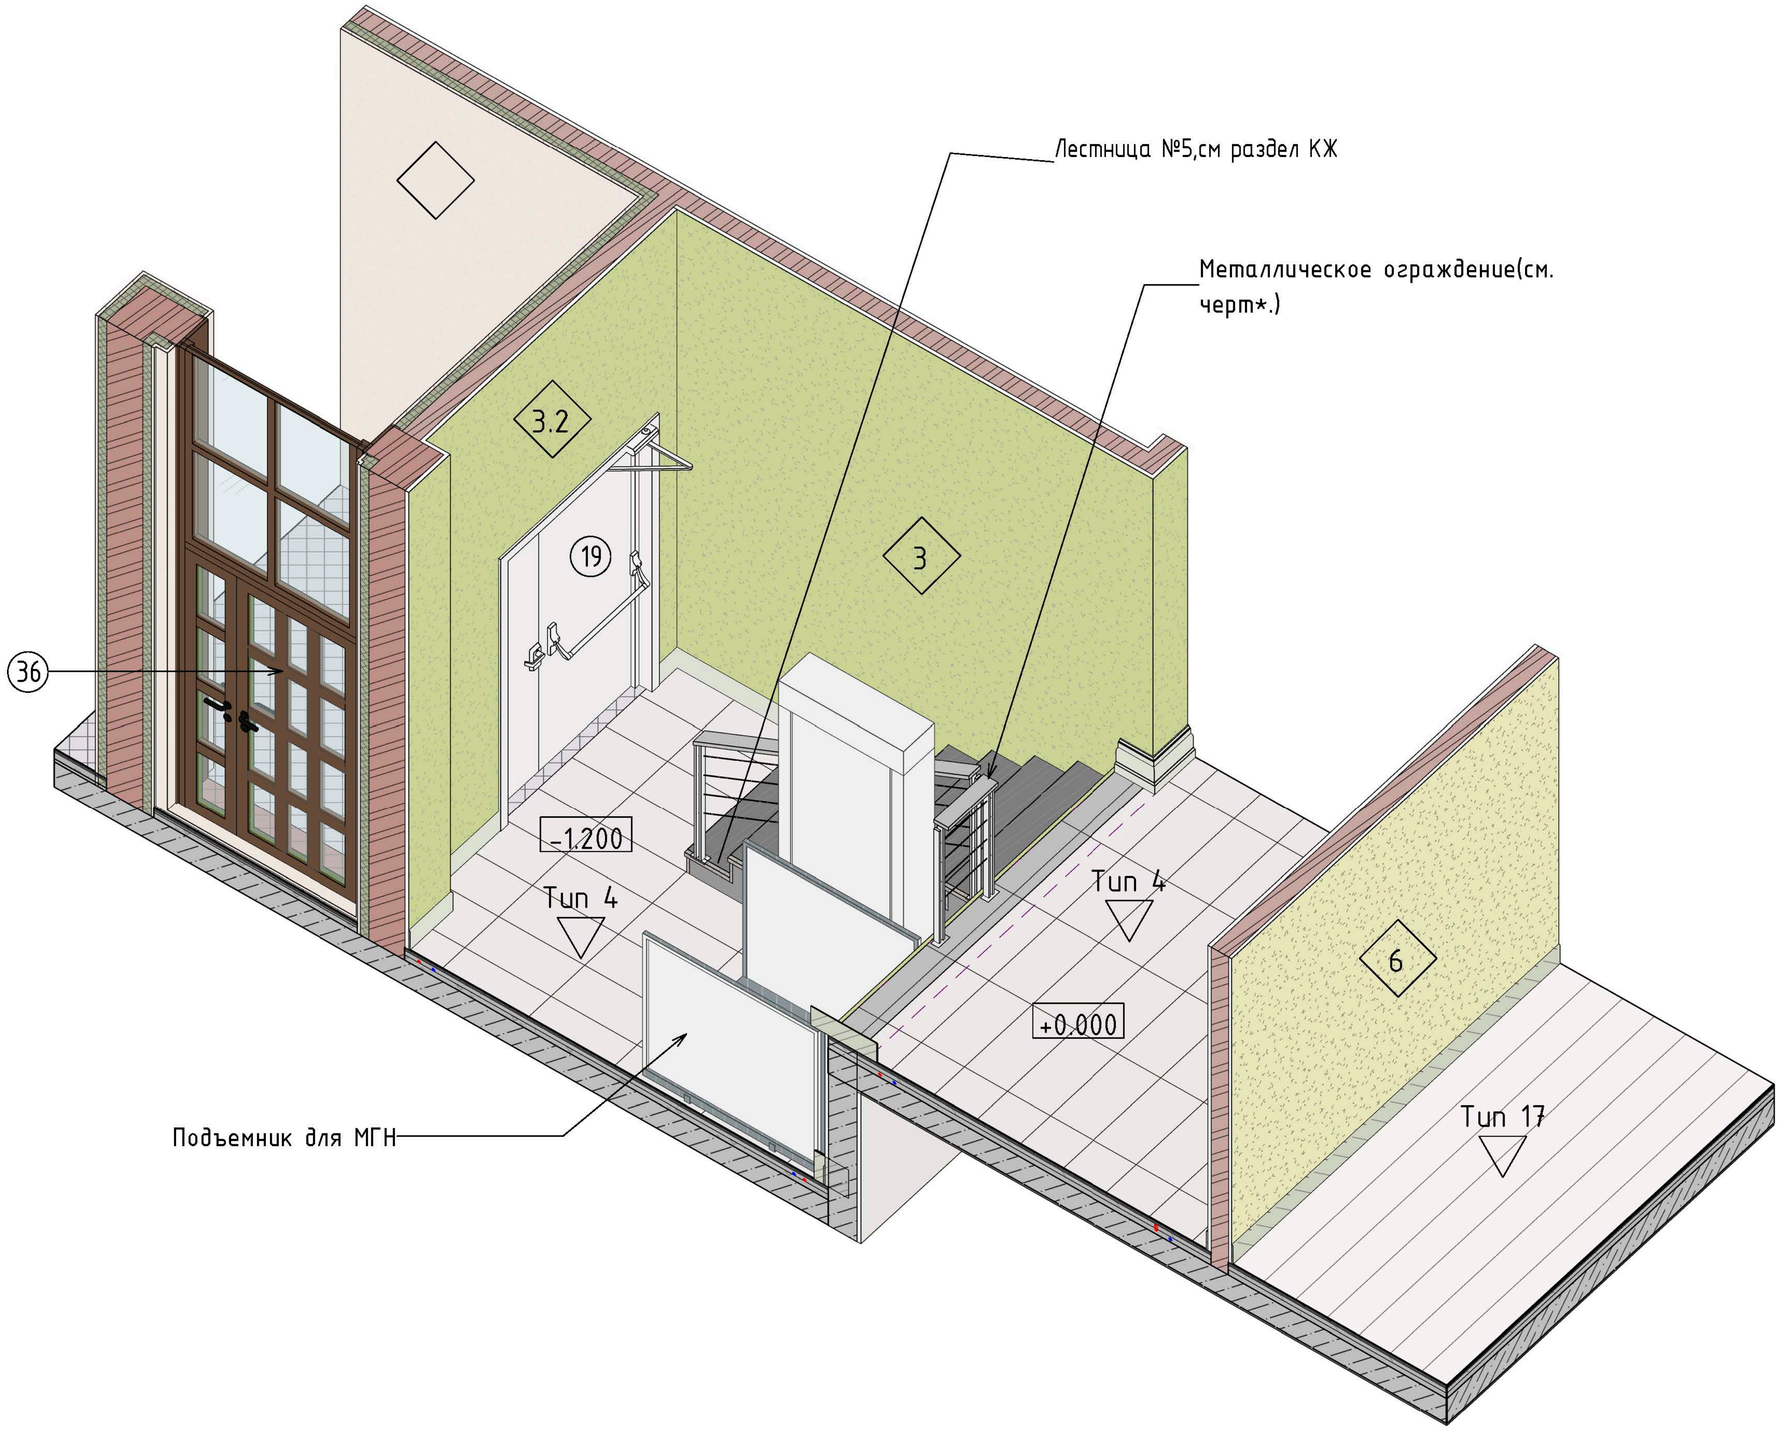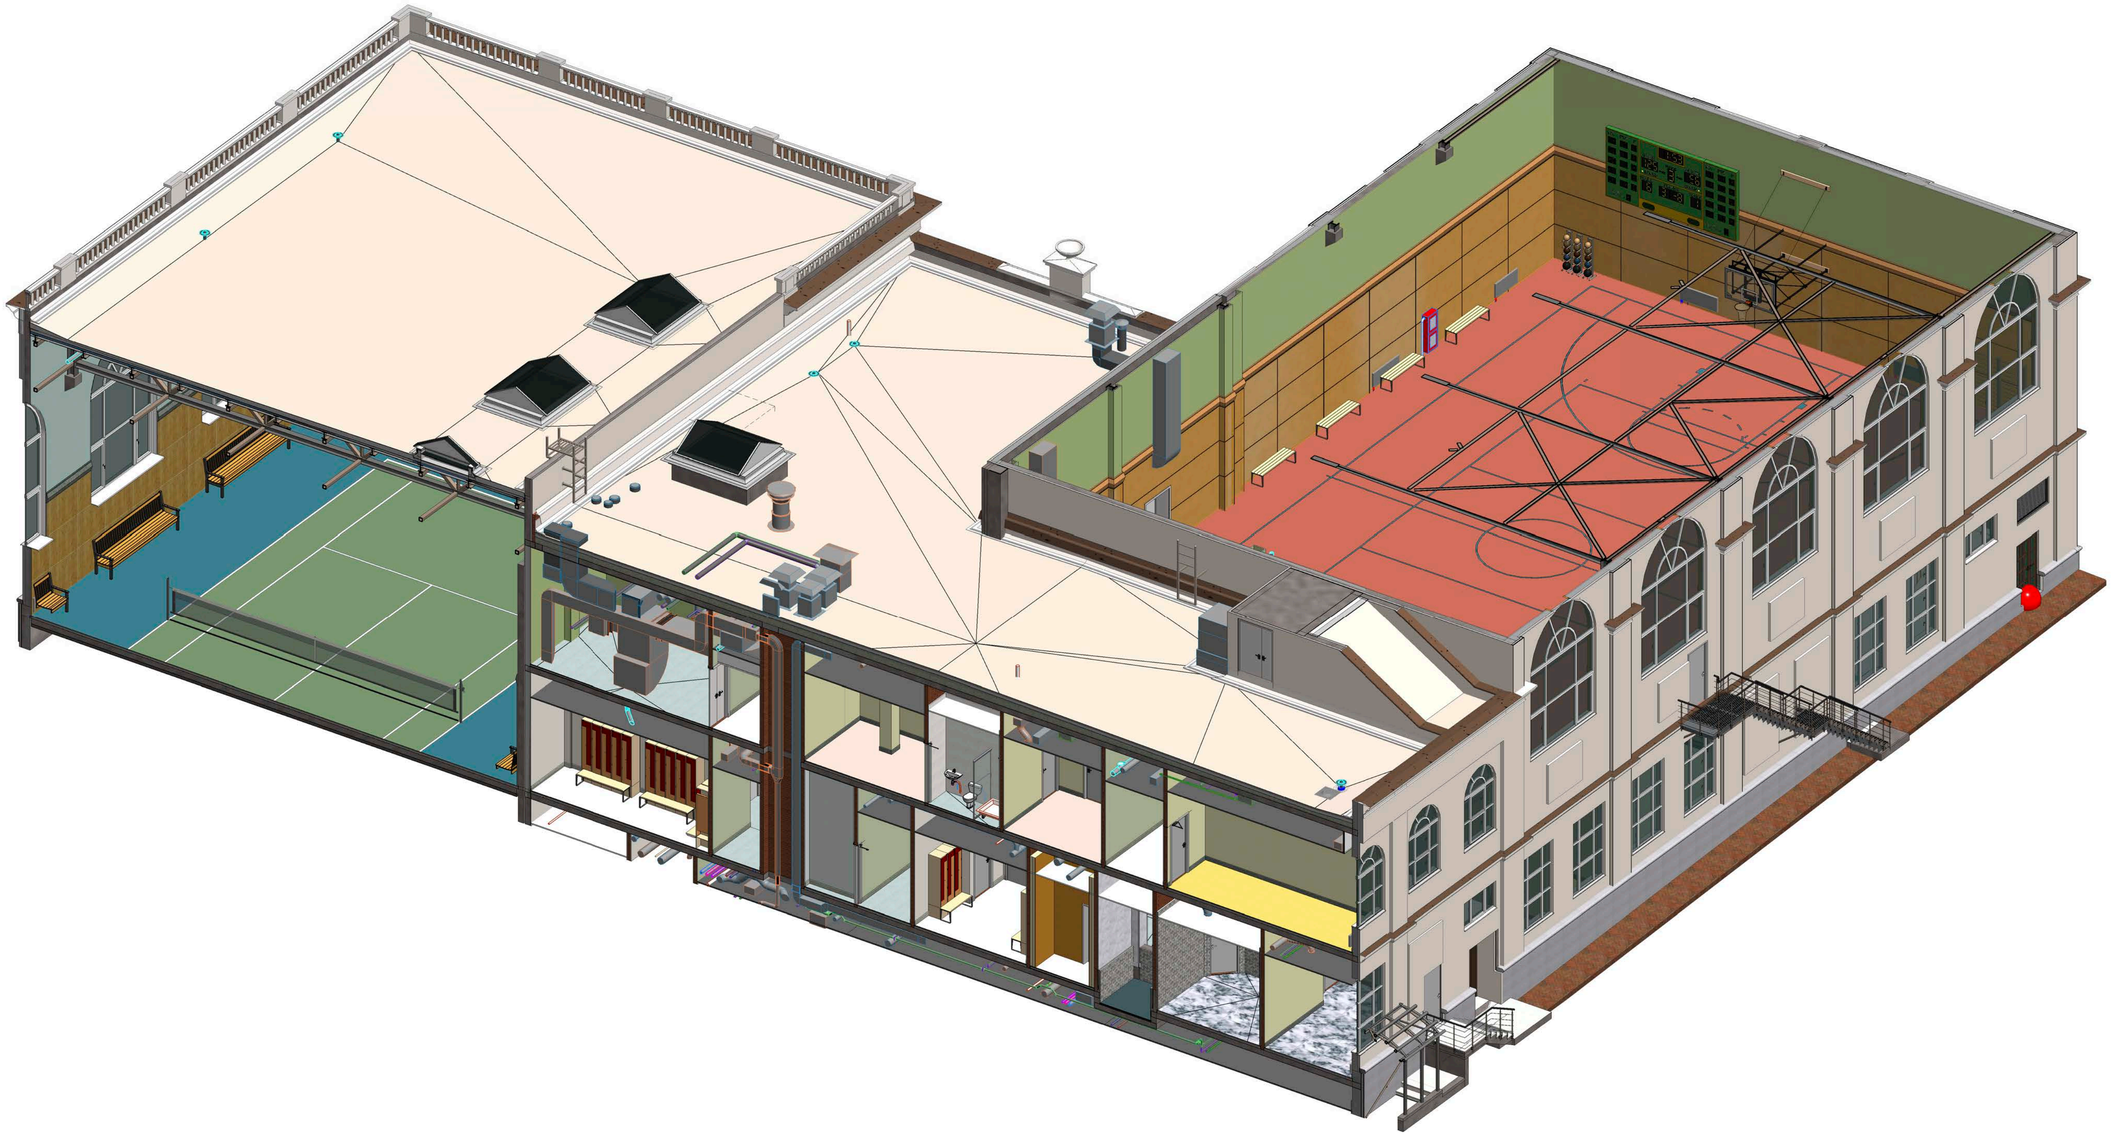
Лестница №5,см раздел КЖ
Металлическое ограждение(см. черт*.)
3.2
19
3
36
-1.200
Тип 4
Тип 4
+0.000
6
Тип 17
Подъемник для МГН